

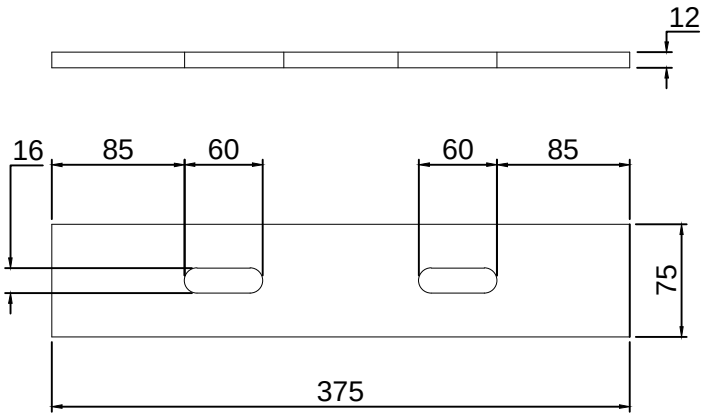


2 TOP PLATE

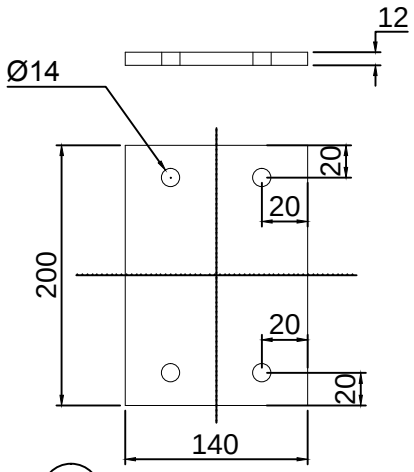

3 BASE PLATE

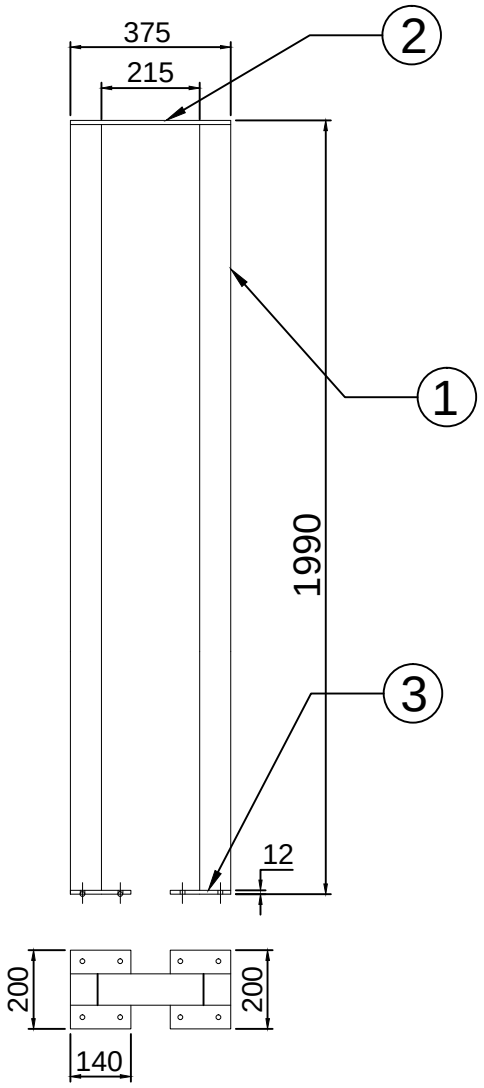

POST

SR.NO	DESCRIPTION	SPECIFICATION	QTY
5	NYLON WHEEL	Ø50 X 75L WITH M14 STUD	10 NOS
4	ANCHOR BOLT	M12 X 150L	40 NOS
3	PROFILE	140 X 12 X 200L	10 NOS
2	PROFILE	75 X 12 X 375L	5 NOS
1	SQ. TUBE	80 X 80 X 3.2 THK X 1965L	10 NOS

This drawing & designing is the property of NIHVA TECHNOLOGIES. Not to be sold or copied to any other concern.

TITLE: SLIDING GATE POST DRAWING

	NAME	SIGN	DATE
DRAWN	P.V.A		26.07.19
CHECK	V.M.T		26.07.19
APPROVAL			

If any queries contact : design@nihva.com

ALL DIMENSION ARE IN mm

NIHVA
NIHVA TECHNOLOGIES PVT. LTD.
NIHVA TECHNOLOGIES PVT. LTD. PUNE
Tel : 020 66304033
Website:- www.nihva.com
Email:- info@nihva.com

CLIENT -

PROJECT -

SITE LOCATION -

DWG. NO. : NIHVA/19-20/VDR/166 REV.:- R00

SCALE: NTS WT: SHEET: 01 OF 01