

LOAD DIAGRAM


Nominal static vertical loads are indicated. Value within brackets include dynamic surload factor 1.25 for door leaf loads in open position.
Includes items provided by ASSA ABLOY only.

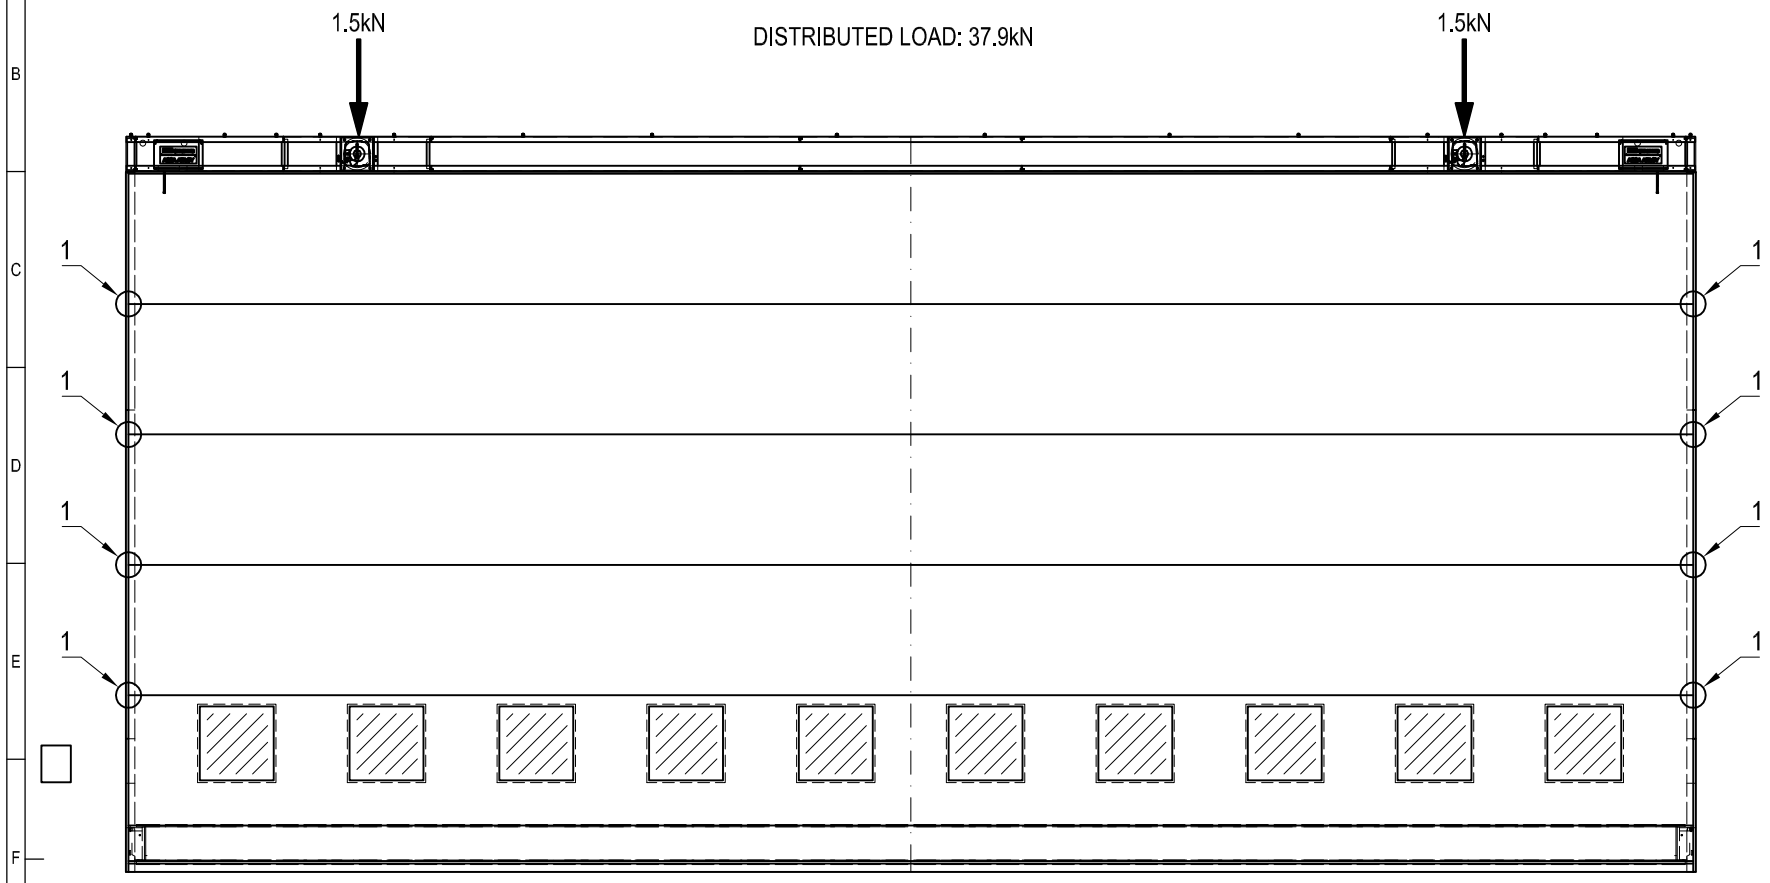


Interior view, Door closed

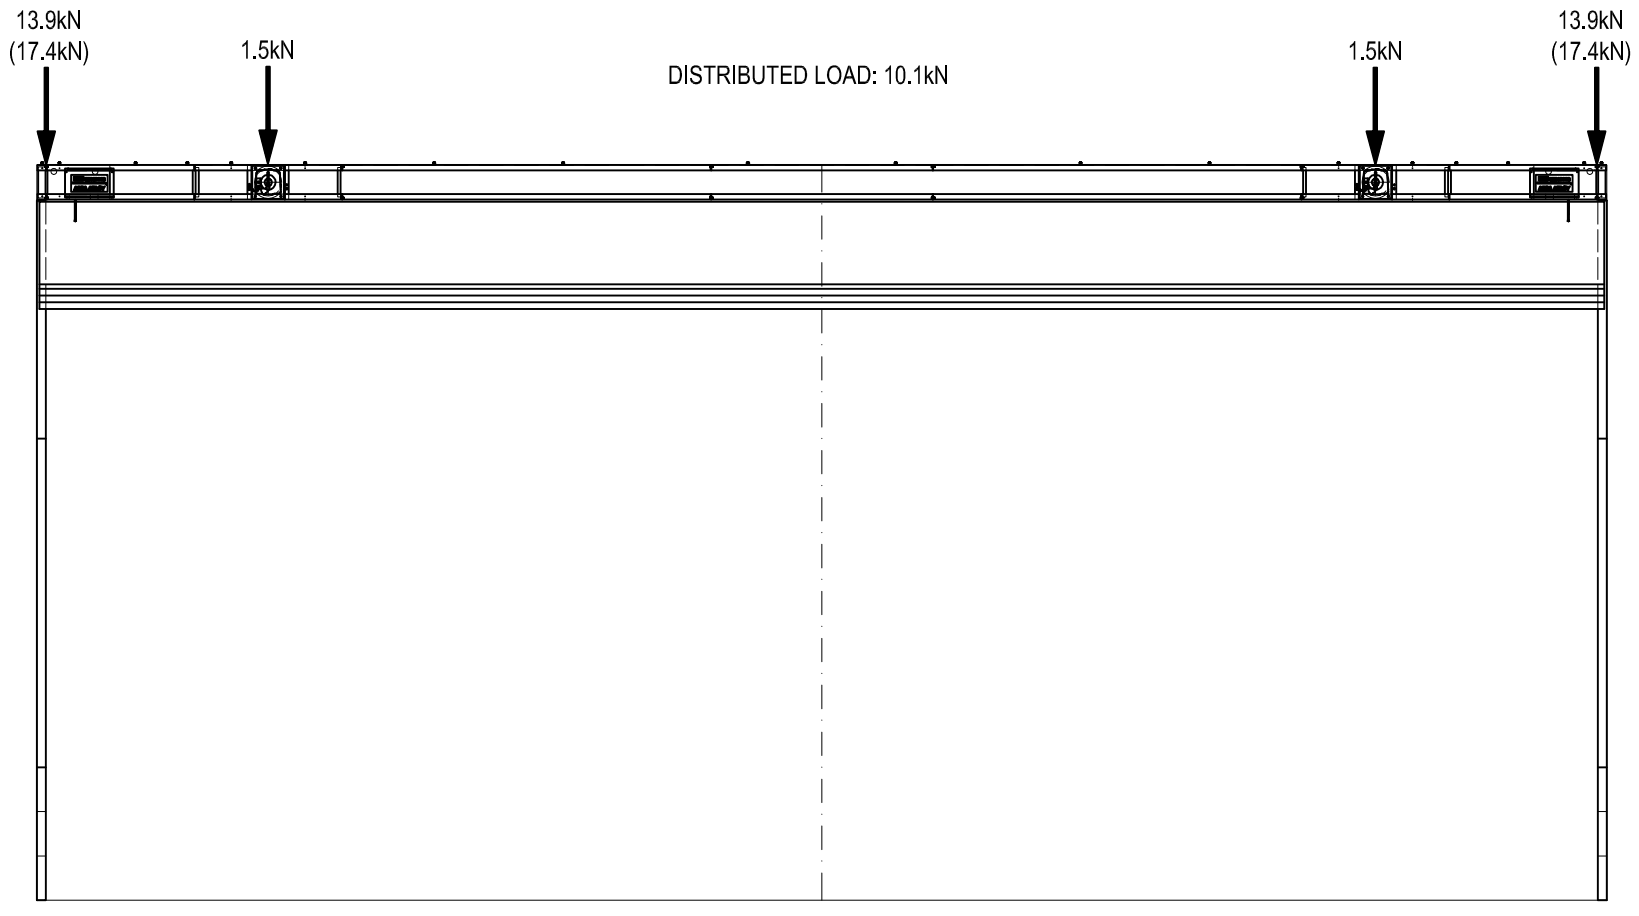


Interior view, Door open

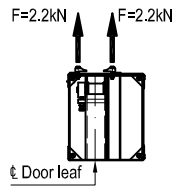

Load on header box attachment (each screw), due to wind load and door weight

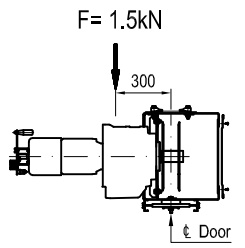

Section @ gear motor
Nord SK 973.1Z-100LA/4
Scale 1:20

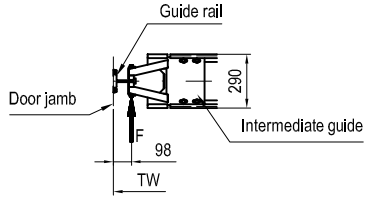

Force by differential pressure transferred to guide rail at each intermediate position.
(located at pos 1)
F=13.1 kN

NOT INCLUDED IN DOOR SUPPLY:

1. Design and supply of all door supporting structural components.
2. Design and supply of all closure between door and adjacent steel.
3. Door jambs adjustable for overall door width and true to plumb.
4. Paint job after completed door installation.
5. Any frameworks being provided by ASSA ABLOY will be clearly indicated as "by ASSA ABLOY".

REQUIREMENTS ON BUILDING:

6. Door head support must be straight within 1/600 of span in the in/out direction and free from protrusions of any kind.
7. For a single door leaf, door head support should be horizontal and straight within 1/600 of span at distributed full door load.
8. Door side jambs must be smooth, straight and parallel, out of plumb must not exceed 2mm/m (total deviation at full length 5 mm) in any direction.
9. Any footings at bottom of jamb columns must not interfere with installation of guide rails at floor level.
10. At time of installation, finished floor, free from obstructions, out to a distance of 2 m on each side of door centreline must be available.
11. Header box must be accessible from both sides during installation.

DOOR PROPERTIES:

12. The door is designed to withstand a differential pressure of 0.7kPa.
13. Guide rails, top- and intermediate beams in extruded aluminium with natural finish.
14. Environmental category: Megadoor standard
15. Bottom beam in carbon steel painted: Light grey (RAL7047)
16. Colored clamp strips on both sides: Yellow (RAL1003)
17. Door header box enclosed on both sides.
18. Color of header box: BLACK (NCS 9000-N. RAL 9005)
19. Vision panels 1200x1200 (10x)
20. The door fabric is a UV stabilized, flame retardant, self-extinguishing, PVC coated polyester fabric with fire technical properties Euroclass C-s2, d0 (according to EN 13501-1:2007). Colour of fabric: Yellow (RAL 1003)

ELECTRICAL:

21. One main control panel provided of PLC type.
22. Control mode : Impulse up / Constant contact down.
23. Cables are included.
24. Back-up power socket & switch.
25. Dry contacts, fire alarm.
26. Electrical tagging.
27. Approx. size of main control panel: WxHxD (600x800x250)
28. Location of main control panel: Left, inside view.
29. Aux. Voltage 24VDC
30. Power supply: 400V /3Ph /50Hz
31. Power: 7.7kW
32. Nom. current: 16.7A
33. Start current: 71.8A
34. (max. allowed voltage drop at start: 5%)

BELT HOIST UNITS:

2x NORD SK 973.1Z-100LA/4
75mm wide polyester belt. Rupture load 108kN/belt.

DOOR IDENTITY NUMBER: 83869001-003

INTERFACE DRAWING, ref. to drwng. no. 46290

DESIGNED	APPROVED	SIZE	SCALE
MÖ		A1	1:50

CODE 83869
ITEM NO
DATE 2015-01-20

If not otherwise stated:
Tolerances ISO 2768-m EN ISO 13920-B
Cutting class ISO 9013-442
Weld class ISO 5817-C
Surface finish Smooth raw surface

ASSA ABLOY

Bharat Forge-Alstom
India
Megadoor 21000 x 8000
Load diagram & Notes

DRAWING NO 46291
REVISION --
PLOT DATE

This document is the property of ASSA ABLOY Entrance Systems AB and shall not without our written permission be copied, imparted to a third party or used for any other unauthorized purpose.