



DRAWING

REV DESCRIPTION	DATE	REV NO
	20-11-2025	REV 00
1.		

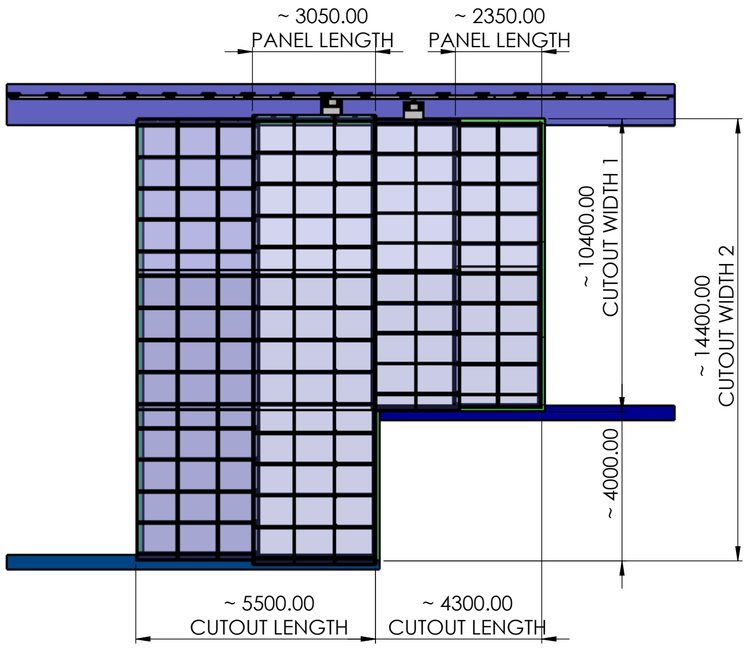


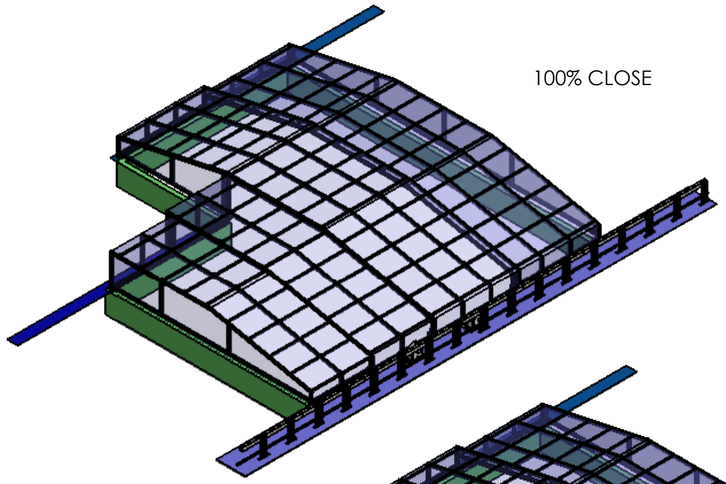

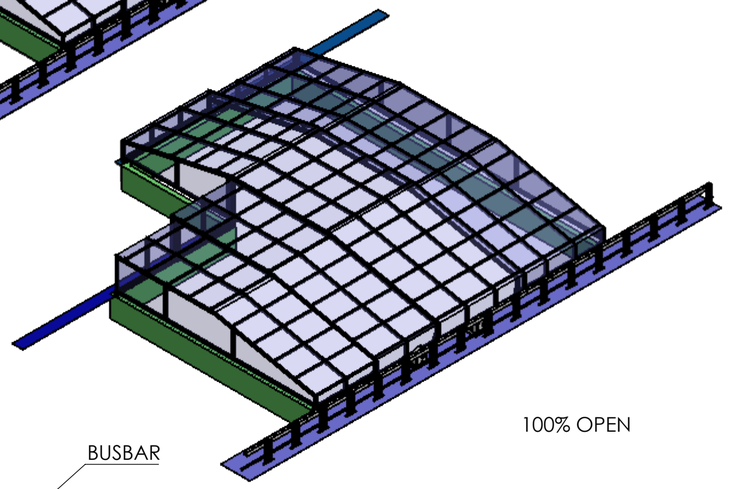

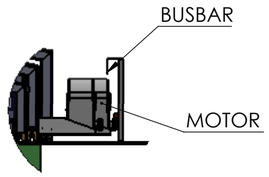


DETAIL B
SCALE 1 : 30

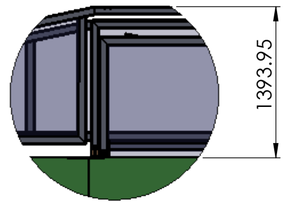

DETAIL D
SCALE 1 : 40

SLIDING DIRECTION



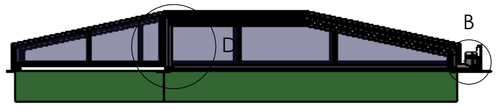

TECHANICAL SPECIFICATIONS

ROOF COVERING MATERIAL	3 MM PC SHEET
GUIDE RAILS	GUIDE RAILS T-75-1B (M.S)
ROLLING WHEEL	NIHVA MAKE
MOTOR	1) MAKE - NICE 2) CAPACITY - 1000 OR 600KG 3) POWER SUPPLY - 230V 4) POWER DRAW - 2.3A 5) POWER - 450W 6) SINGLE PHASE BI-DIRECTIONAL MOTOR 7) MECHANICAL LIMIT SWITCH
PANEL STRUCTURE	M.S RECT. TUBE & AL STRIPS
HARDWARE	SS 304
MECHANISAM	RACK AND PINION ARRANGEMENT
RAL SHADE	AS PER CLIENT

NOTE :
THIS DRAWING ONELY FOR CONCEPT

SPECIAL INSTRUCTION'S :

TITLE - ROOF AUTOMATION

DWG NO - NTPL-000-PM-001-00-00-00

NIHVA Technologies Pvt. Ltd.
NIHVA TECHNOLOGIES PVT.LTD.PUNE
Website - www.nihva.com

	NAME	SIGNATURE	DATE
DRAWN	J.P.		20-11-2025
CHK'D	B.S.		20-11-2025
APPV'D	V.T.		20-11-2025

PRODUCT - RETRACTABLE ROOF
PROJECT NO - NTPL-000-PM
REVISION - 00
SITE LOCATION - HYDERABAD
MATRIAL -
QTY - 1
If any queries contact - Design@nihva.com
PROJECTION METHOD:
SCALE :
ALL DIMENSION ARE IN mm
A2
SHEET 1 OF 1