
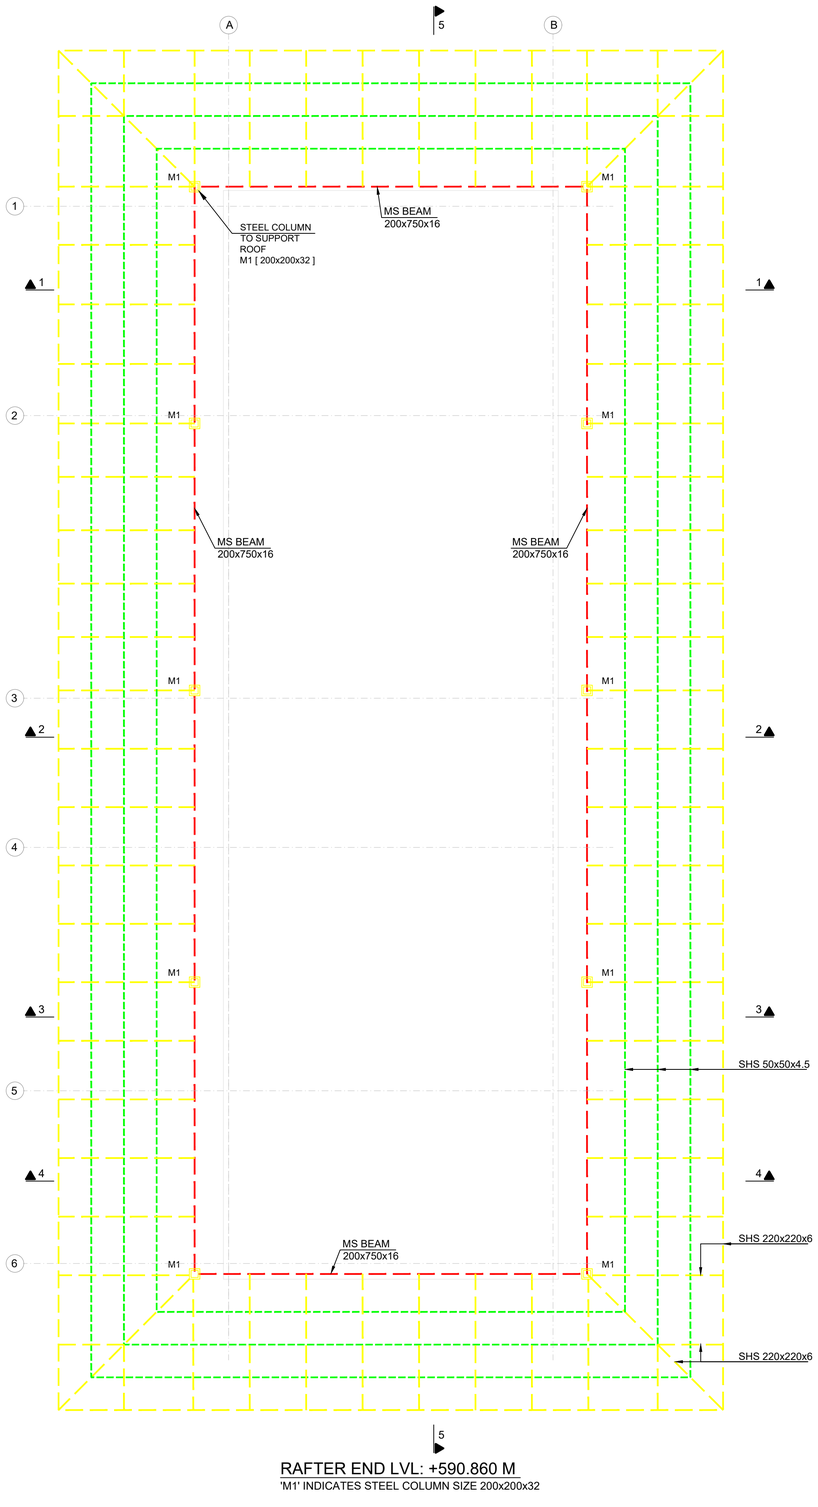


RAFTER END LVL: +590.860 M

'M1' INDICATES STEEL COLUMN SIZE 200x200x32

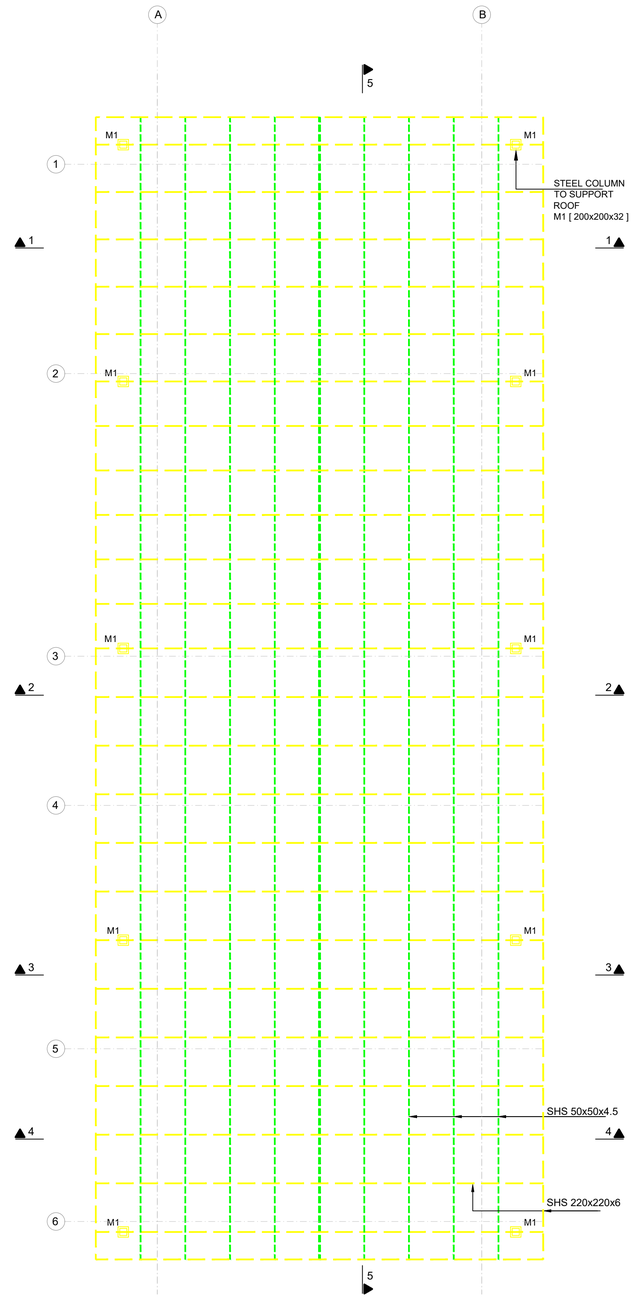

RAFTER TOP LVL: +597.355 M

'M1' INDICATES STEEL COLUMN SIZE 200x200x32