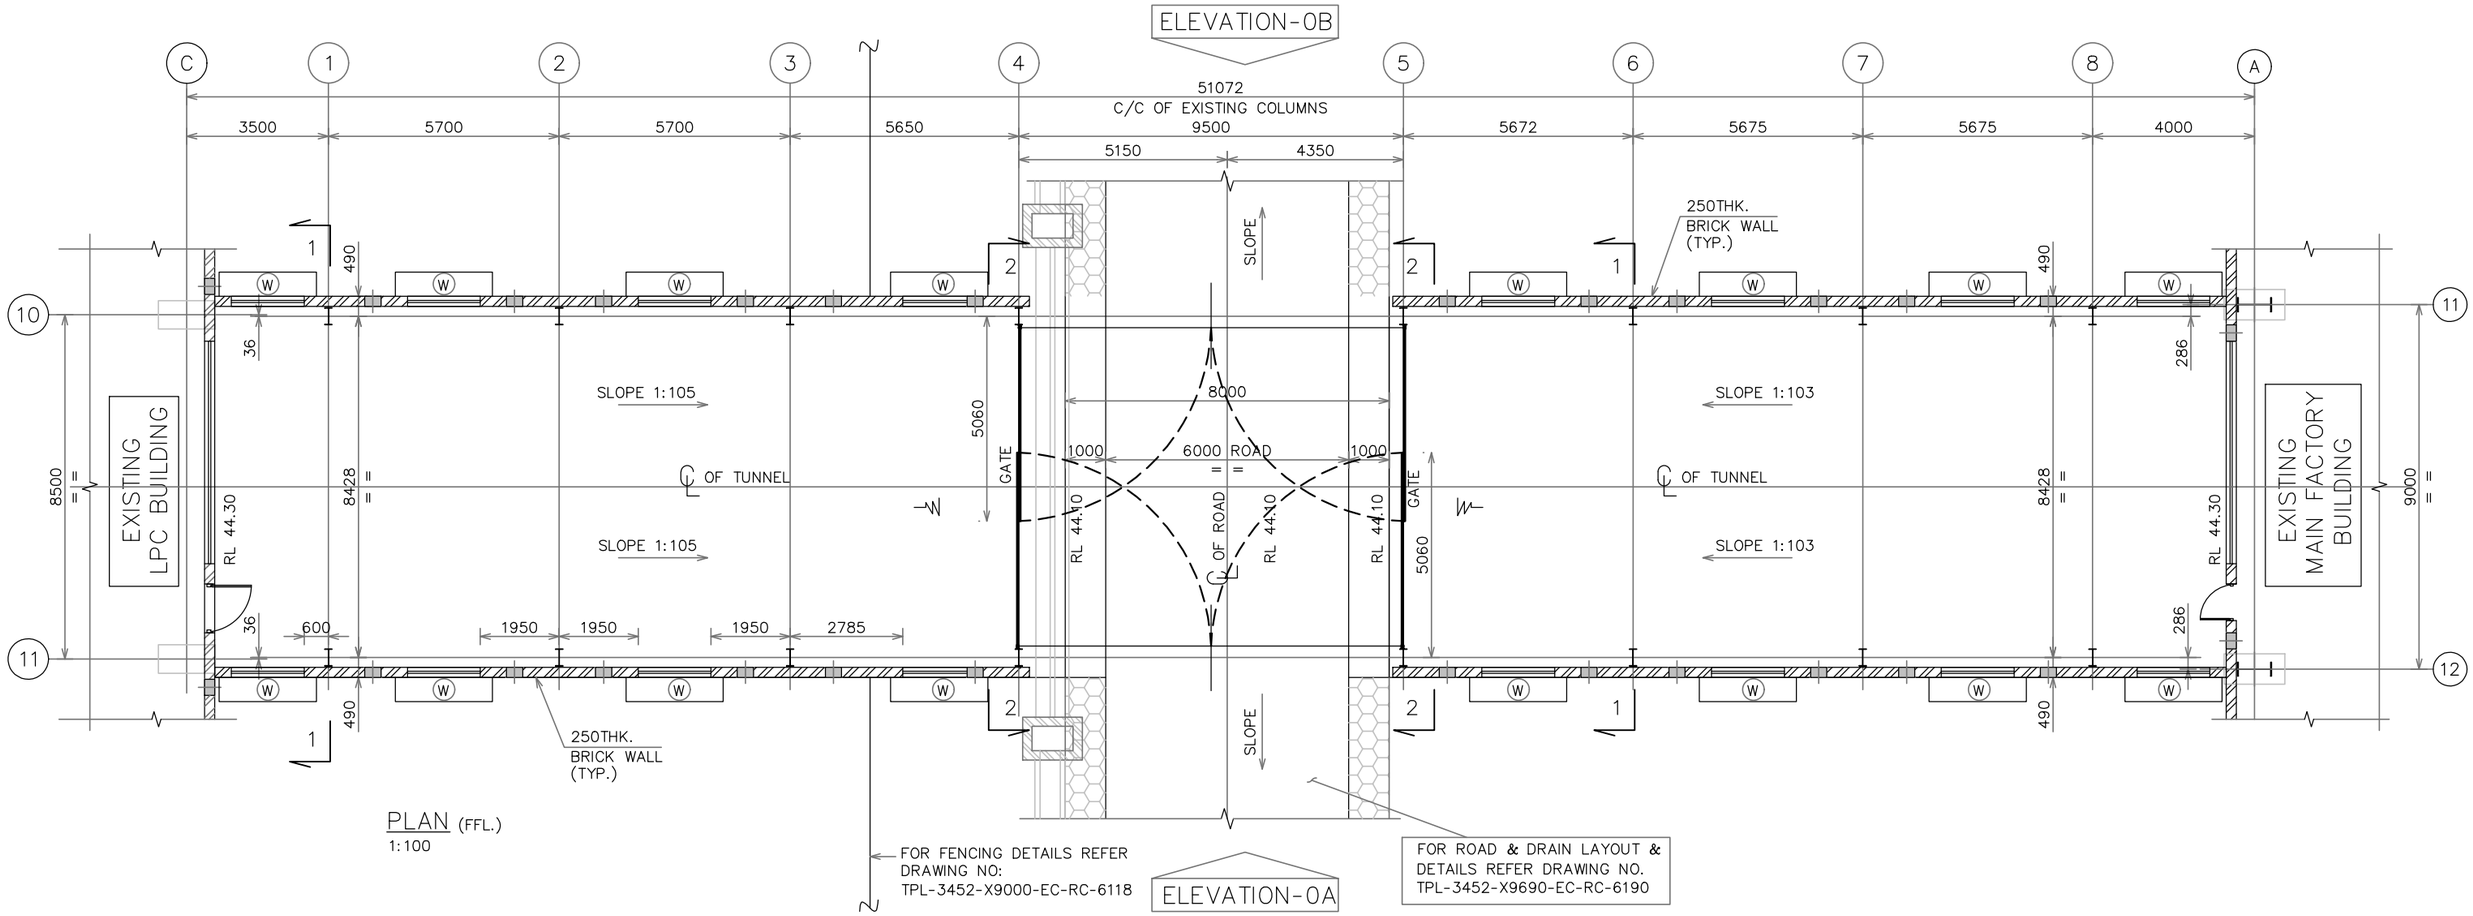
ELEVATION-0B
C
1
2
3
4
5
6
7
8
A
10
11
12
51072
C/C OF EXISTING COLUMNS
3500
5700
5700
5650
9500
5672
5675
5675
4000
5150
4350
250THK.
BRICK WALL
(TYP.)
SLOPE
490
36
286
SLOPE 1:105
SLOPE 1:103
8000
5060
GATE
1000
6000 ROAD
1000
℄ OF TUNNEL
℄ OF ROAD
RL 44.10
RL 44.30
8500
8428
9000
EXISTING
LPC BUILDING
EXISTING
MAIN FACTORY
BUILDING
600
1950
1950
1950
2785
250THK.
BRICK WALL
(TYP.)
PLAN (FFL.)
1:100
FOR FENCING DETAILS REFER
DRAWING NO:
TPL-3452-X9000-EC-RC-6118
ELEVATION-0A
FOR ROAD & DRAIN LAYOUT &
DETAILS REFER DRAWING NO.
TPL-3452-X9690-EC-RC-6190