



Note:--

1.All dimension are in MM
2.All Civil work will be in client scope
3.Manufacturing,civil and installation tolerance will be ±10mm
4.Top and Bottom track should be in parallal within ±3mm
5.If structure required for the top track mounting will be client scope
6. Dimension may vary beacuse site visite not done yet
7. 4leaf door weight will be 1640kg

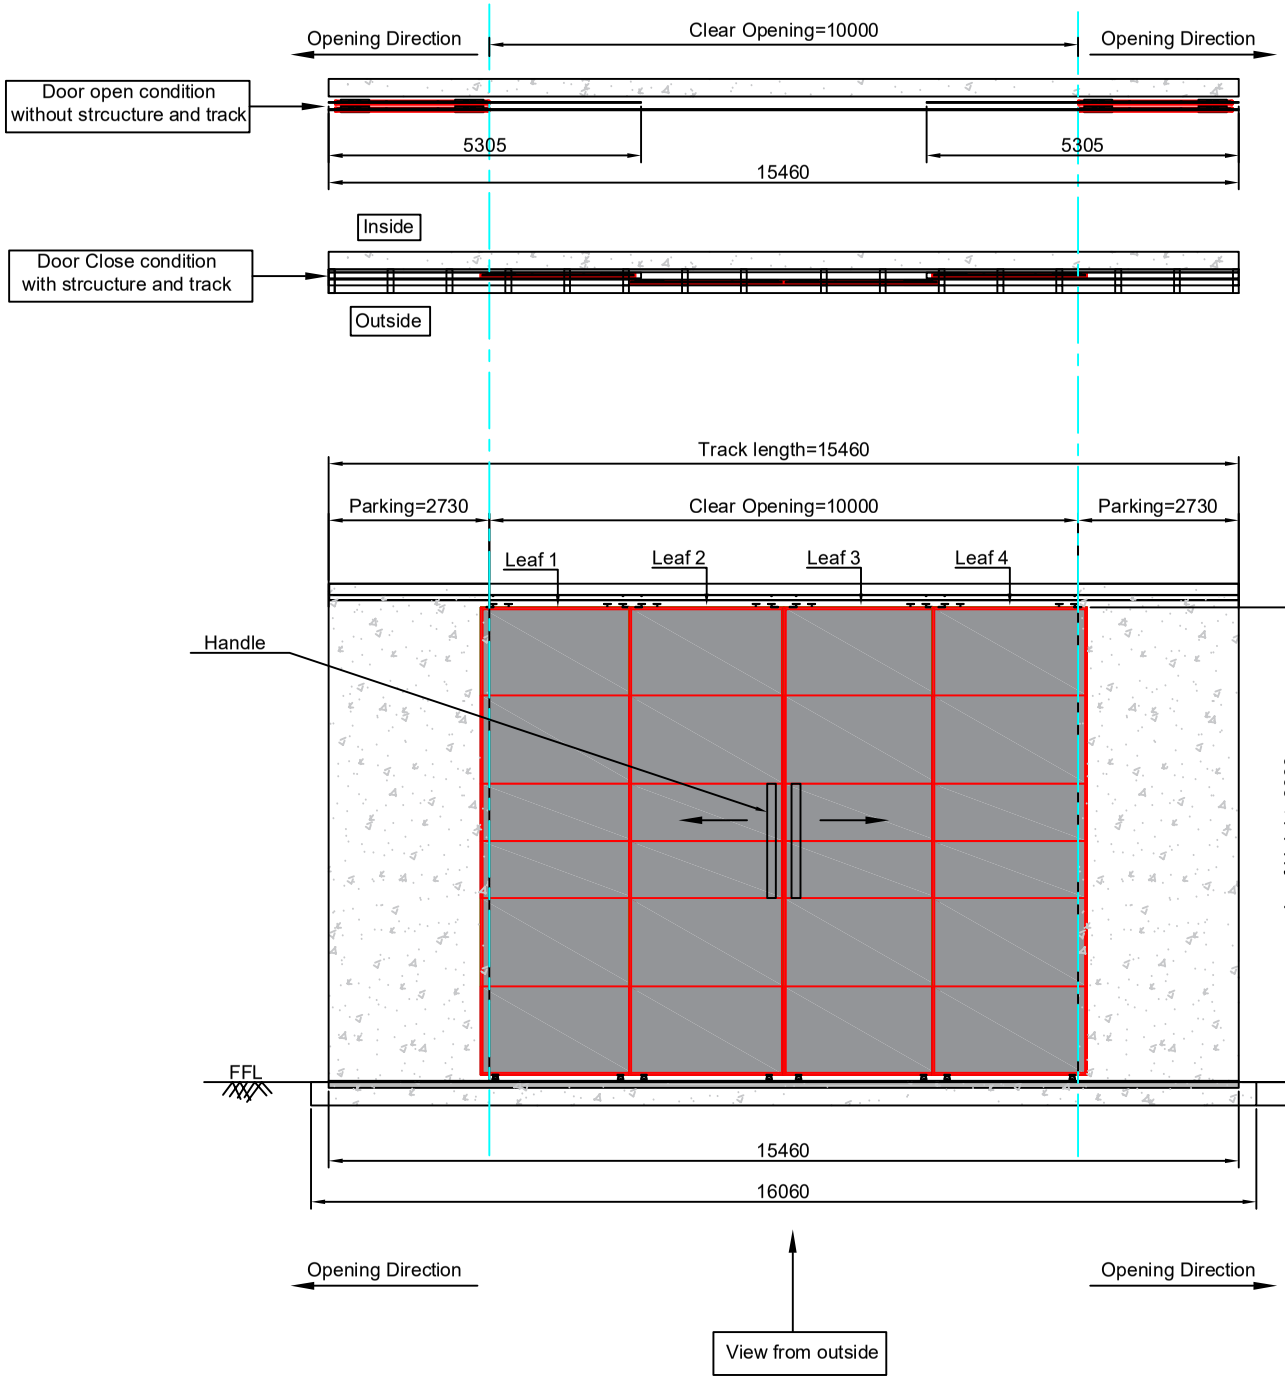

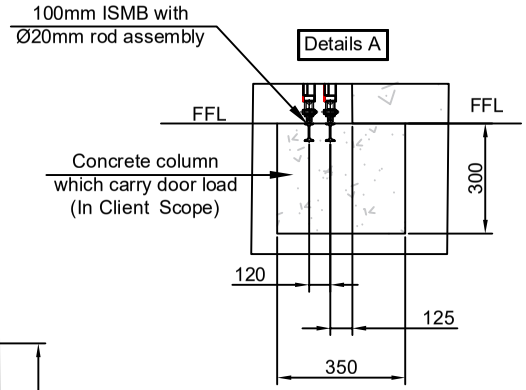

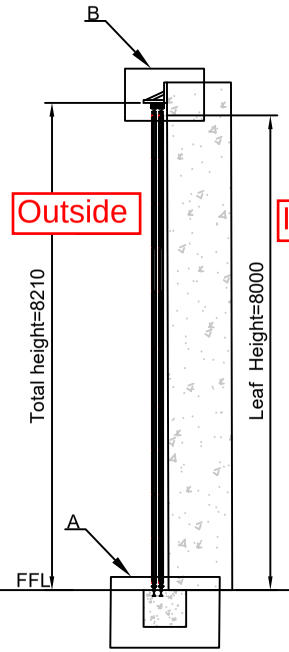

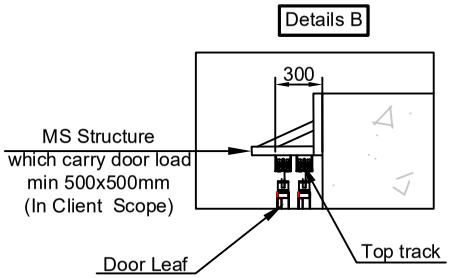

This drawing & design is the property of NIHVA TECHNOLOGIES. Not to be sold or copied to any other concern.

TITLE:- GA DRAWING DOR MANUAL SLIDING DDOR

NIHVA TECHNOLOGIES PVT. LTD.

	NAME	DATE	SIGN
DRAWN	SUJATA	03/11/2022	
CHECK	A.K	03/11/2022	
APPRD.	V.T	03/11/2022	

CLIENT - BESTALL
LOCATION -
PRODUCT - SLIDING DOOR
DWG NO:-NIHVA/22-23/CLT/0037 REV- 01
ALL DIMENSION ARE IN mm
SCALE: NTS SCALE:-- 1:1 SHEET: 01 OF 01

Rev.No	Revision	Date	Revised By
1.	Required structure dimension and total door height has been mentioned	23/02/2023	Sujata