



DRAWING

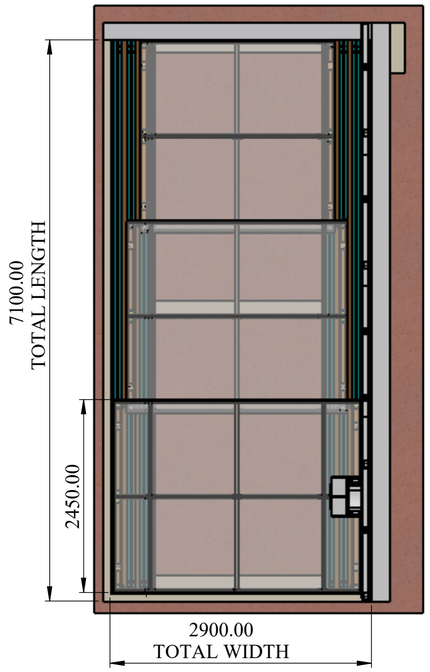

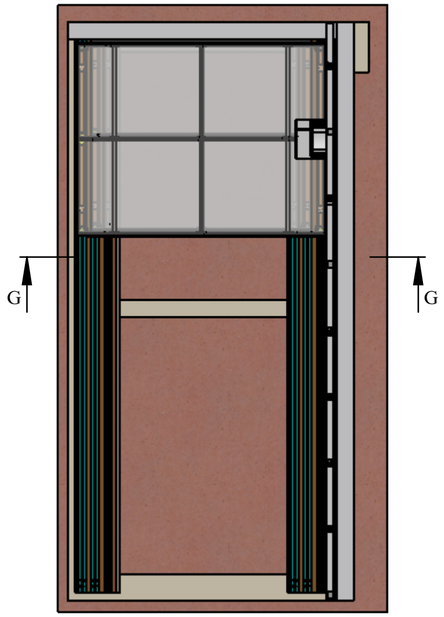


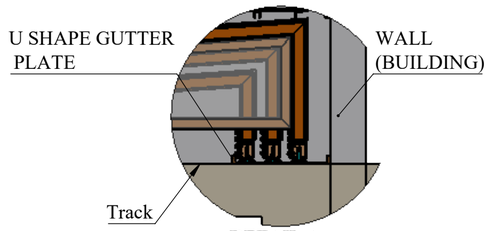


DETAIL A
SCALE 1 : 25

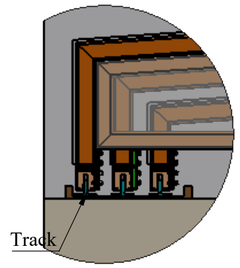


DETAIL B
SCALE 2 : 35

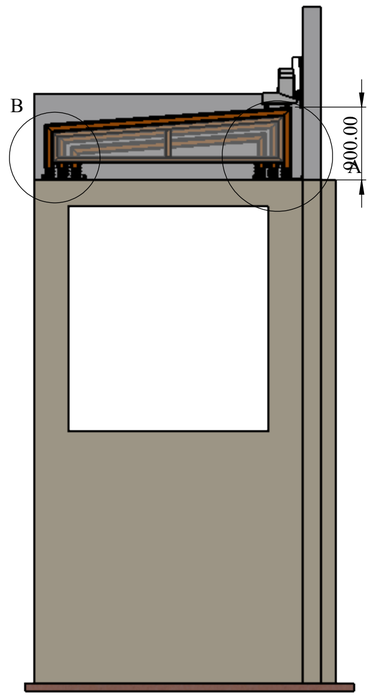

CLOSE VIEW

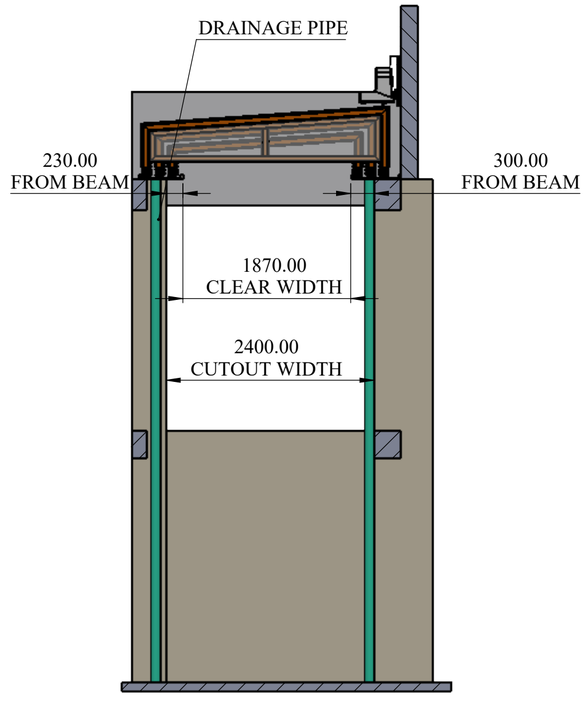

SECTION G-G
SCALE 1 : 50

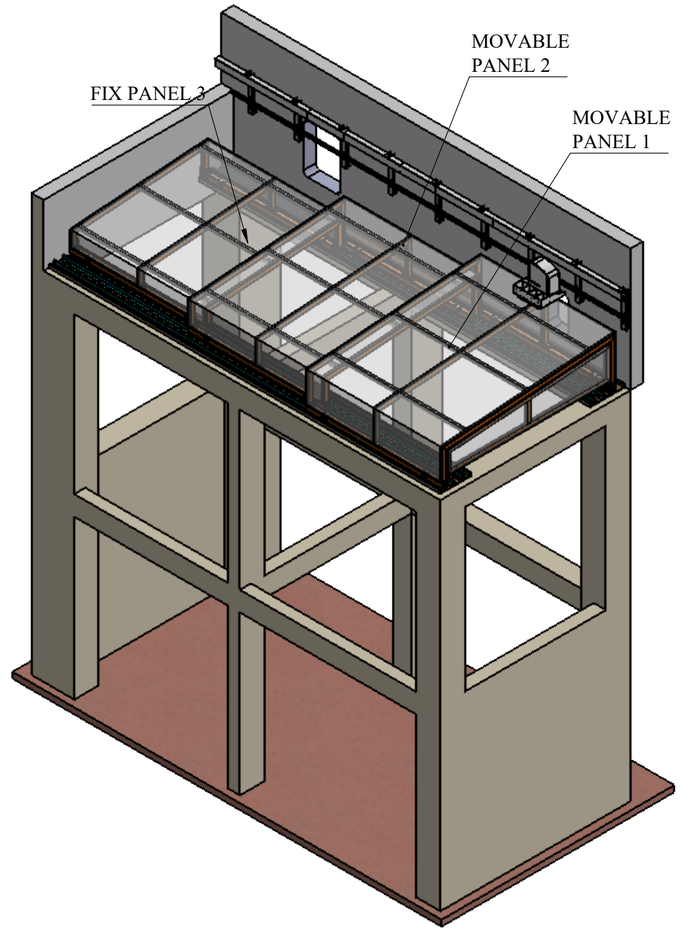

REV DESCRIPTION	DATE	REV NO
	29-04-2026	REV 00
1.		

NOTE :

SPECIAL INSTRUCTION'S :

TITLE - ROOF AUTOMATION				NIHVA TECHNOLOGIES PVT.LTD.PUNE
DWG NO - NTPL-000-PM				Website - www.nihva.com
	NAME	SIGNATURE	DATE	PRODUCT - RETRACTABLE ROOF
DRAWN	V.W.		29-04-2026	PROJECT NO - NTPL-000-PM / REVISION - 00
CHK'D	B.S.		30-04-2026	SITE LOCATION - MUMABI / WEIGHT -
APPV'D	V.T.		30-04-2026	MATRIAL - / QTY - 1
If any queries contact - info@nihva.com				PROJECTION METHOD: / SCALE :
ALL DIMENSION ARE IN mm		A2		SHEET 1 OF 1