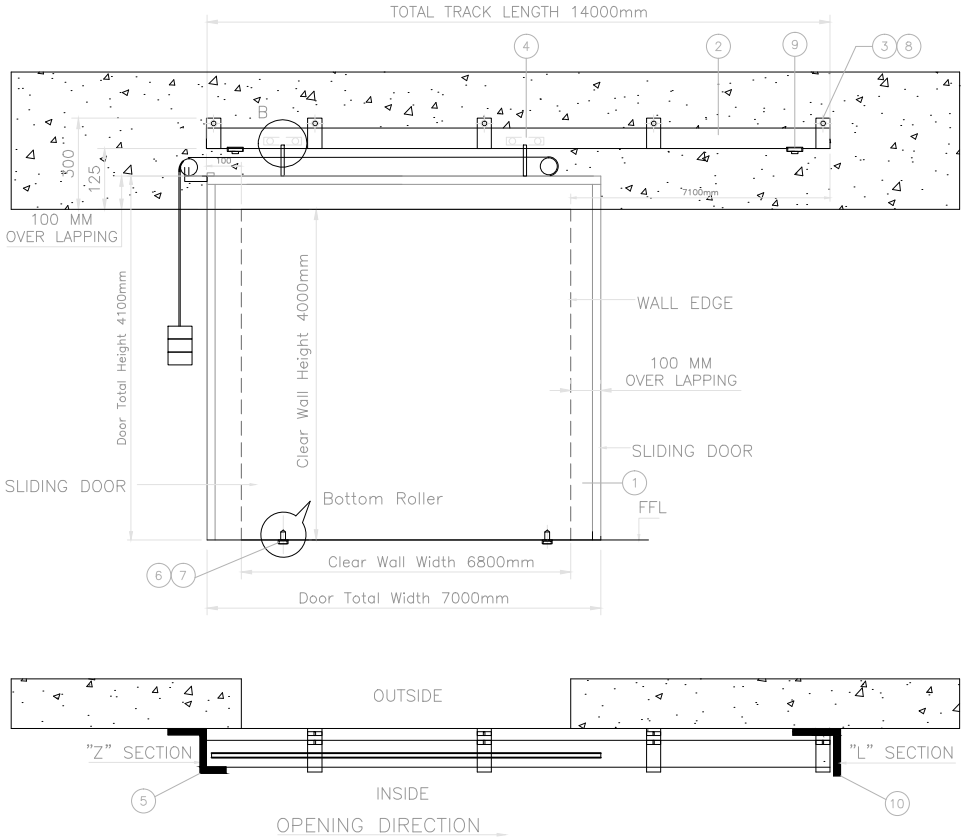

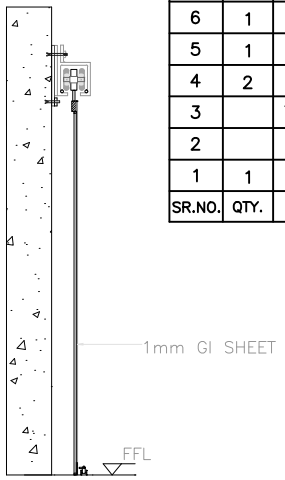

SR.NO.	QTY.	DESCRIPTION
10	1	'L' SECTION
9	1	STOPPER (FOR HANGER ASSLY.)
8	1	COVER (FOR TRACK BKT.)
7	1	BOTTOM ROLLER MTG. FLAT (BOTTOM ROLLER BKT.)
6	1	BOTTOM ROLLER ASSLY.
5	1	'Z' SECTION
4	2	HANGER ROLLER ASSLY.
3		TRACK BRACKET
2		SLIDING TRACK
1	1	SLIDING DOOR & FRAME / BACK SUPPORT SQ. TUBE

DOOR DIMENSION		
CLEAR WIDTH	CLEAR HEIGHT	
6800mm	4000mm	01NOS

REV. NO	DATE	DRAWN	DESCRIPTION	SIGN.
R01	27-07-2018	SURAJ	1.DOOR SIZE CHANGED	

NOTE : DOOR OVERLAPING 100mm AT RH & LH AND TOP SIDE
ALL DIMENSIONS ARE IN MM.
CLIENT SHOULD CONFIRM DOOR OPENING DIRECTION.

TOLERANCE:- ± 10mm

This drawing & designing is the property of NIHVA TECHNOLOGIES. Not to be sold or copied to any other concern.

TITLE
MANUAL SLIDING DOOR

NIHVA
NIHVA TECHNOLOGIES PVT. LTD.

NIHVA TECHNOLOGIES PVT. LTD. PUNE
Tel : 020 66304033
Email:- info@nihva.com
Website:- www.nihva.com

	NAME	SIGN	DATE
DRAWN	SURAJ		10/07/18
CHECK	R.D		10/07/18
APPROVAL	R.D		10/07/18

CLIENT - REWARD CONSTRUCTIONS PVT LTD.
PROJECT - REWARD CONSTRUCTIONS PVT LTD.
SITE - RANJANGAON MIDC.

If any queries contact : design@nihva.com
ALL DIMENSION ARE IN mm
DWG. NO. : NIHVA/18-19/0053/R01 REV- 01
SCALE: NTS WT: SHEET: 01 OF 01