


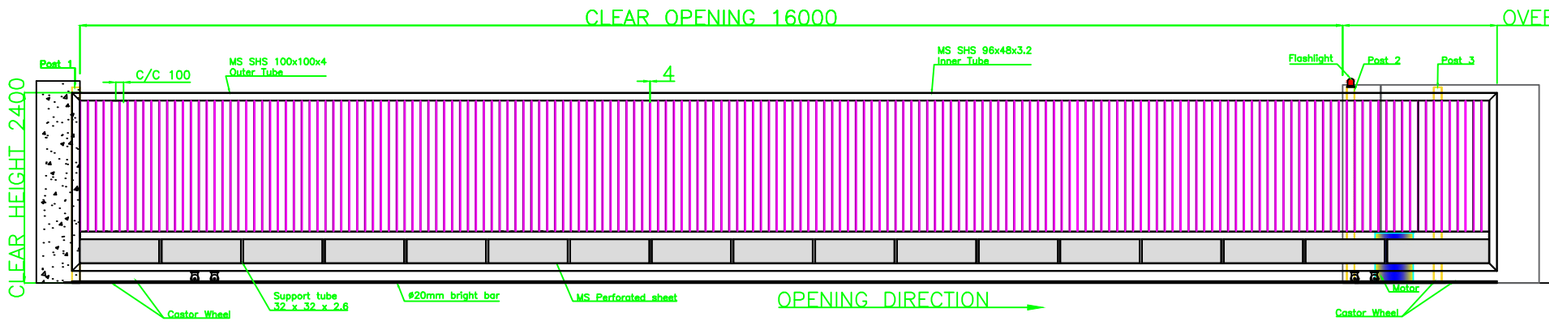


ELEVATION VIEW
(INSIDE)

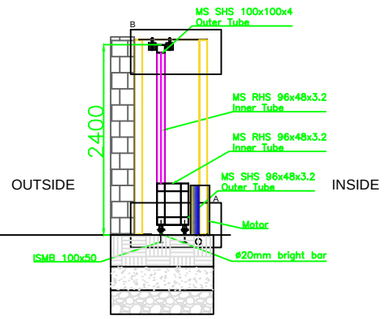


SIDE VIEW

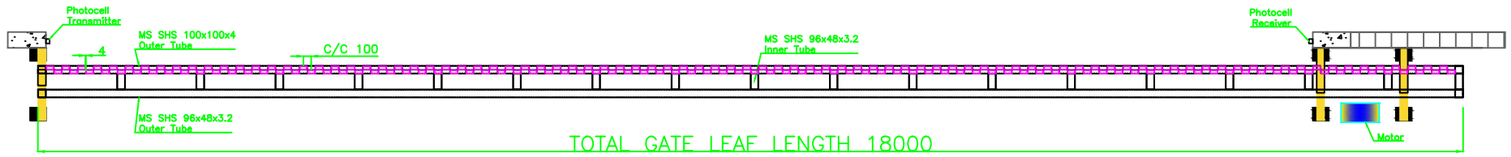

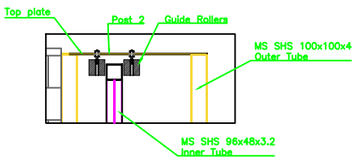

DETAIL B

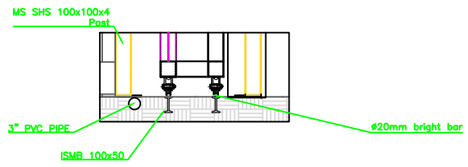

DETAIL A

Technical Specs of Motorized Sliding Gate

1. Opening length - 16000mm
2. Gate Height - 2400mm
3. Parking length required - 18200mm
4. Outer tube size - MS SHS 100x100x4mm
5. Inner tube size - MS RHS 96x48x3mm
6. Bottom Rail - Bright bar Ø20mm
7. Post size - MS SHS 100x100x4mm
8. T`Safety feature - Photocell and flashing light
9. Paint: RAL 7044

Note-

1. All dimension are in mm.
2. All civil work is under client scope.
3. 3" PVC pipe in the foundation to be provided by client.
4. 3PH power required near motor.

Rev 01- (23-02-2022)

1. Tube sizes changed from 100 x 50 to 96 x 48.
2. Tube mounting changed as per client requirement.
3. Distance between the roller increased for cladding.

Rev 02- (24-02-2022)

1. Mentioned the gap between the tube 4mm.
2. Mentioned the C/C distance 100mm.
3. Added RCC details in drawing

Rev 03- (05-03-2022)

1. Added RAL Shade.

This drawing & design is the property of NIHVA TECHNOLOGIES. Not to be sold or copied to any other concern.

TITLE: MOTORIZED SLIDING GATE				NIHVA TECHNOLOGIES PVT. LTD. PUNE Tel : 020 66304033 Email:- info@nihva.com Website:- www.nihva.com	
	NAME	SIGN	DATE	CLIENT - SRF	
DRAWN	G.P.		23.02.22		
CHECK	A.K.		23.02.22	LOCATION - INDORE	
APPRD.	V.T.		23.02.22	PRODUCT - MOTORIZED SLIDING GATE	
If any queries contact : design@nihva.com				NIHVA\21-22\CLT\344	REV- 3
ALL DIMENSION ARE IN mm				SCALE: NTS	SHEET: 01 OF 01