
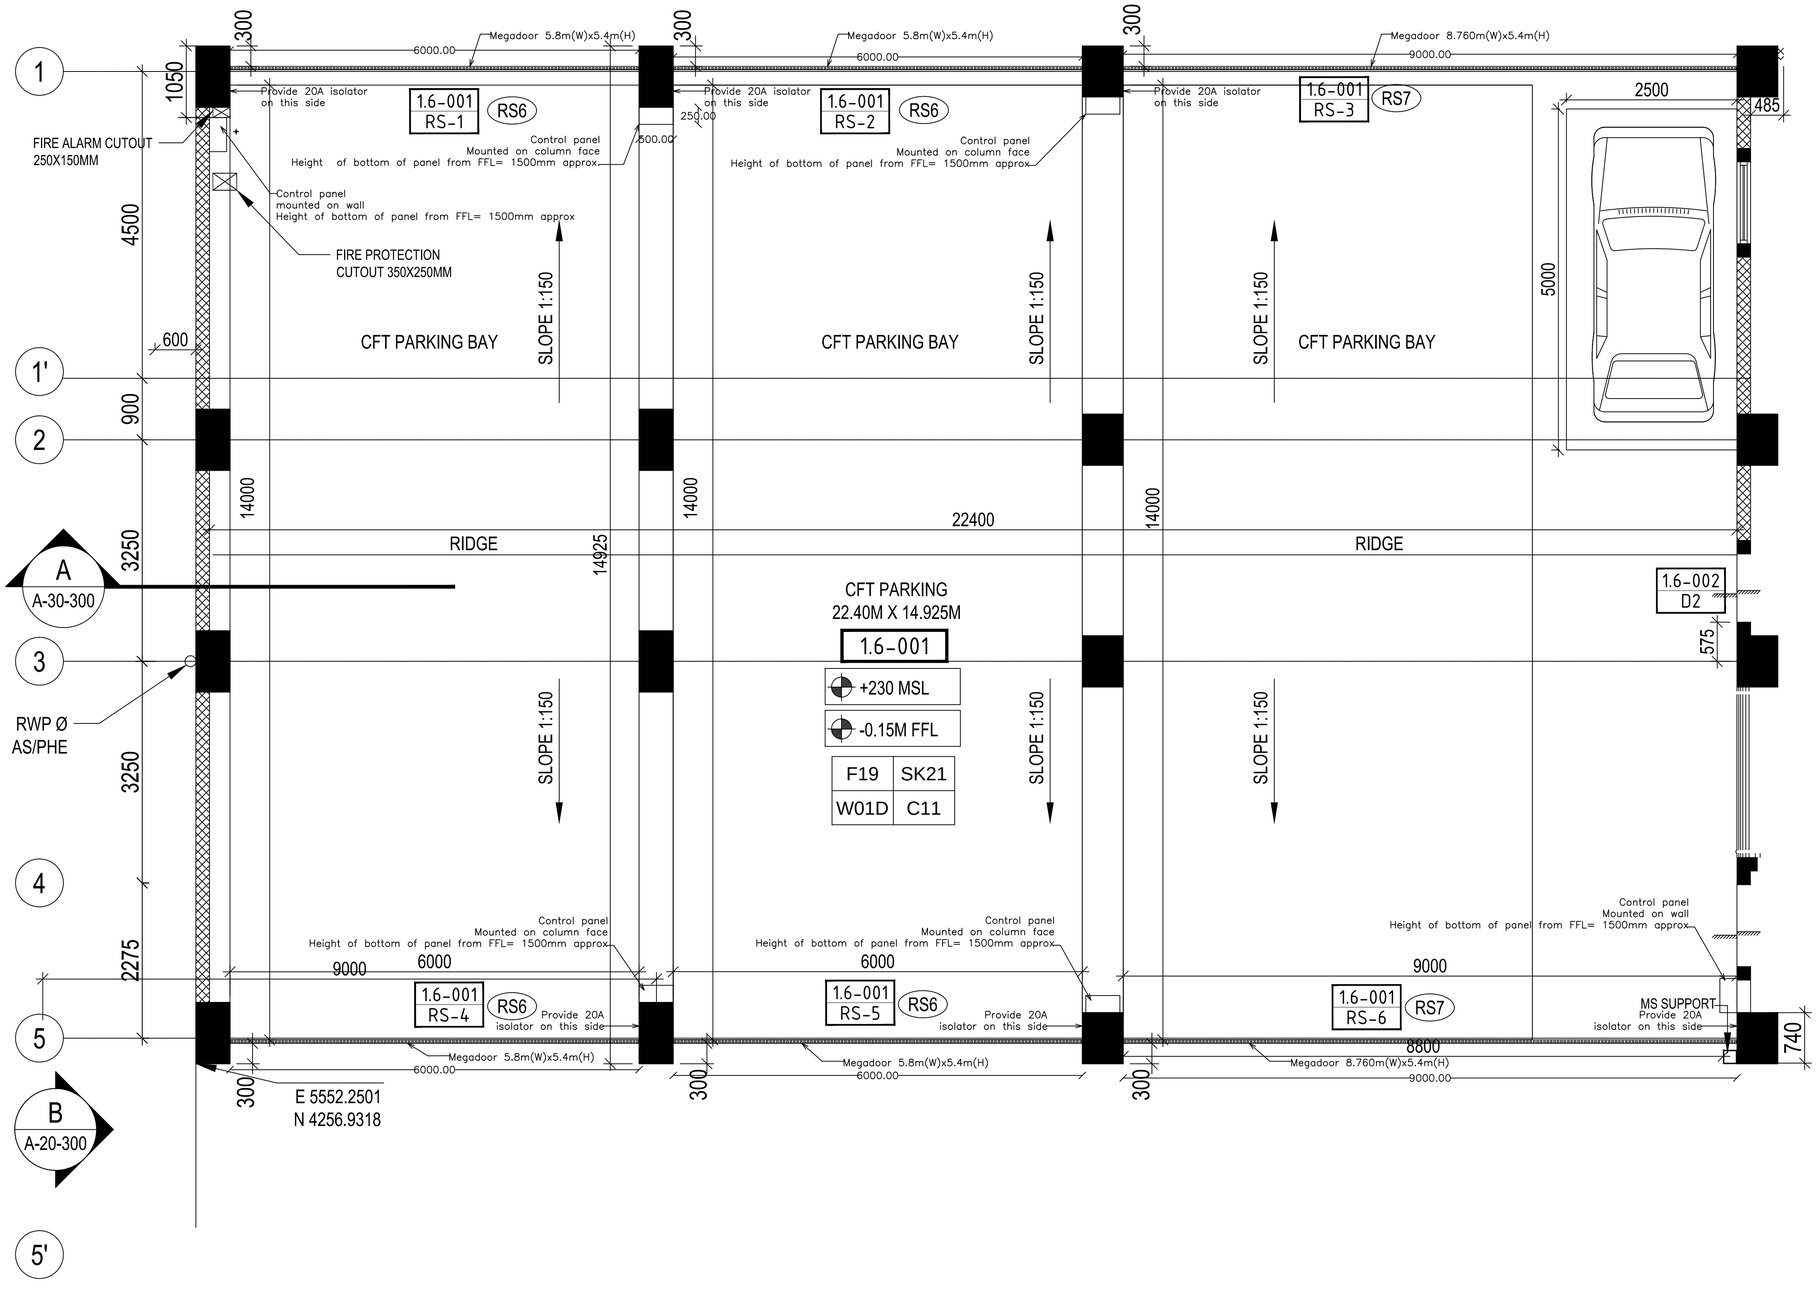


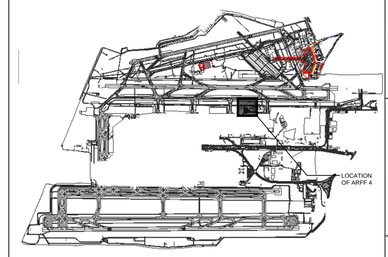

KEY PLAN (NOT TO SCALE)

REFERENCE DRAWING :

DIAL-LT-D-UTL-A-20-300 : ARFF4 FIRE STATION
GROUND FLOOR PLAN

SHOP DRAWING

REV.NO.	DESCRIPTION	DESIGNED	DRAWN	CHECKED	APPROVED
A	Shop drawing issued for construction.	24.11.2021 GJP	24.11.2021 GJP		

REVISIONS

CHECKED BY	SIGN	DATE	CHECKED BY	SIGN	DATE	CHECKED BY	SIGN	DATE
ARCHITECTURE			HVAC			QS		
CIVIL & STRUCTURAL			FPS			GEOTECH.		
ELECTRICAL			PIPING			AIRPORT SYSTEMS		
ELV SYSTEM			PHE			INTERFACE		

DELHI INTERNATIONAL AIRPORT LIMITED

PROJECT: INDIRA GANDHI INTERNATIONAL AIRPORT PHASE-3A DEVELOPMENT WORKS

CLIENT :

CONCEPT : AECOM

PROJECT CONSULTANT: Engineering Design and Research Center (EDRC), L&T Construction

INSTALLED AND SUPPLIED BY: NIHA TECHNOLOGIES PVT LTD

JOBNO.

JOB No :	NAME	SIGN	DATE
DSGN	GJP		02.10.2021
DRWN	GJP		02.10.2021
CHKD			
APPD			

TITLE: Control panel locations

SCALE: 1:100,1:50

DRAWING No. DIAL-LT-Q-UTL-A-10-105

SHEET:

PROJECTION: FIRST ANGLE

SIZE: A1

REV: A

RELEASED FOR: ☐ PRELIMINARY ☐ TENDER ☐ INFORMATION ☐ APPROVAL ☑ CONSTRUCTION