


TOP VIEW

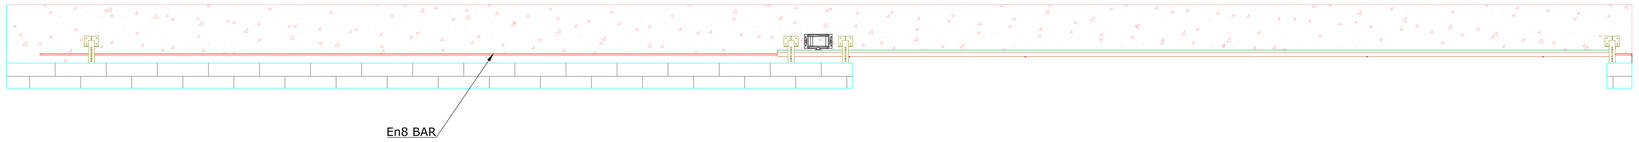


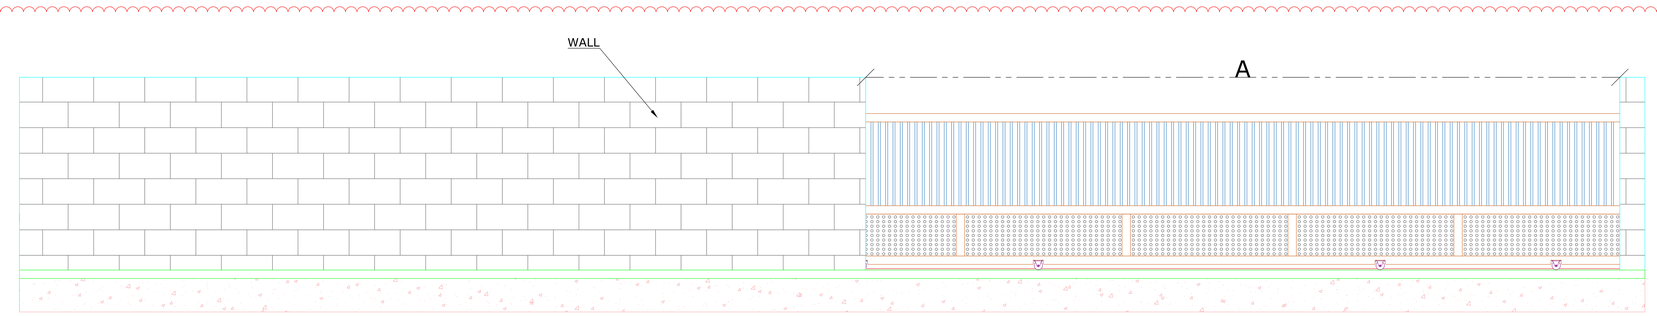


FRONT VIEW

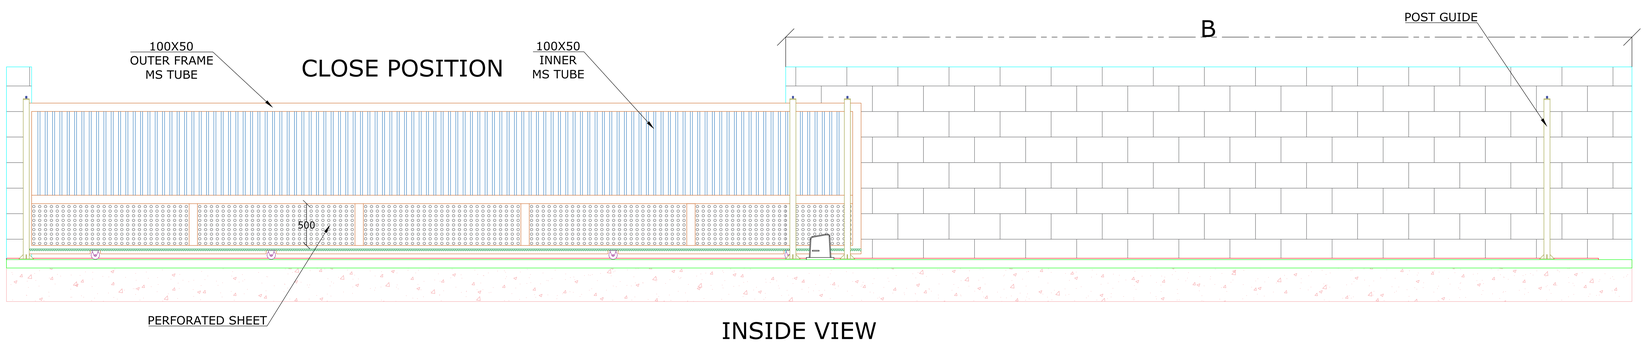


INSIDE VIEW

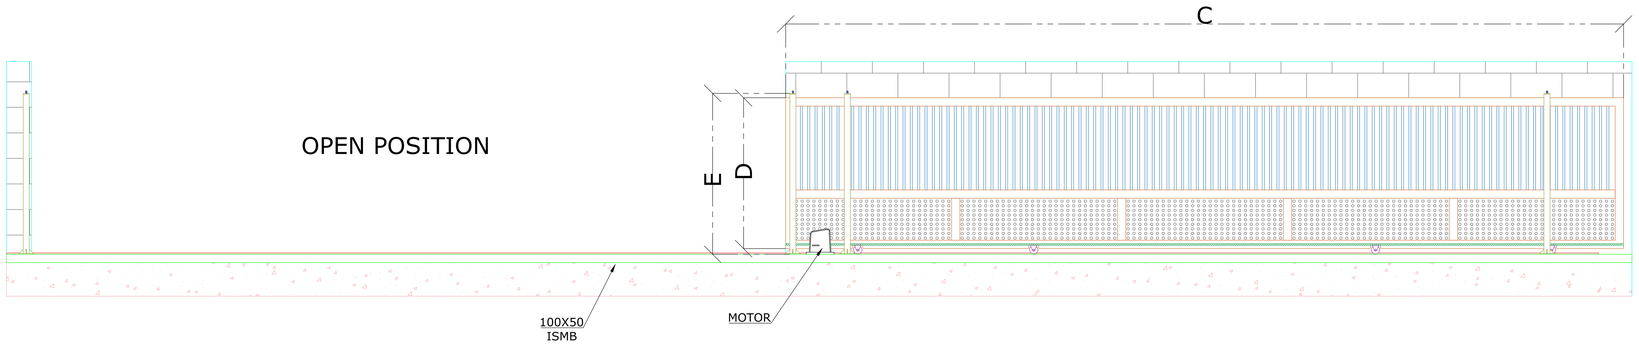


1. MOTORIZED SINGLE LEAF SLIDING GATE

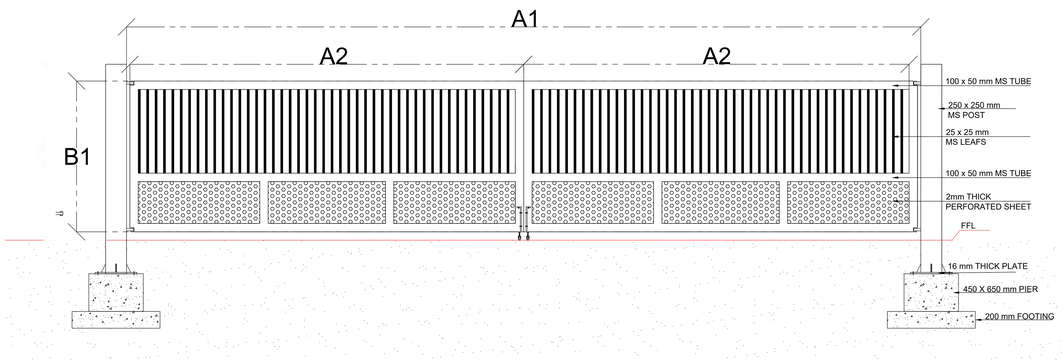

2. MANUAL DOUBLE LEAF SWING GATE

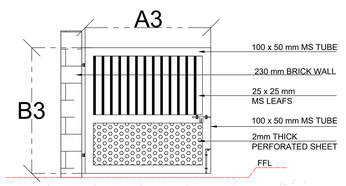

3. WICKET GATE

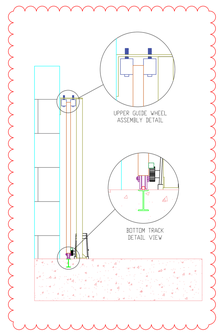

SIDE VIEW

NOTE:-
1. All dimension are in MM
2. This drawing is solely meant to be understood.

DIMENSION :-

1	A	9000 mm	CLEAR WIDTH
2	B	11000 mm	GATE PARKING AREA
3	C	10000 mm	SLIDING LEAF WIDTH
4	D	1800 mm	SLIDING LEAF HEIGHT
5	E	1920 mm	GUIDE POST HEIGHT
6	A1	9000 mm	CLEAR WIDTH
7	A2	4500 mm	SWING LEAF WIDTH
8	B1	1800 mm	SWING LEAF HEIGHT
9	A3	1500 mm	CLEAR WIDTH
10	B3	1500 mm	LEAF HEIGHT

TECHNICAL DATA :

SR.NO	COLOR CODE	MATERIALS	SPECIFICATIONS
1			WALL
2		MS	OUTER FRAME MS TUBE
3		MS	INNER MS TUBE
4		MS	PERFORATED SHEET
5		MS	GUIDE POST
6		STD	BOTTOM WHEEL
7		NYLON & CCS (100Cr6)	UPPER GUIDE ROLLER
8		STD	MOTOR
9		En8	En8 BAR
10		MS	ISMB
11			CIVIL WORK (CONCRETE)

ACCESSORIES :-

IMPORTANT NOTES:-

NIHVA TECHNOLOGIES PVT. LTD.
NIHVA TECHNOLOGIES PVT. LTD. PUNE
Email:- info@nihva.com
Website:- www.nihva.com

TITLE:-

1. MOTORIZED SINGLE LEAF SLIDING GATE
2. MANUAL DOUBLE LEAF SWING GATE
3. WICKET GATE

CLIENT'S APPROVAL :

CLIENT - REWARDS CON.

PROJECT - GATE

SITE LOCATION -

DWG. NO. : NIHVA/24-25/XX00

SCALE: NTS	WT:	SHEET:1 OF 1	REV- 0

	NAME	DATE	SIGN
DRAWN	V.T.	09-10-2024	
DRAWN	S.J.	09-10-2024	
CHECK	S.W.	10-10-2024	
APPROVAL	V.T.	10-10-2024	

If any queries contact : design1@nihva.com

NOTE: ALL DIMENSIONS ARE IN mm

THIS DRAWING & DESIGNING IS THE PROPERTY OF NIHVA TECHNOLOGIES. NOT TO BE SOLD OR COPIED TO ANY OTHER CONCERN.