

OUTRIGGER ASSLY

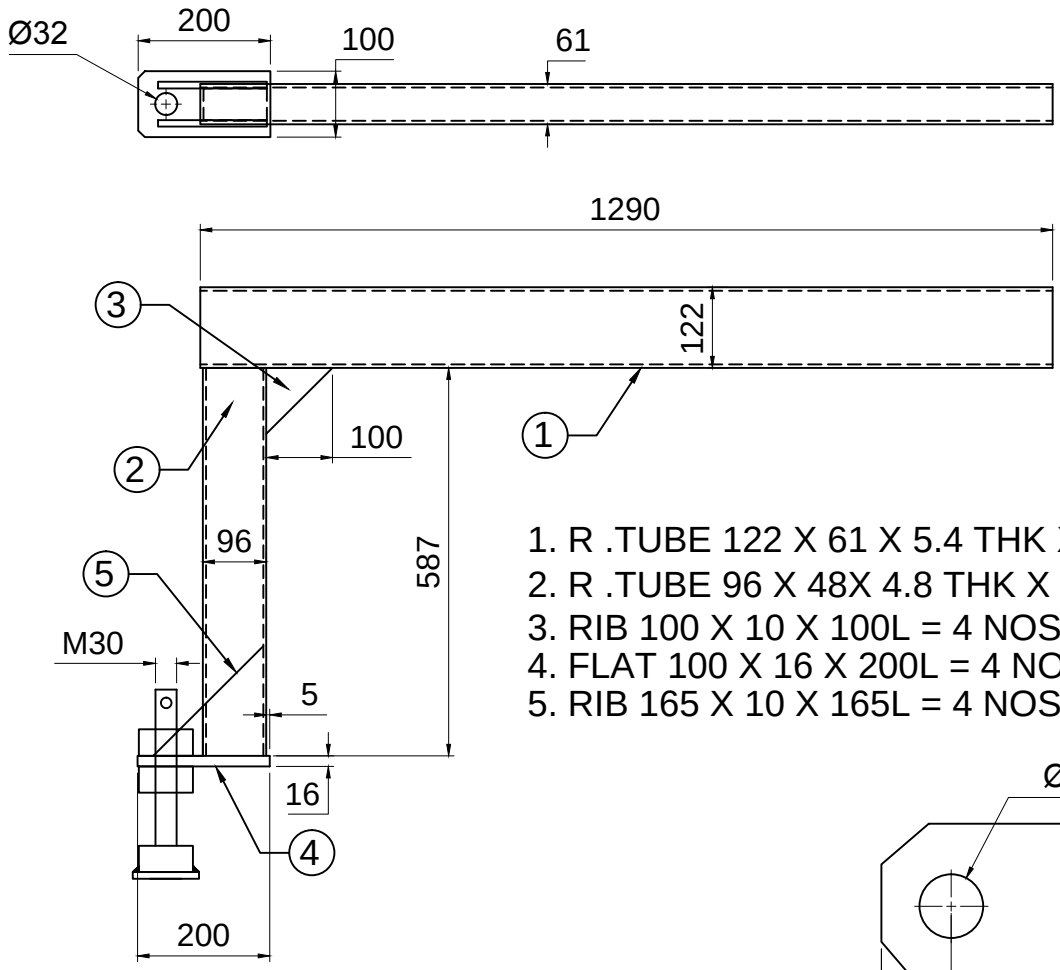

1. R .TUBE 122 X 61 X 5.4 THK X 1290L = 4 NOS
2. R .TUBE 96 X 48X 4.8 THK X 585L = 4 NOS
3. RIB 100 X 10 X 100L = 4 NOS
4. FLAT 100 X 16 X 200L = 4 NOS
5. RIB 165 X 10 X 165L = 4 NOS

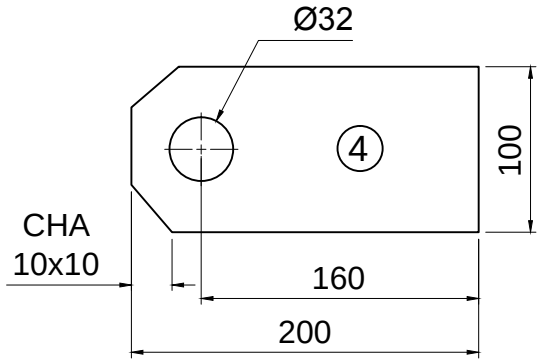

This drawing & design is the property of NIHVA TECHNOLOGIES. Not to be sold or copied to any other concern.

TITLE : - OUTRIGGER			NIHVA TECHNOLOGIES PVT. LTD. PUNE Tel : 020 66304033 Email:- info@nihva.com Website:- www.nihva.com
	SIGN	DATE	
DRAWN	P.A	04.10.2018	CLIENT -
CHECK	R.D	04.10.2018	PROJECT -
REV.			SITE -
APPROVAL			DWG. NO. : NIHVA/18-19/MFG/NSL/1018/015
If any queries contact : projects@nihva.com			SCALE: NTS | WT: | SHEET: 01 OF 01
ALL DIMENSION ARE IN mm			