
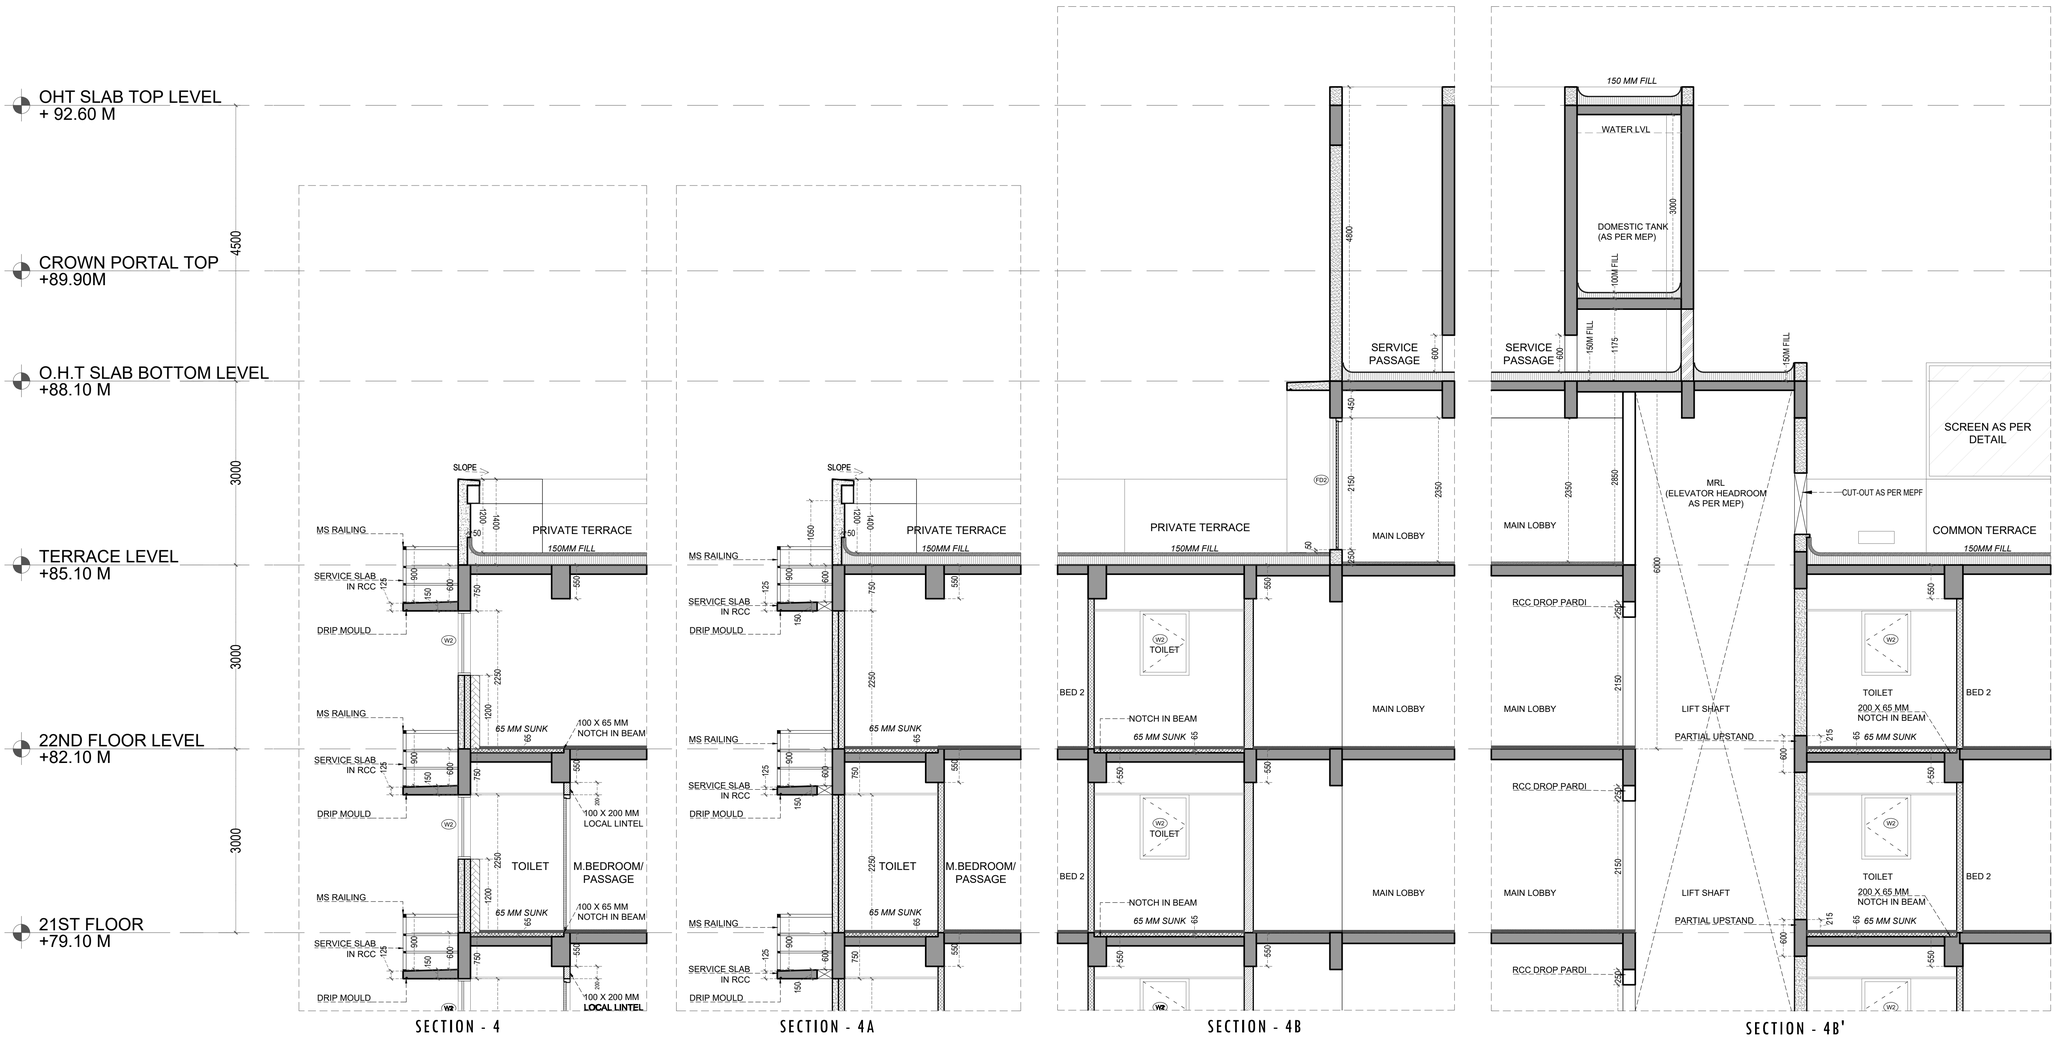


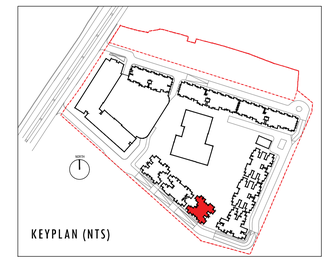

DOOR SCHEDULE (FOR TERRACE FLOOR)

NO.	LOCATION	WIDTH (CIVIL OPENING)	LINTEL (FRM SFL)	CILL (FRM SFL)	DESCRIPTION
FD1	STAIRCASE	1200	2400	-	SINGLE LEAF FIRE RATED WOODEN FLUSH DOOR (DETAIL AS PER VENDOR)
FD2	LOBBY	1100X2150 (WXH)	2400	250	SINGLE LEAF FIRE RATED METAL DOOR (DETAIL AS PER VENDOR)
FD3	IBMS ROOM	1200X2050 (WXH)	2400	350	SINGLE LEAF FIRE RATED METAL DOOR (DETAIL AS PER VENDOR)
DD1	F.H.C/ ELE SHAFTS	1200X1975 (W X H)	2400	425 (UPSTAND BEAM)	DOUBLE LEAF FIRE RATED METAL DOOR (DETAIL AS PER VENDOR)
DD1A	ELV SHAFT	1100X1975 (W X H)	2400	425 (UPSTAND BEAM)	DOUBLE LEAF FIRE RATED METAL DOOR (DETAIL AS PER VENDOR)
DD3	PLB SHAFT	600 X1975 (W X H)	2400	425 (UPSTAND BEAM)	SINGLE LEAF FIRE RATED METAL DOOR (DETAIL AS PER VENDOR)
DD2	STAIRCASE ELE SHAFT	1200 X1975 (W X H)	2400	425 (UPSTAND BEAM)	DOUBLE LEAF FIRE RATED METAL DOOR (DETAIL AS PER VENDOR)

WINDOW SCHEDULE

NO.	LOCATION	CIVIL OPENING (W X H)	LINTEL (FRM SFL)	CILL (FRM SFL)	DESCRIPTION
LW1B	LOBBY WINDOW	1000 X 1200	2400	1200	SINGLE LEAF OPENABLE GLASS PANEL WINDOW WITH FRICTION HINGE
LW5	STAIRCASE WINDOW	850 X1200	2450 (FROM ML)	1250 (FROM ML)	SINGLE LEAF OPENABLE GLASS PANEL WINDOW WITH FRICTION HINGE

FINS SCHEDULE

NO.	LOCATION	CIVIL OPENING (W X H)	DESCRIPTION
F1	UTILITY	2400X2275	FINS AS PER DETAIL
F2	STAIRCASE TOILET SHAFT	1590X2985	FINS AS PER DETAIL
F3	SERVICE AREAS	2265X2985	FINS AS PER DETAIL
F4	TERRACE SERVICE CHOWKS	910X800	FINS AS PER DETAIL
F5	PERGOLA	2600X3253	FINS AS PER DETAIL
F6	IBMS TERRACE	1000X2200	FINS AS PER DETAIL
F6A	IBMS TERRACE	475X2200	FINS AS PER DETAIL
F7	SERVICE CORRIDOR	600X1000	FINS AS PER DETAIL

GENERAL NOTES

1 : All dimensions are in millimeters and levels in meters unless specified otherwise.
2 : Do not scale the drawing; follow written dimensions.
3 : All dimensions are unfinished dimensions unless specified otherwise.
4 : Any discrepancies should be brought to the notice of the Architect prior to execution of job / procuring materials at site.
5 : This drawing is the property of Kapadia Associates and should not be reproduced, copied, handed over to a third party or used for any purpose other than for which it has been issued.
6 : This drawing is to be read in conjunction with all relevant structural & services drawings.

NOTE:

1. PLEASE READ IN CONJUNCTION WITH KITCHEN DETAIL,TOILET DETAIL, FIN DETAIL & RAILING DETAIL, STARICASE DETAILS.
2. 10MM ADDITIONAL COVER HAS BEEN INCLUDED IN THE SHEAR WALL THICKNESS, WHEREVER REQUIRED FOR GROOVE.

REVISION INDEX

REV. NO.	DATE	REMARKS
R00	30-06-2026	VFC ISSUED

CLIENT

LODHA GROUP

PROJECT TITLE

LODHA RISERVO - A4

VIKHROLI,MUMBAI

DRAWING TITLE & NO.

AR-KA-A4-401.3_TERRACE WALL SECTIONS

DRAWING STAGE

WORKING DRAWING

SCALE	REV. NO.	REV. DATE
1:50	R00	30-06-2026

STAMP & SIGNATURE

Jagadishponraj Nadar
Digitally signed by: Jagadishponraj Nadar
DN: CN = Jagadishponraj Nadar
OU = Lodha Users
Date: 2026.07.01 16:13:24 +06'30'

Vaibhav Shimpi
Digitally signed by: Vaibhav Shimpi
DN: CN = Vaibhav Shimpi
OU = Lodha Users
Date: 2026.07.01 16:42:39 +06'30'

Digitally signed by: SUPRIYA UKIDAVE
Date: 2026.07.01 12:00:07 +06'30'

KAPADIA ASSOCIATES
architecture • urban design
112-114, Peninsula Centre,Dr. S.S. Rao Road,Parel East, Mumbai 400012
Tel : 91-22-6660 2838 / 39 E-mail : kapl@kapl.in Website : www.kapl.in