

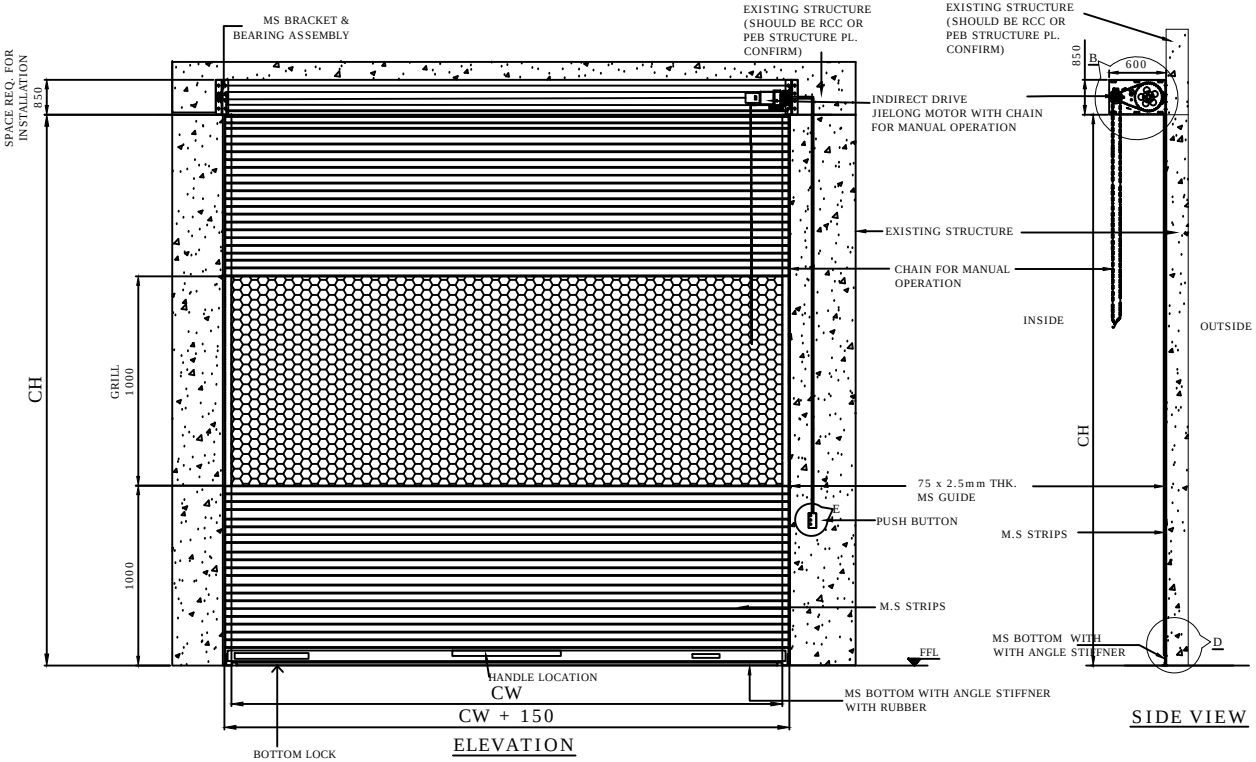


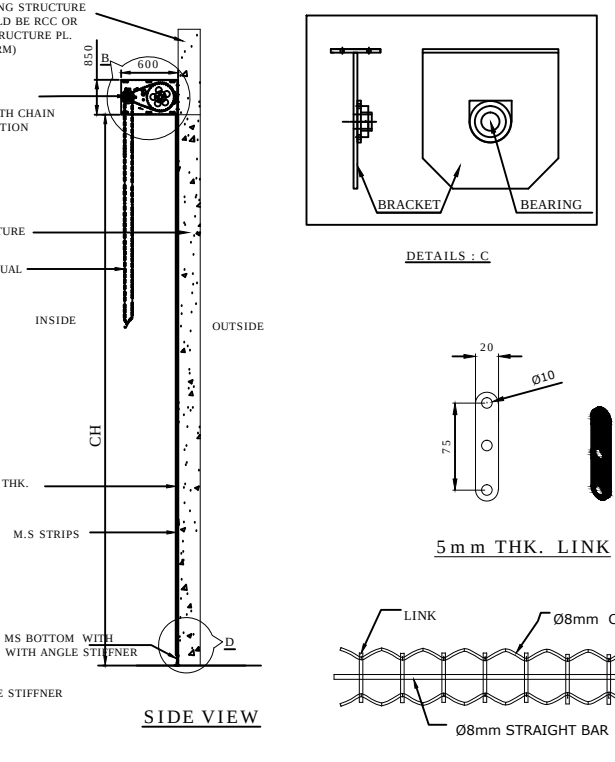



DETAILS : C

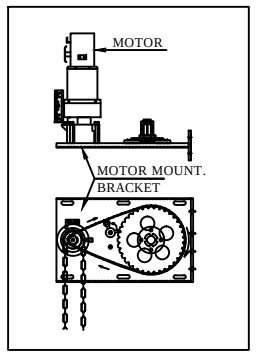


DETAILS : A & B


5mm THK. LINK

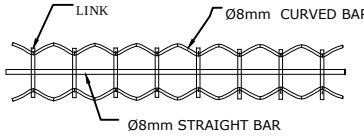


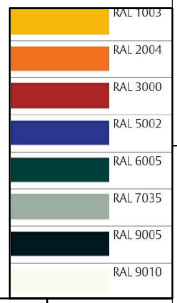

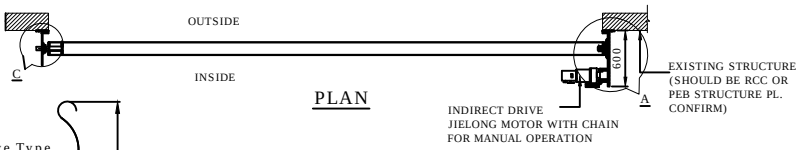

PLAN

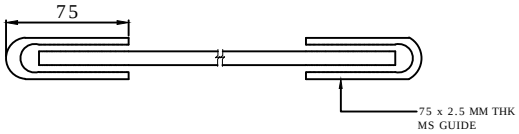

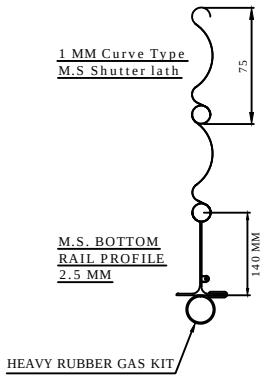

DETAILS : D

R01	06.01.19	P.A	1. SIZES & QTY CHANGE.
REV NO	DATE	DRAWN	REMARK

(NOTE: REQUIRED TECHANICAL STRUCTURE FOR SHUTTER IN CLIENT SCOPE)

CLEAR WIDTH (CW)	CLEAR HEIGHT (CH)	QUANTITY
3000	3500	1
3850	3600	1
3000	3600	7
2000	3000	2
4000	3660	2

This drawing & design is the property of NIHVA TECHNOLOGIES. Not to be sold or copied to any other concern.

TITLE: MOTORIZED ROLLING SHUTTER

	NAME	SIGN	DATE
DRAWN	P.A		24.12.2019
CHECK	G.J		24.12.2019
APPRD.			

NIHVA TECHNOLOGIES PVT. LTD.
NIHVA TECHNOLOGIES PVT. LTD. PUNE
Tel : 020 66304033
Email:- info@nihva.com
Website:- www.nihva.com

CLIENT - DESAI CONSTRUCTION
PROJECT - GE LOCOMOTIVE
SITE LOCATION - GUJARAT
If any queries contact : design@nihva.com
DWG. NO. : NIHVA/19-20/0184/R01
REV- R01
ALL DIMENSION ARE IN mm
SCALE: NTS
WT:
SHEET: