




SECTION A - A
1:30

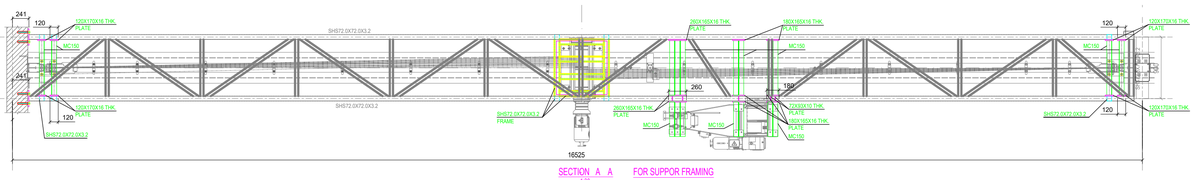


SECTION A A FOR SUPPOR FRAMING
1:30

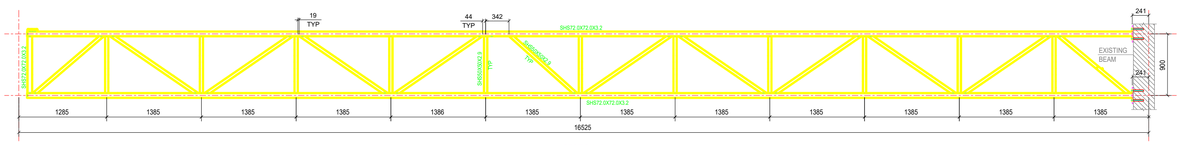


SECTION B - B
1:30

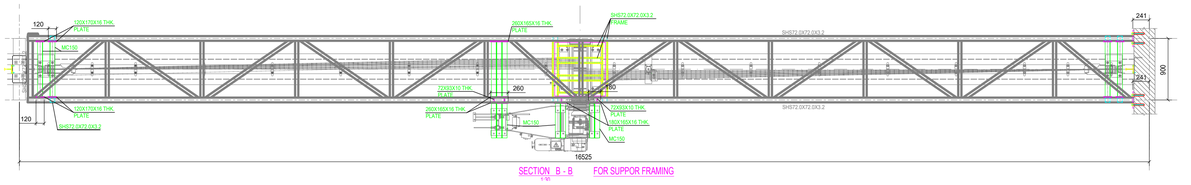


SECTION B - B FOR SUPPOR FRAMING
1:30

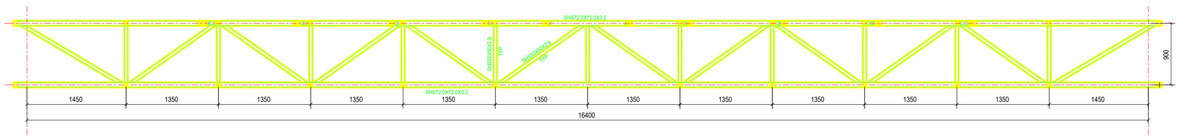


SECTION E - E
1:30

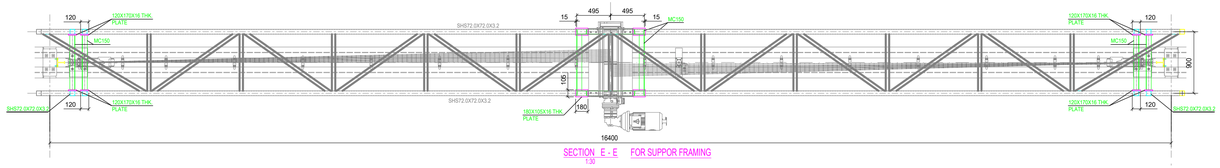

SECTION E - E FOR SUPPOR FRAMING
1:30

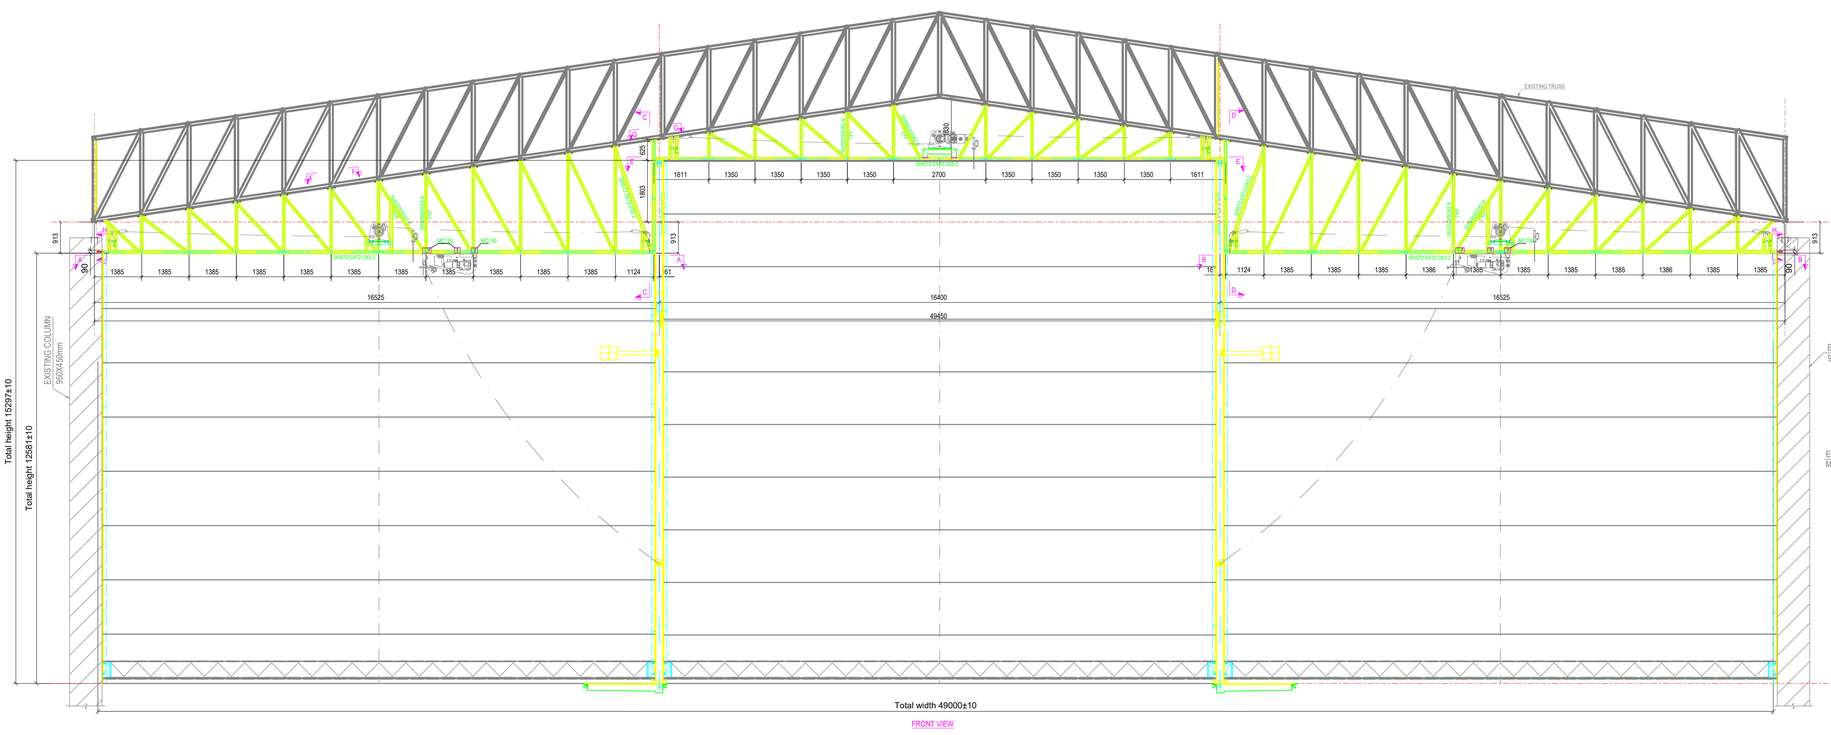


FRONT VIEW

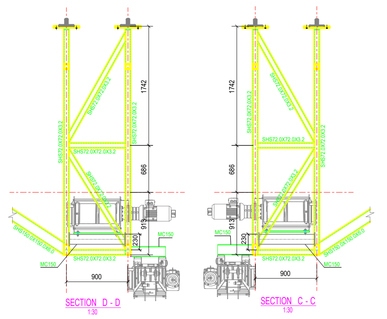


SECTION D - D
1:30

SECTION C - C
1:30

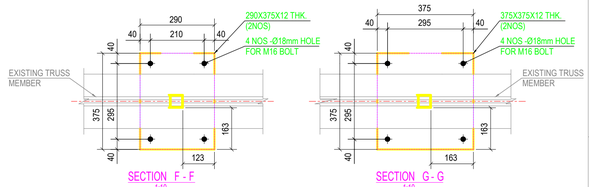


SECTION F - F
1:10

SECTION G - G
1:10

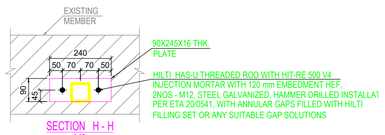

SECTION H - H
1:10

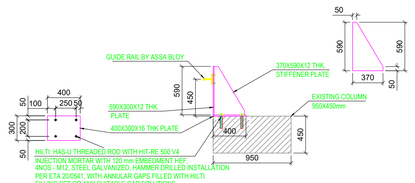

TYP GUIDE RAIL CONNECTION PLATE DETAIL

Rev No.	Revision	Date	Revised By
000	INITIAL DRAWING FOR APPROVAL	11/07/2022	KL

This drawing & design is the property of NIHVA TECHNOLOGIES. Not to be sold or copied to any other concern.

TITLE:-- STRUCTURE AND MEGA DOOR

NIHVA TECHNOLOGIES PVT. LTD.
NIHVA TECHNOLOGIES PVT. LTD, PUNE
Tel : 020 66304033
Email:- info@nihva.com
Website:- www.nihva.com

	NAME	DATE	SIGN
DRAWN	KISHAN	11/07/2022	
CHECK	M.SUTAR	11/07/2022	
APPRD.	HARSHAL	11/07/2022	

CLIENT- COCHIN INTERNATIONAL AIRPORT
LOCATION - COCHIN,
PRODUCT - MEGA DOOR
If any queries contact : design@nihva.com
DWG NO:-NIHVA/22-23/CLT/0075
REV- 01
ALL DIMENSION ARE IN mm
SCALE: NTS
SCALE:-- 1:1
SHEET: 01 OF 01