


-

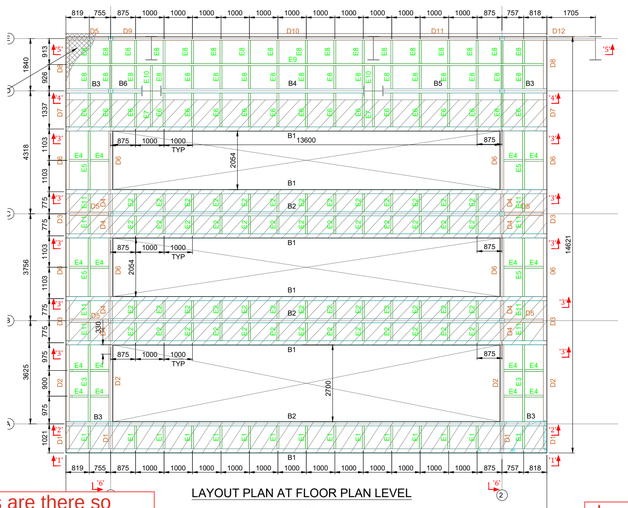

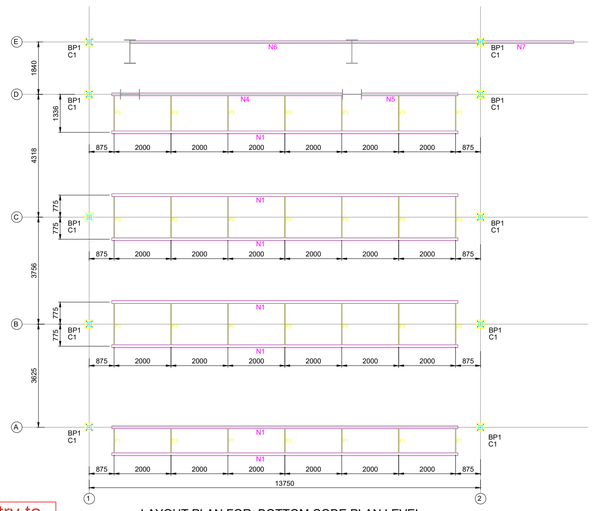


hear bracings are there so please this area


please try to remove this poles if required the take cantilever support to improve the work area and moment

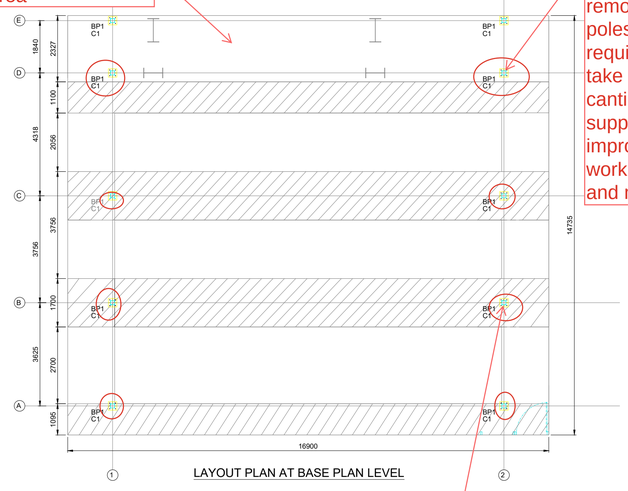



move this poles to the wall area and give us the design this items are fouling to our platform

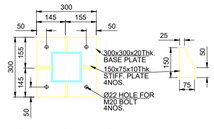



DETAIL FOR BASE PLATE FOR 150X150X6THK.

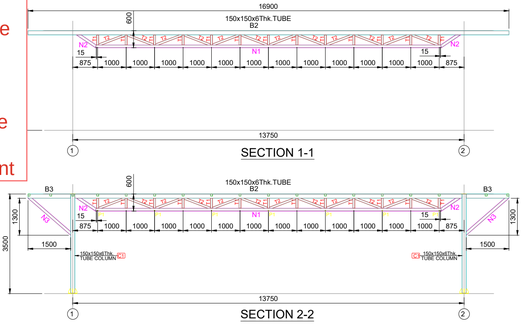

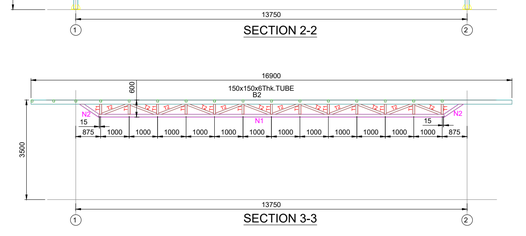

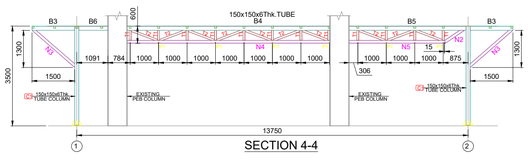

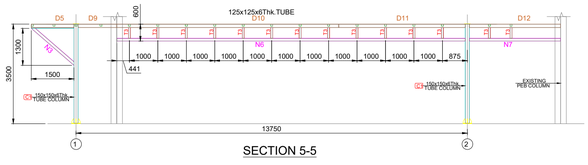

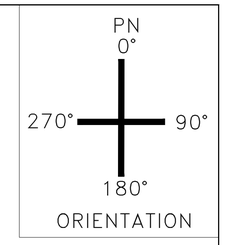

MTO							
ITEM No.	DESCRIPTION	WD. mm	LG. mm	UNIT WT. (kg/m)	QTY.	WEIGHT IN kg. UNIT	TOTAL
BP1	20 thk pl.	300	300.00	157.00	10	14.13	141.30
C1	150x150x6Thk.		3480.00	26.40	10	91.87	918.72
B1	150x150x6Thk.		16900.00	26.40	5	446.16	2230.80
B2	150x150x6Thk.		13600.00	26.40	3	359.04	1077.12
B3	150x150x6Thk.		1500.00	26.40	4	39.60	158.40
B4	150x150x6Thk.		7122.00	26.40	1	188.02	188.02
B5	150x150x6Thk.		4106.00	26.40	1	108.40	108.40
B6	150x150x6Thk.		1016.00	26.40	1	26.82	26.82
D1	125x125x6Thk.		796.00	21.69	4	17.27	69.06
D2	125x125x6Thk.		2700.00	21.69	4	58.56	234.25
D3	125x125x6Thk.		1400.00	21.69	4	30.37	121.46
D4	125x125x6Thk.		625.00	21.69	8	13.56	108.45
D5	125x125x6Thk.		1375.00	21.69	5	29.82	149.12
D6	125x125x6Thk.		2056.00	21.69	8	44.59	356.76
D7	125x125x6Thk.		1187.00	21.69	2	25.75	51.49
D8	125x125x6Thk.		1702.00	21.69	2	36.92	73.83
D9	125x125x6Thk.		1351.00	21.69	1	29.30	29.30
D10	125x125x6Thk.		7792.00	21.69	1	169.01	169.01
D11	125x125x6Thk.		1141.00	21.69	1	24.75	24.75
D12	125x125x6Thk.		3201.00	21.69	1	69.43	69.43
E1	75X75X6Thk.		795.00	12.27	15	9.75	146.32
E2	75X75X6Thk.		625.00	12.27	52	7.67	398.78
E3	75X75X6Thk.		2700.00	12.27	2	33.13	66.26
E4	75X75X6Thk.		656.00	12.27	16	8.05	128.79
E5	75X75X6Thk.		2056.00	12.27	4	25.23	100.91
E6	75X75X6Thk.		1187.00	12.27	17	14.56	247.60
E7	75X75X6Thk.		1258.00	12.27	2	15.44	30.87
E8	75X75X6Thk.		814.00	12.27	34	9.99	339.58
E9	75X75X6Thk.		16650.00	12.27	1	204.30	204.30
E10	75X75X6Thk.		885.00	12.27	2	10.86	21.72
E11	75X75X6Thk.		367.00	12.27	8	4.50	36.02
N1	100X100X6Thk.		12163.00	16.98	7	206.53	1445.69
N2	100X100X6Thk.		806.00	16.98	15	13.69	205.29
N3	100X100X6Thk.		1985.00	16.98	9	33.71	303.35
N4	100X100X6Thk.		7122.00	16.98	1	120.93	120.93
N5	100X100X6Thk.		3388.00	16.98	1	57.53	57.53
N6	100X100X6Thk.		12241.00	16.98	1	207.85	207.85
N7	100X100X6Thk.		3201.00	16.98	1	54.35	54.35
N8	100X100X6Thk.		1305.00	16.98	8	22.16	177.27
N9	100X100X6Thk.		1413.00	16.98	2	23.99	47.99
N10	100X100X6Thk.		1700.00	16.98	2	28.87	57.73
T1	72X72X3.2Thk.		350.00	6.71	104	2.35	244.24
T2	72X72X3.2Thk.		969.00	6.71	94	6.50	611.19
T3	72X72X3.2Thk.		375.00	6.71	14	2.52	35.23
P1	32X32X3.2Thk.		795.00	2.69	7	2.14	14.97
P2	32X32X3.2Thk.		1400.00	2.69	14	3.77	52.72
P3	32X32X3.2Thk.		1187.00	2.69	7	3.19	22.35
						TOTAL	11686.32

10 mm THK. PLATE	156.37 SQ.M

STEEL NOTES:-

1. ALL DIMENSIONS ARE IN MILLIMETRES & LEVELS ARE IN METRES.
2. ALL STRUCTURAL STEEL AS PER IS:2062.
3. PROVIDE WELDING AS PER IS:816.
4. PROVIDE MIN. 6MM WELD.
5. USE ELECTRODS AS PER IS:814 (PT.-I).
6. FILLET/ BUTT WELD SHALL BE OF 6MM SIZE AND SHALL BE CONTINUOUS.
7. FABRICATION AND ERECTION SHALL BE AS PER IS:800 AND IS:803.
8. WELD SHALL BE GROUND SMOOTH.
9. ALL GUSSET PLATES SHALL BE MIN. 8 THK.
10. ALL M.S. BLACK BOLTS AND NUTS SHALL CONFORM TO IS:1363(PT. 1 TO 3).
11. ALL STRUCTURE WILL BE PROVIDED WITH MIN. ONE COAT OF EPOXY PRIMER AND ONE COATS OF PU PAINT.
12. ALL CONNECTIONS SHALL BE FULLY WELDED AFTER BOLTING.

REV.NO.	DESCRIPTION.	REV.DATE	DRAWN.	CHKD.	APPD.
0	RELEASE FOR APPROVAL.	20.07.26			

DWG.TITLE :- NEOTRAFO - FABRICATION FOR COLLAPS ROOF

PROJECT	NEOTRAFO MANUFACTURING PLANT HYDERABAD, INDIA.
CLIENT	NEOTRAFO SOLTIONS PVT. LTD.
CONTRACTOR	-
NIHVA Technologies Pvt. Ltd.	NIHVA TEHNOLOGIES PVT.LTD.PUNE

DRAWN : MHS	CHECKED :HAB	SCALE: NTS
APPROVED : H.A.B.	JOB CODE. : ----	DATE: 15.01.26
DWG.NO: SALT-0000-STR-0001	(SH-1OF1)	REV. - R0 SIZE. - A3