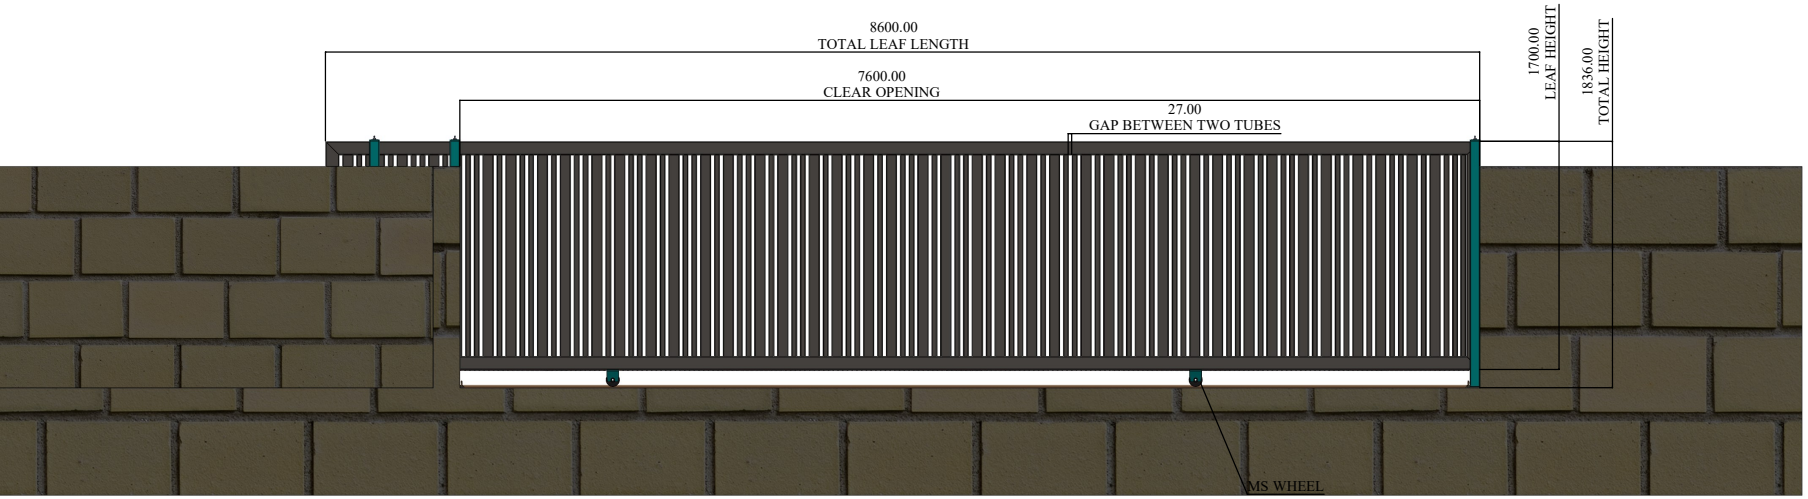
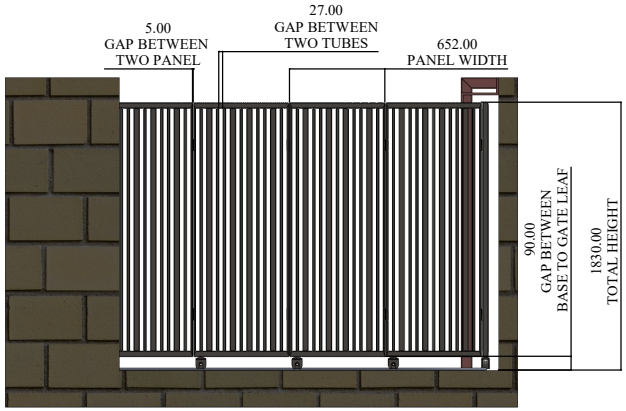

8600.00
TOTAL LEAF LENGTH
7600.00
CLEAR OPENING
27.00
GAP BETWEEN TWO TUBES
1700.00
LEAF HEIGHT
1836.00
TOTAL HEIGHT
MS WHEEL


5.00
GAP BETWEEN
TWO PANEL
27.00
GAP BETWEEN
TWO TUBES
652.00
PANEL WIDTH
90.00
GAP BETWEEN
BASE TO GATE LEAF
1830.00
TOTAL HEIGHT