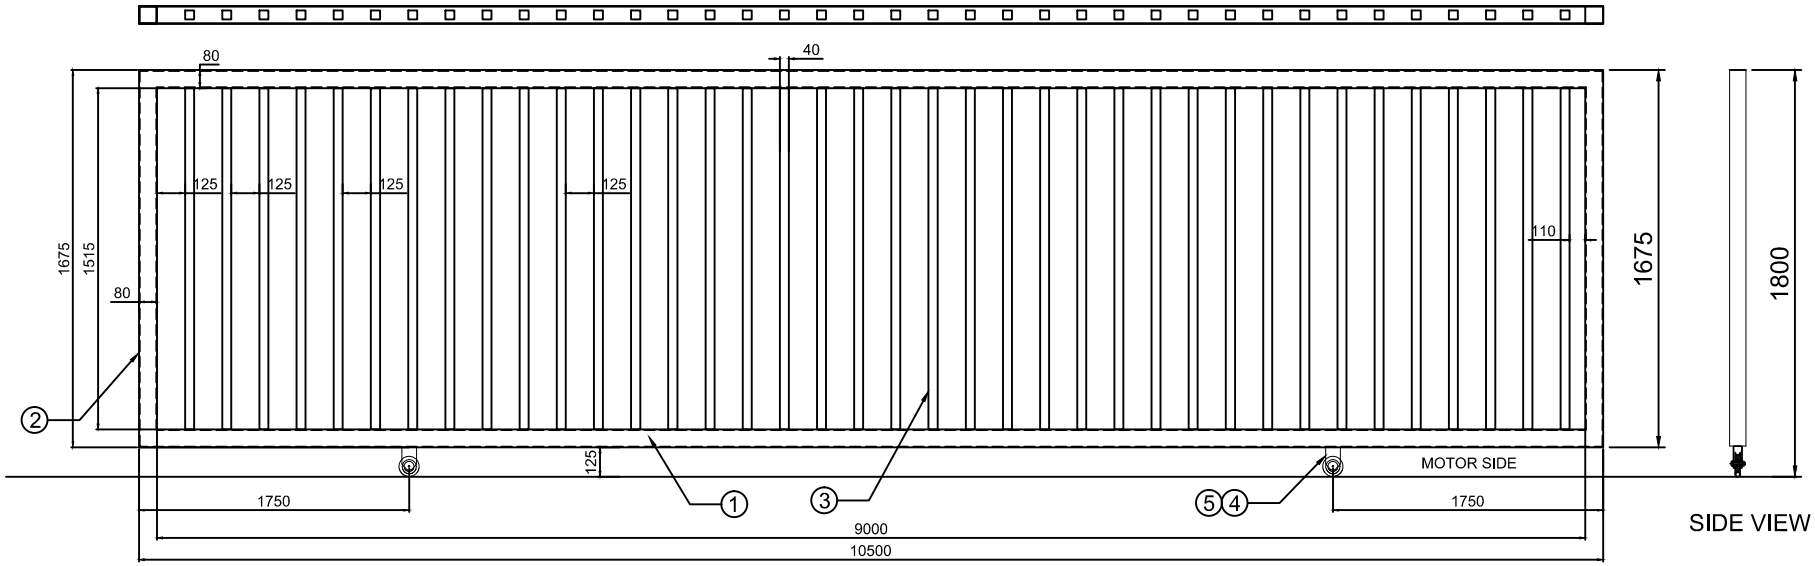


SR.NO	DESCRIPTION	SPECIFICATION	QTY	WEIGHT
5	WHEEL	4 " STEEL WHEEL	2 NOS	
4	WHEEL BKT	STANDARD FOR 4 " WHEEL	2 NOS	
3	SQ. TUBE	40 X 40 X 2 THK X 1515L	63 NOS	135 KGS
2	SQ. TUBE	80 X 80 X 3.2 THK X 1675L	2 NOS	27 KGS
1	SQ. TUBE	80 X 80 X 3.2 THK X 10500L	2 NOS	168 KGS

This drawing & designing is the property of NIHVA TECHNOLOGIES. Not to be sold or copied to any other concern.

TITLE: SLIDING GATE LEAF

NIHVA
NIHVA TECHNOLOGIES PVT. LTD.
NIHVA TECHNOLOGIES PVT. LTD. PUNE
Tel : 020 66304033
Website:- www.nihva.com
Email:- info@nihva.com

	Name	SIGN	DATE
DRAWN	P.V.A		31.05.19
CHECK	V.M.T		31.05.19
APPROVAL			

If any queries contact : design@nihva.com

ALL DIMENSION ARE IN mm

CLIENT -

PROJECT -

SITE LOCATION -

DWG. NO. : NIHVA/19-20/VDR/053 REV.- 0

SCALE: NTS WT: SHEET: 01 OF 01