

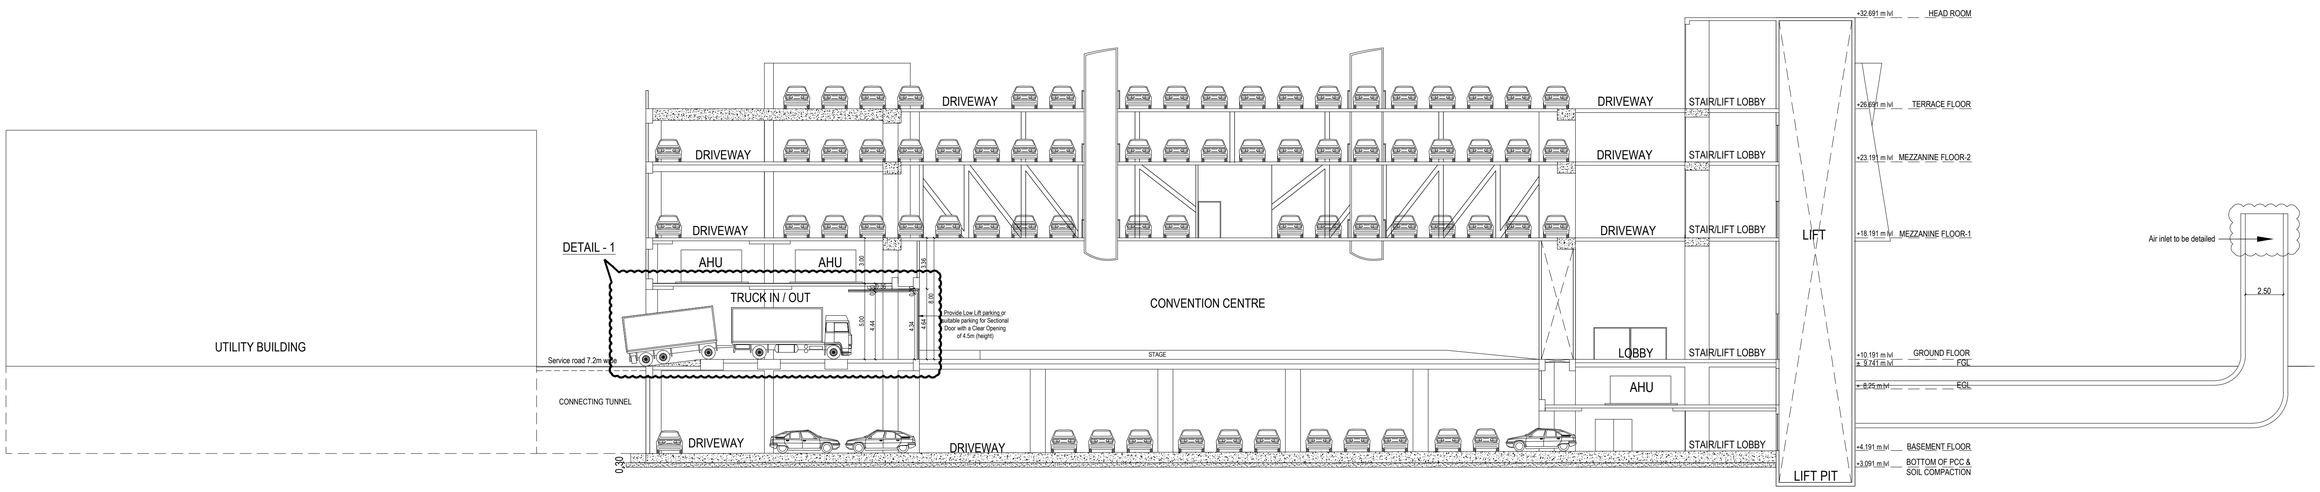



Reference Section- BB'

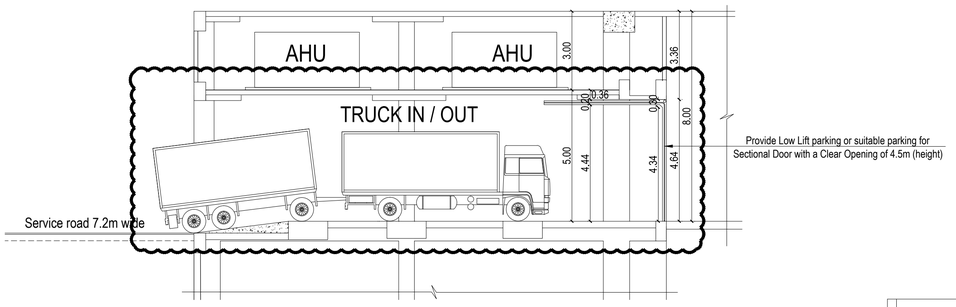

DETAIL - 1

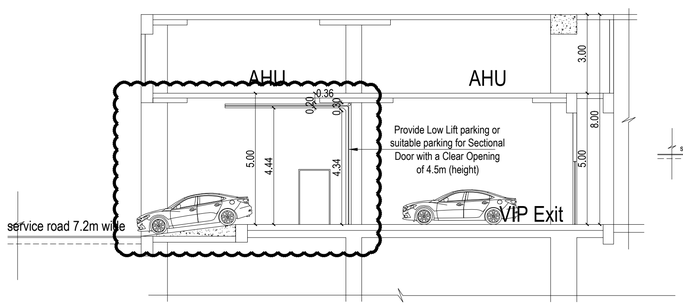

DETAIL - 2

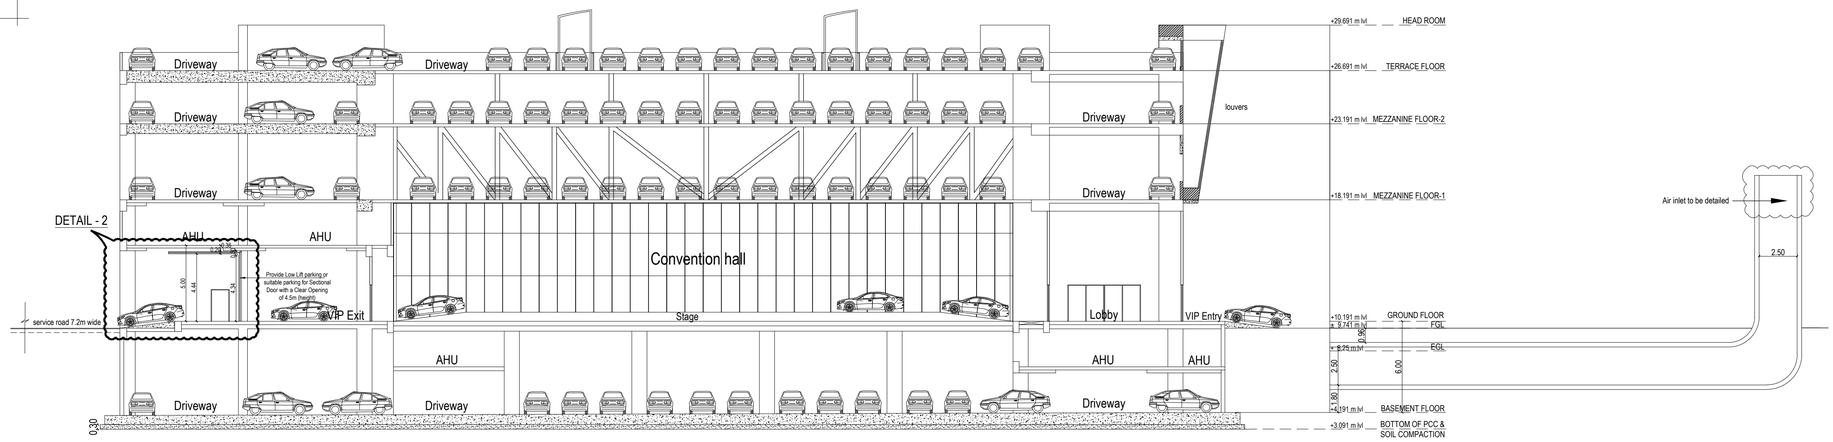

Reference Section- CC'

PROPOSED EXPANSION PROJECT OF CHENNAI TRADE CENTRE CAMPUS , NANDAMBAKKAM, CHENNAI.

Note:

P.S	—	Plumbing shaft
F.S	—	Fire shaft
E.S	—	Electrical shaft
T.S	—	Telecommunication shaft
PZ.S	—	Pressurization shaft

COPYRIGHT

THIS DRAWING IS A COPYRIGHT. IT IS NOT TO BE REPRODUCED, COPIED HANDED OVER TO A THIRD PARTY OR USED FOR ANY PURPOSE OTHER THAN FOR THE PROJECT INVOLED.WITHOUT THE KNOWLEDGE OF TAAMAESEK.

ARCHITECTS & ENGINEERS

Taamaesek Engineering Consortium
New no. 5, Old no.2a, Bishop Wallers Avenue west, Mylapore,
Chennai - 600 004. Ph : 044-24671157/1139. Fax : 044-24672237.
url:www.taamaesek.com
e-mail: info@taamaesek.com