

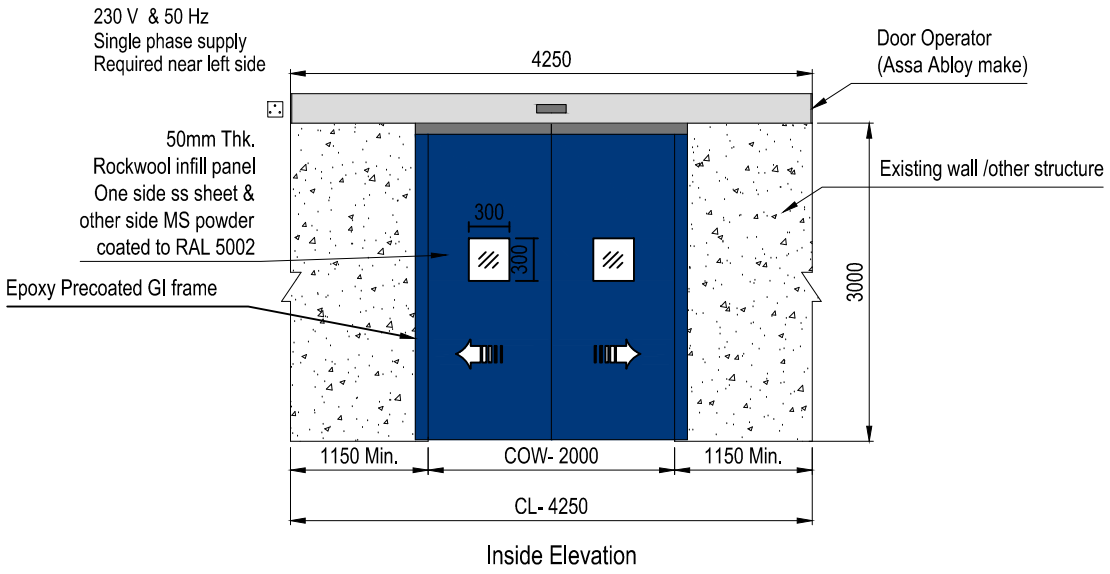


Inside Elevation

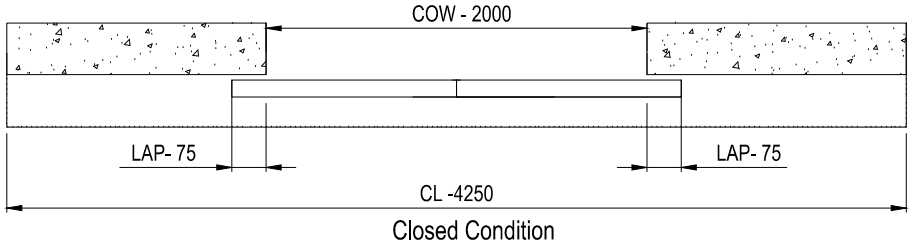


Closed Condition

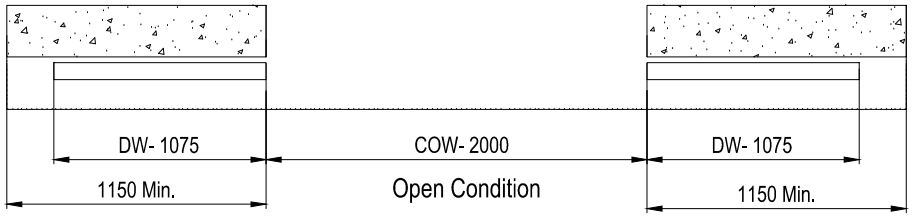

Open Condition

Plan

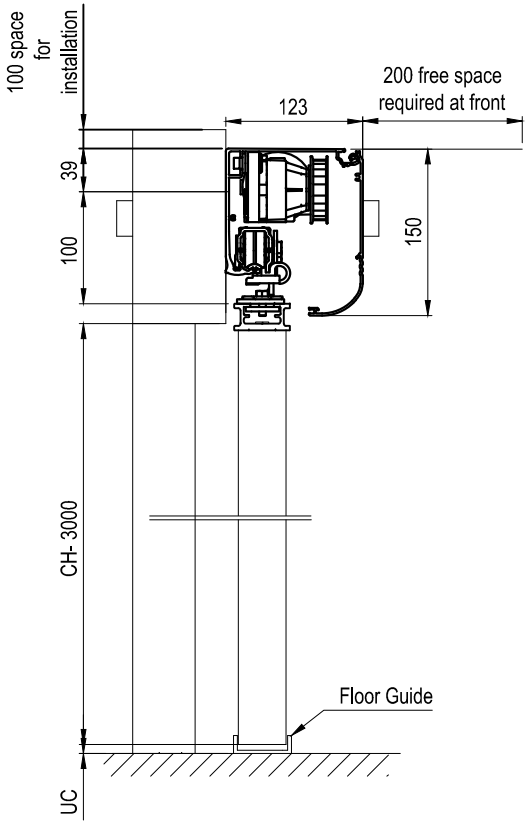

Door Size			
Sr. No.	Clear Width	Clear Height	Quantity
1	2000	3000	1

REV 1(31-03-2018)- Panel thickness revised from 60mm to 50mm.
Also panel will be of SS on one side & MS powder coated on other side.
REV 2(21-04-2018)- Vision window of size 300X300mm added to the panel. color of one side of panel will be RAL 5002 Ultramarine blue.

This drawing & designing is the property of NIHVA TECHNOLOGIES. Not to be sold or copied to any other concern.

TITLE	G.A.OF AUTOMATIC SLIDING DOOR		NIHVA TECHNOLOGIES PVT. LTD. PUNE Tel : 020 66304033 Email:- info@nihva.com Website:- www.nihva.com	
	SIGN	DATE		
DRAWN	OMKAR	10/03/18	CLIENT - MASTPRO	
CHECK	S.S.	10/03/18	PROJECT - MARS INTERNATIONALS	
REV.	00		SITE - PUNE	
APPROVAL	S.S.	10/03/18	DWG. NO. : NIHVA/17-18/0397/R02	REV-2
If any queries contact : design@nihva.com			SCALE: NTS	WT: SHEET: 01 OF 01
ALL DIMENSION ARE IN mm				