Weitergabe sowie Vervielfältigung dieses Dokuments, Verwertung und Mitteilung seines Inhalts sind nur nach vorheriger ausdrücklicher schriftlicher Zustimmung von SMS Meer GmbH gestattet. Das Dokument ist vor unberechtigtem Zugriff Dritter zu schützen. Zuwiderhandlungen verpflichten zu Schadensersatz. Alle Rechte aus Patent-/Gebrauchsmuster-/Markenschutz vorbehalten.

The reproduction, distribution and utilization of this document as well as the disclosure of its content to others without prior explicit written consent of SMS Meer GmbH is prohibited. Holder has to protect this document against unauthorized withdrawal of third parties. Offenders will be held liable for the payment of damages. All rights reserved in case of patent/utility model/trademark protection.

Schnitt (Section) S06-01 - S06-01

E
Zaun (Fence)
Höhe (height)
2.000 mm
Geländer
(Railing)
C1
Zaun (Fence)
Höhe (height)
1.800 mm
Geländer
(Railing)
B
Zaun (Fence)
Höhe (height)
2.000 mm
Geländer
(Railing)

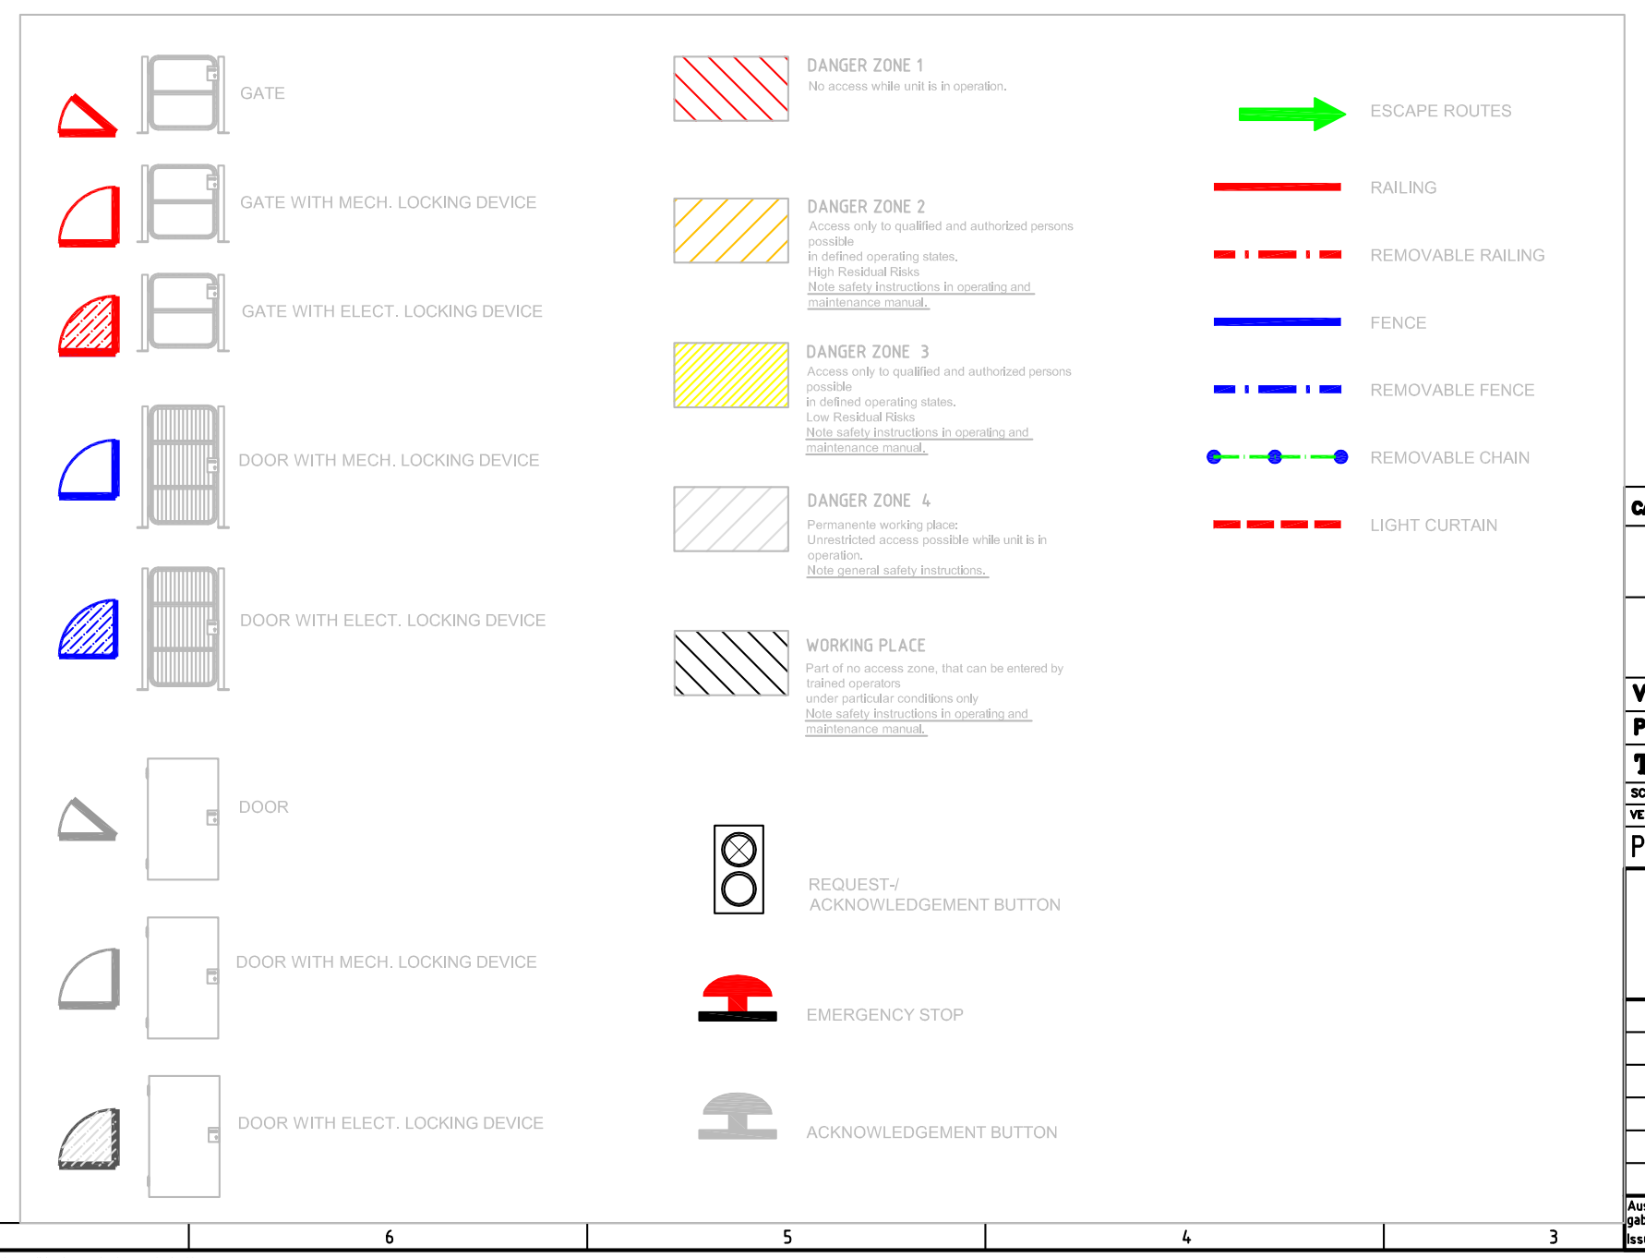
GATE
GATE WITH MECH. LOCKING DEVICE
GATE WITH ELECT. LOCKING DEVICE
DOOR WITH MECH. LOCKING DEVICE
DOOR WITH ELECT. LOCKING DEVICE
DOOR
DOOR WITH MECH. LOCKING DEVICE
DOOR WITH ELECT. LOCKING DEVICE
REQUEST-/
ACKNOWLEDGEMENT BUTTON
EMERGENCY STOP
ACKNOWLEDGEMENT BUTTON
ESCAPE ROUTES
RAILING
REMOVABLE RAILING
FENCE
REMOVABLE FENCE
REMOVABLE CHAIN
LIGHT CURTAIN

DANGER ZONE 1
No access while unit is in operation.

DANGER ZONE 2
Access only to qualified and authorized persons possible in defined operating states.
High Residual Risks
Note safety instructions in operating and maintenance manual.

DANGER ZONE 3
Access only to qualified and authorized persons possible in defined operating states.
Low Residual Risks
Note safety instructions in operating and maintenance manual.

DANGER ZONE 4
Permanente working place:
Unrestricted access possible while unit is in operation.
Note general safety instructions.

WORKING PLACE
Part of no access zone, that can be entered by trained operators under particular conditions only
Note safety instructions in operating and maintenance manual.

9463 0000 / RAILBHIL

CATEGORY OF DRWG.	APPROVAL	INFORMATION	REFERENCE	RECORD	CONSTRUCTION

SAIL

BHILAI STEEL PLANT, BHILAI, CHATTISGARH
7,0 MTPA EXPANSION

मेकॉन लिमिटेड
MECON LIMITED

VENSDOR'S NAME: SMS Meer/SMS Meer India/ABB
PACKAGE DESCRIPTION: UNIVERSAL RAIL MILL (Pkg No-047)
TITLE OF DRAWING. PARTITION 6, Safety Layout
SCALE-
VENDOR'S DRG NO.-
PROJECT DRG. NO. BSP-SMS Meer-08-047-21-130-35-BE-06654
REV.

Fertigungsvorschriften
Manufacturing Instructions
SN 200

Ursprung / Origin
Fertiggewicht
Finished weight
kg
Modell-Nr.
Pattern-No.
Werkstoff / Material
Projektionsmethode 1
First angle projection method
ISO 128

	Datum Date	Name
Bearb. Drawn	19.10.11	Prätzel
Geprüft Checked	19.10.11	Prätzel
Norm Stand		

Aus- gabe Issue	Änderung Revision	Datum Date	Name

Typ
Type
Safety Layout
Benennung
TEILBEREICH, 6
Title
PARTITION 6
Maßstab
Scale
1:50
Sach-Nr.
Drawing-No.
0100133-00.654
Blatt
Sheet
06
06
Blätter
Sheets

SMS
MEER
SMS group

Ersatz für:/Supersedes:
Ersetzt durch:/Superseded by:

Diese Zeichnung und alle darauf enthaltenen Informationen sind vertraulich. This drawing and all information on it is confidential.

A0