

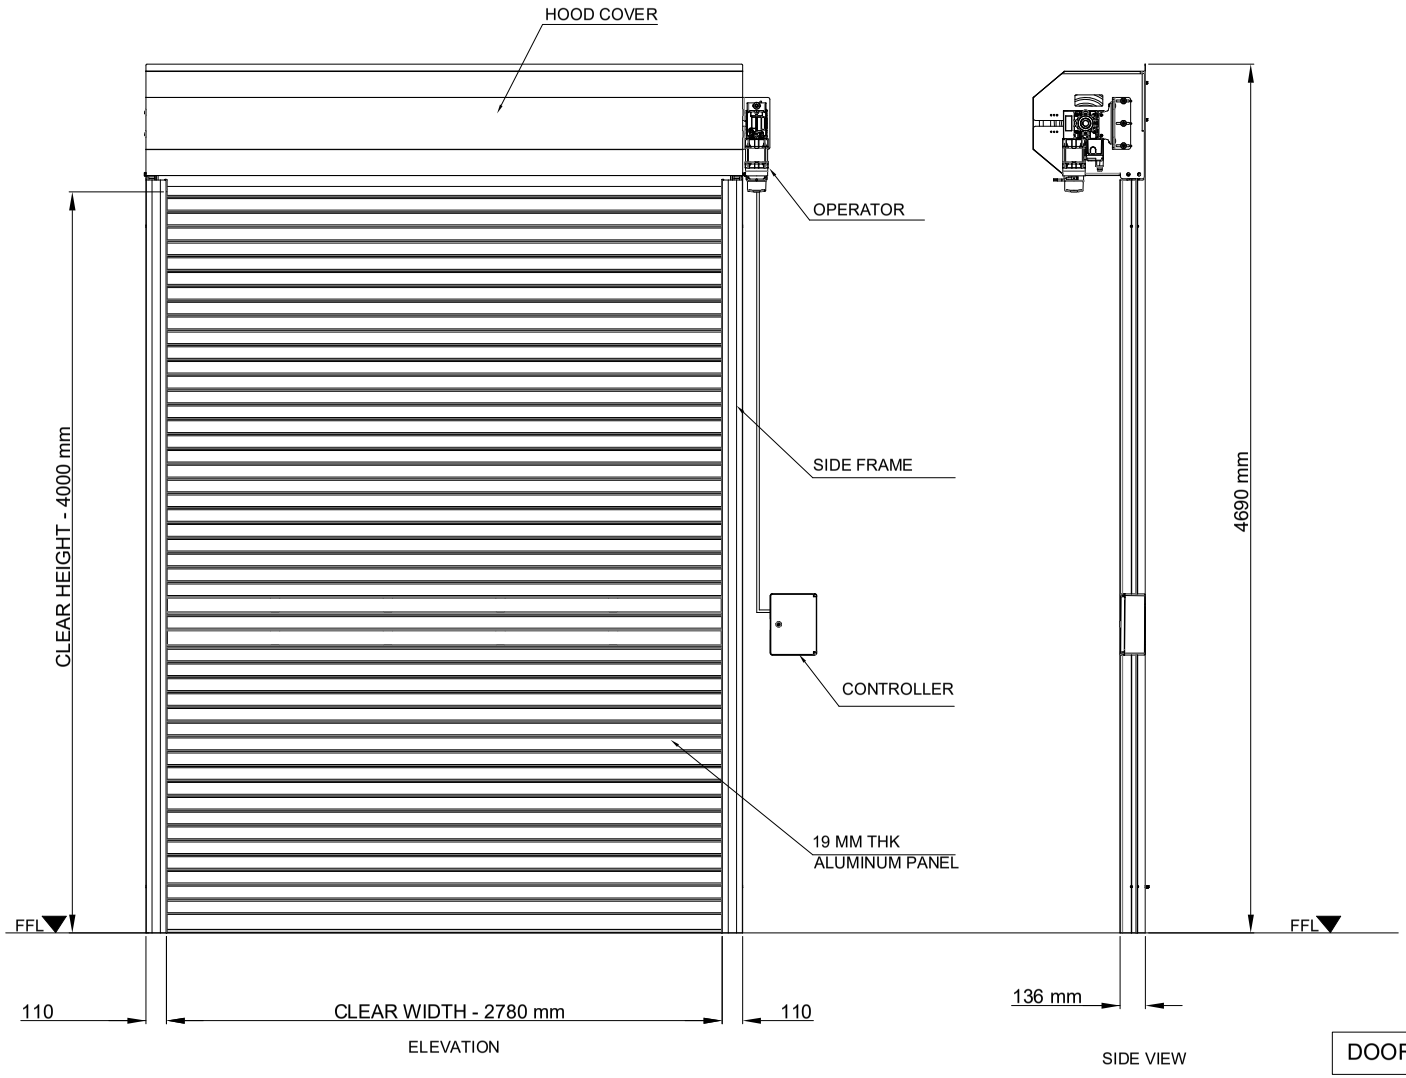


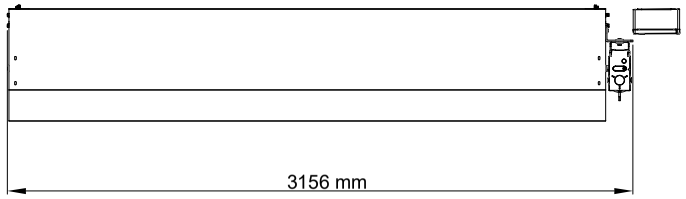

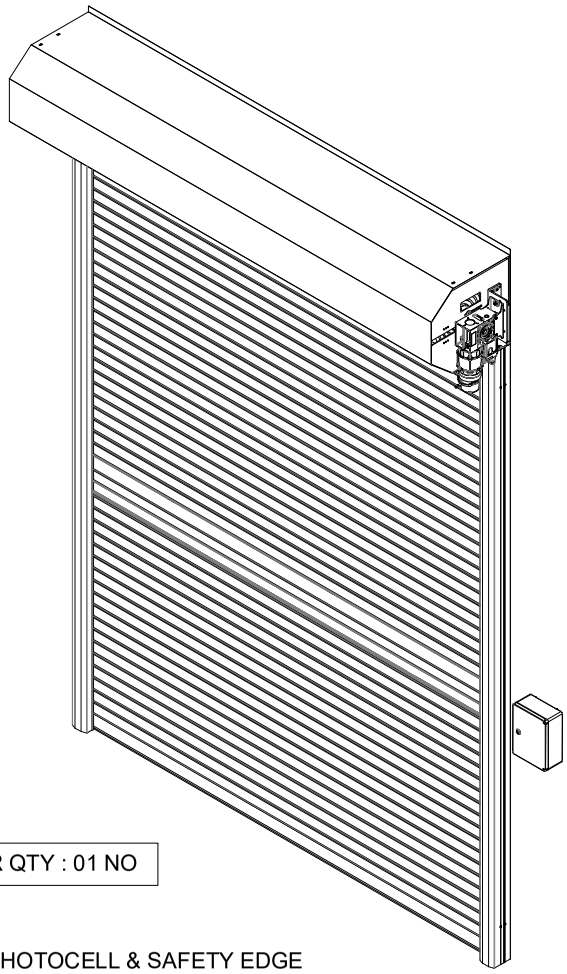

DOOR QTY : 01 NO

NOTES:
1. COLOR : RAL 9006
2. SAFETY DEVICE : PHOTOCELL & SAFETY EDGE
3. MANUAL ACTIVATION : CRANK HANDLE
4. IF STRUCTURE REQUIRED WILL BE IN CLIENT SCOPE

Rev. no	Revision	Date	Revised by
1.	Clear width reduced by 220mm	14/04/2023	Sujata

This drawing & design is the property of NIHVA TECHNOLOGIES. Not to be sold or copied to any other concern.

TITLE
ALUMINUM HIGH SPEED ROLLING SHUTTER

NIHVA TECHNOLOGIES PVT. LTD.

	NAME	SIGN	DATE
DRAWN	SUJATA		11/04/2023
CHECK	A.K		11/04/2023
APPRD.	V.T		11/04/2023

If any queries contact : design1@nihva.com

CLIENT -Kohler India Corporation Pvt. Ltd
PROJECT - AL RS
SITE LOCATION - GUJARAT
DWG. NO. : NIHVA/22-23/CLT/0199 REV- 0
ALL DIMENSION ARE IN mm SCALE: NTS WT: SHEET: 01 OF 01