
1 GROUND FLOOR

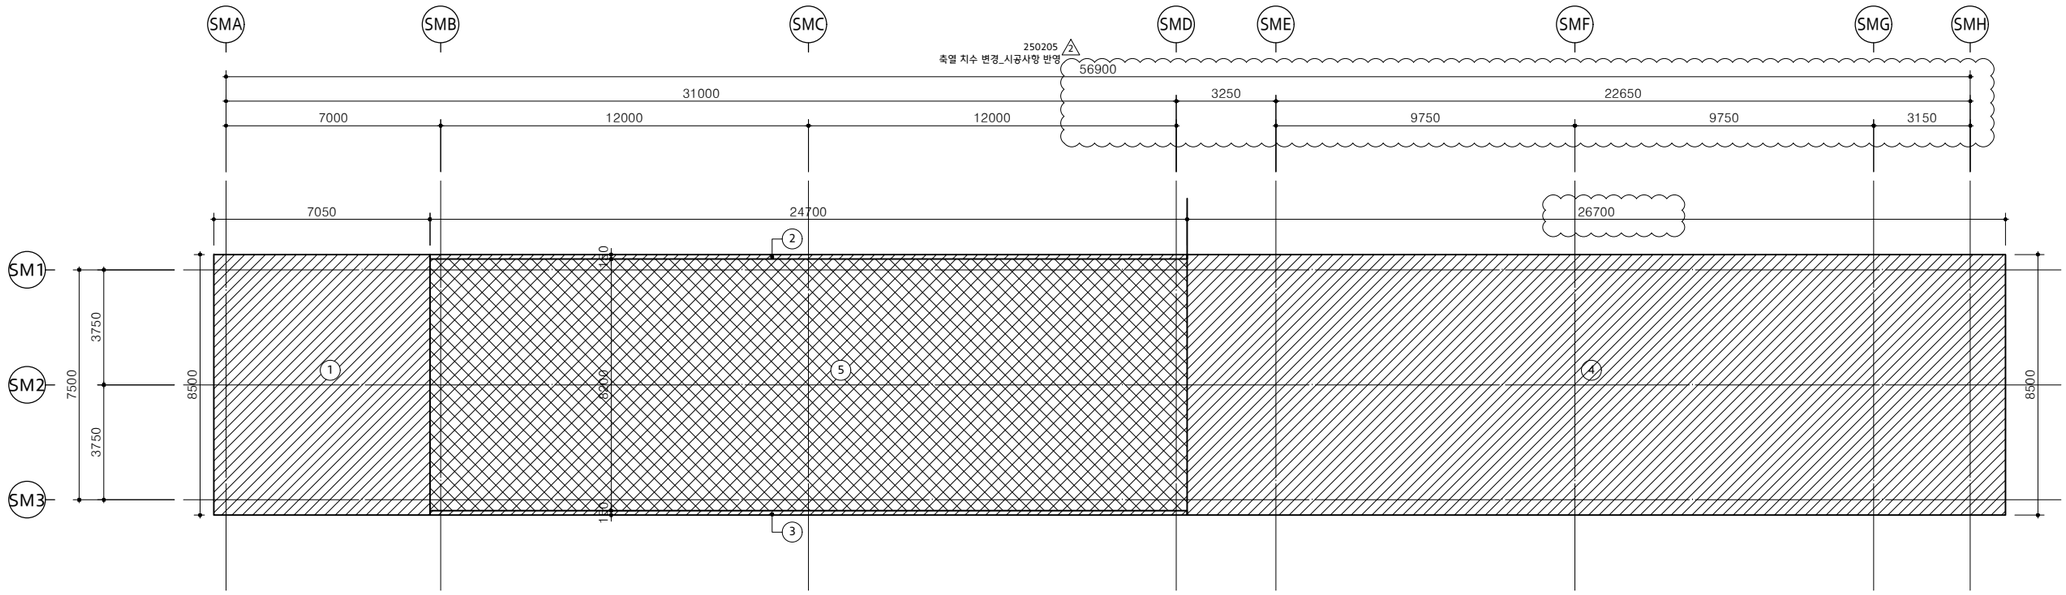

NO.	CALCULATING TABLE	AREA (㎡)	REMARK
1	7.05 X 8.50	59.93	CANOPY
2	24.70 X 0.15	3.70	
3	24.70 X 0.15	3.70	
4	26.70 X 8.5	226.95	
5	24.70 X 8.20	202.54	BUILDING
TOTAL	1 + 2 + 3 + 4 + 5	496.82	

250205 2 축열 치수 변경_시공사항 반영

250205 2 축열 치수 변경_시공사항 반영

KEY PLAN

NOTE

REV.	DESCRIPTION	DRAWN	DATE
2	CD Rev.2	OH.J.S	2025. 02.14
1	CD Rev.1	OH.J.S	2024. 10.18
0	CONSTRUCTION DRAWING	OH.J.S	2024. 07.30
A	DESIGN DEVELOPMENT	OH.J.S	2024. 06.28

CLIENT

HYUNDAI

ARCHITECTS & ENGINEERS

JUNGLIM ARCHITECTURE

PROJECT TITLE

PUNE HMI PROJECT

DRAWING TITLE

[MAIN SECURITY OFFICE]
AREA TABULATION


SCALE A1:1/100 A3:1/200	DRAWN	CHECKED	REVIEWED	APPROVED	APPROVED
	OH.J.S	HONG.G.D	LEE.S.L	HEC INDIA	PARK.T.S
DATE 14 FEB,2025					

MAIN CONTRACTOR

HEC INDIA LLP


DRAWING NO. WA-IPB-645-A-0501 REV. 2

A1 SIZE (841mm x 594mm)

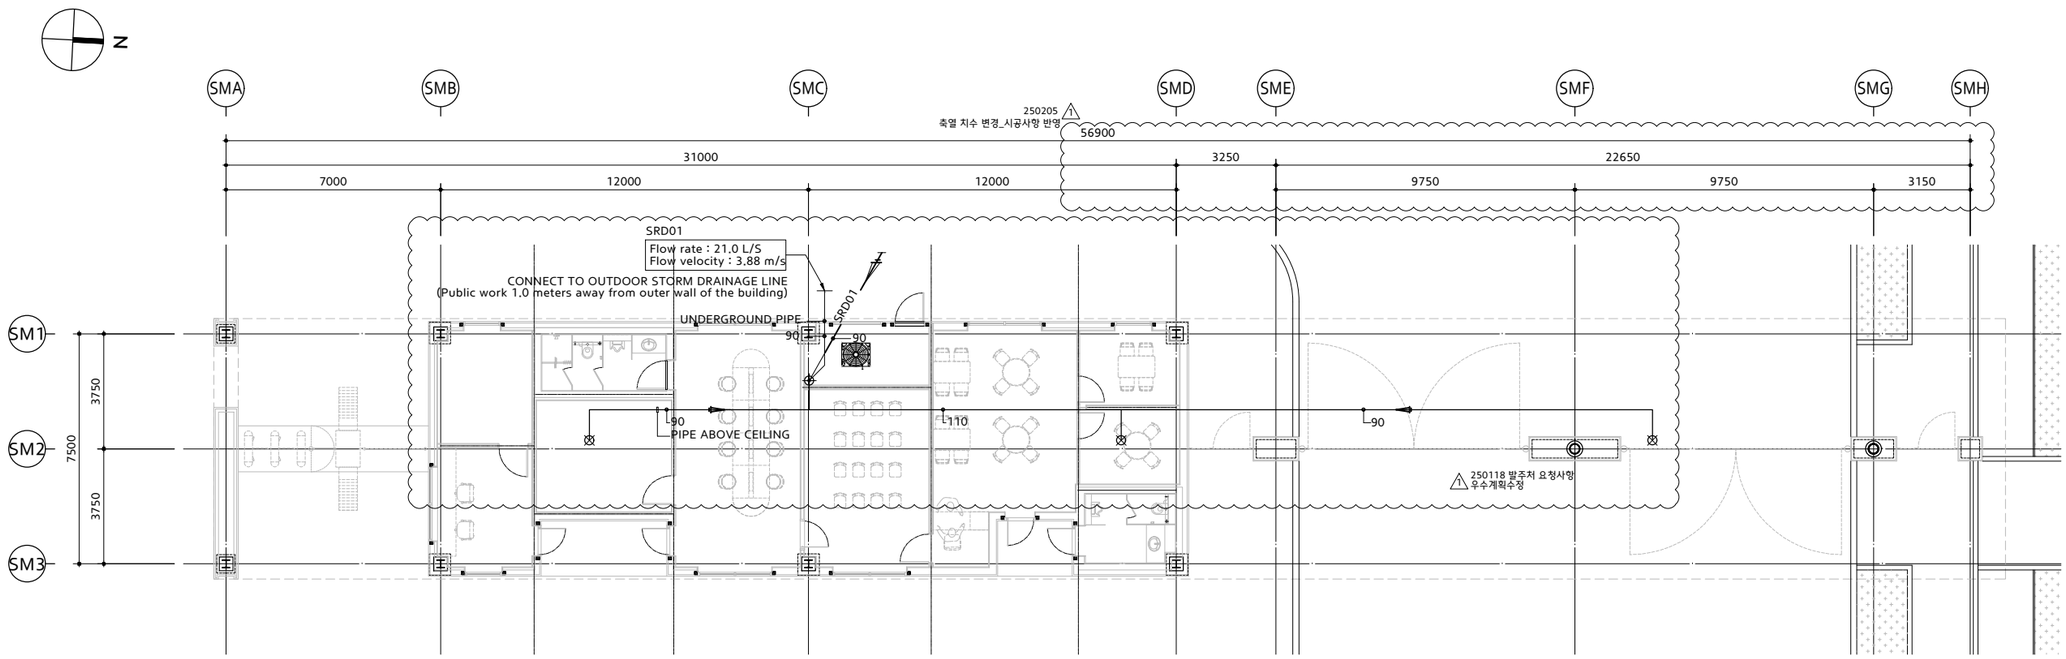


1 GROUND FLOOR STORMWATER DRAIN PLAN

SCALE : 1/100

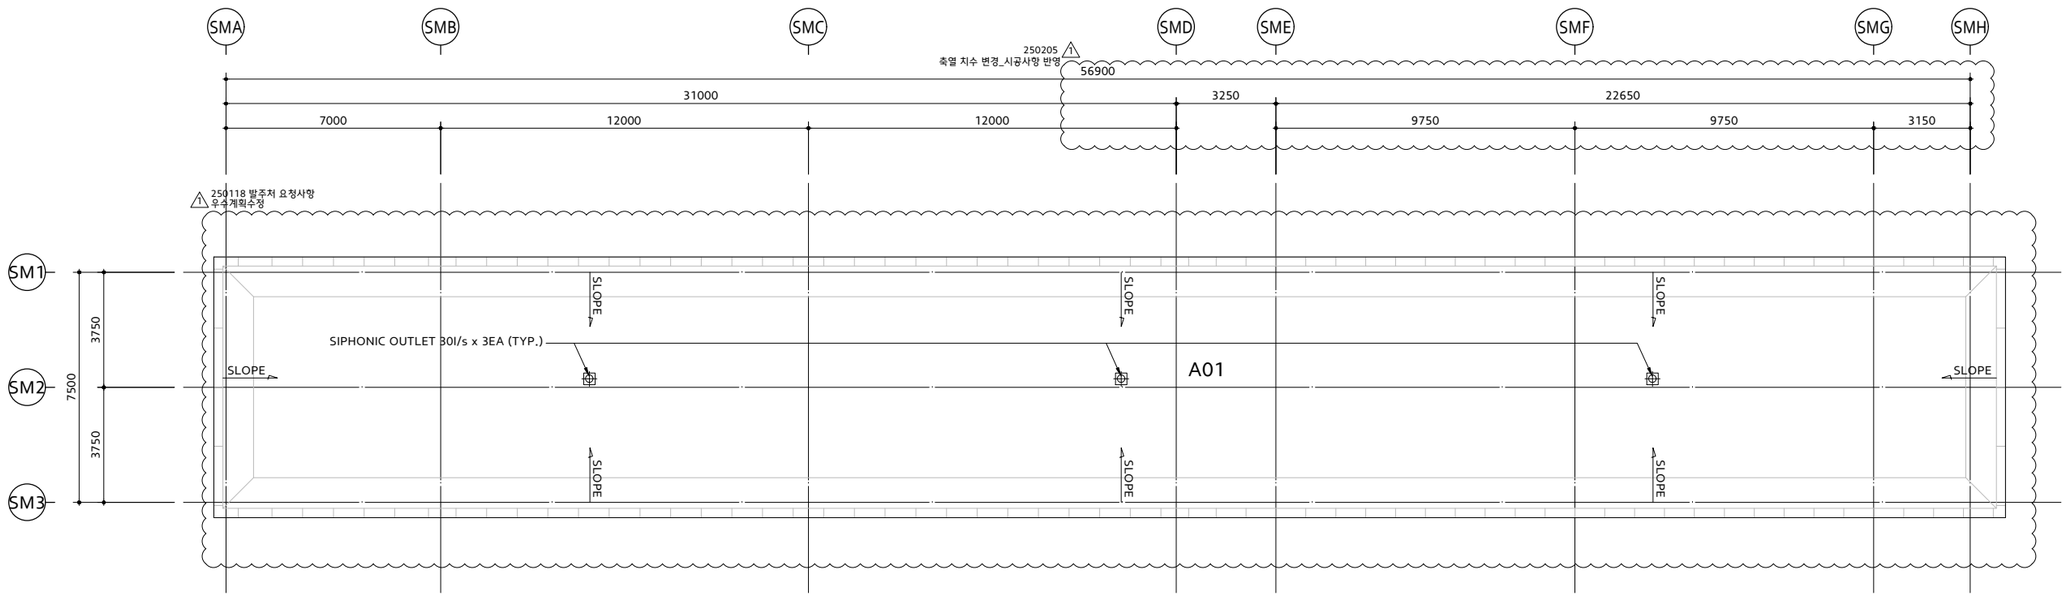

2 ROOF STORMWATER DRAIN PLAN

SCALE : 1/100

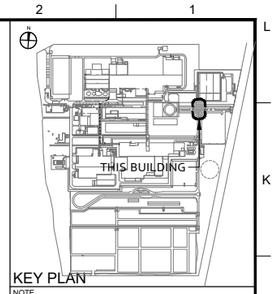

KEY PLAN

NOTE

1. GROUND FLOOR LEVEL
   -GROUND FLOOR FL ±0.00 = EL+663.20
2. LEVEL(T.O.C) OF GROUND FLOOR, WHICH IS THE BASE LEVEL OF ALL LEVEL DIMENSIONS.
3. THIS DRAWING SHOULD BE APPROVED BY HEC & HMI BEFORE APPLICATION
4. REFER TO DRAWING NUMBER "000-G-0001~0900" FOR GENERAL NOTES AND STANDARDS DETAIL.
5. SITE SURVEY FOR THIS DRAWING SHALL BE REQUIRED AND SUPERVISOR'S APPROVAL SHALL BE OBTAINED PRIOR TO CONSTRUCTION.
6. IF THE DRAWING IS DIFFERENT FROM CURRENT SITE, SUPERVISORS AND DESIGNER'S APPROVAL SHALL BE OBTAINED PRIOR TO CONSTRUCTION.
7. STRUCTURES IN THE BUILDING SHOULD BE ALKYD ENAMEL PAINT ON ANTI- RUST PAINT.
8. ALL SEALANT SHALL BE SUBMITTED TO THE MANUFACTURING ENGINEERING TEAM AND APPROVED PRIOR TO THE INSTALLATION BY THEM.

REV.	DESCRIPTION	DRAWN	DATE
1	CD Rev.1	OH,J.S	2025. 02.14
0	CONSTRUCTION DRAWING	OH,J.S	2024. 07.30

CLIENT

HYUNDAI

ARCHITECTS & ENGINEERS

JUNGLIM ARCHITECTURE

PROJECT TITLE

PUNE HMI PROJECT

DRAWING TITLE

[MAIN SECURITY OFFICE]
GROUND FLOOR & ROOF STORMWATER DRAIN PLAN

SCALE	DRAWN	CHECKED	REVIEWED	APPROVED	APPROVED
A1: 1/100 A3:1/200	OH,J.S	HONG,G.D	LEE,S.L	HEC INDIA	PARK,T.S
DATE					
14 FEB,2025					


MAIN CONTRACTOR

HEC HANLIM

DRAWING NO. WA-IPB-645-A-3002

REV. 1

A1 SIZE (841mm x 594mm)

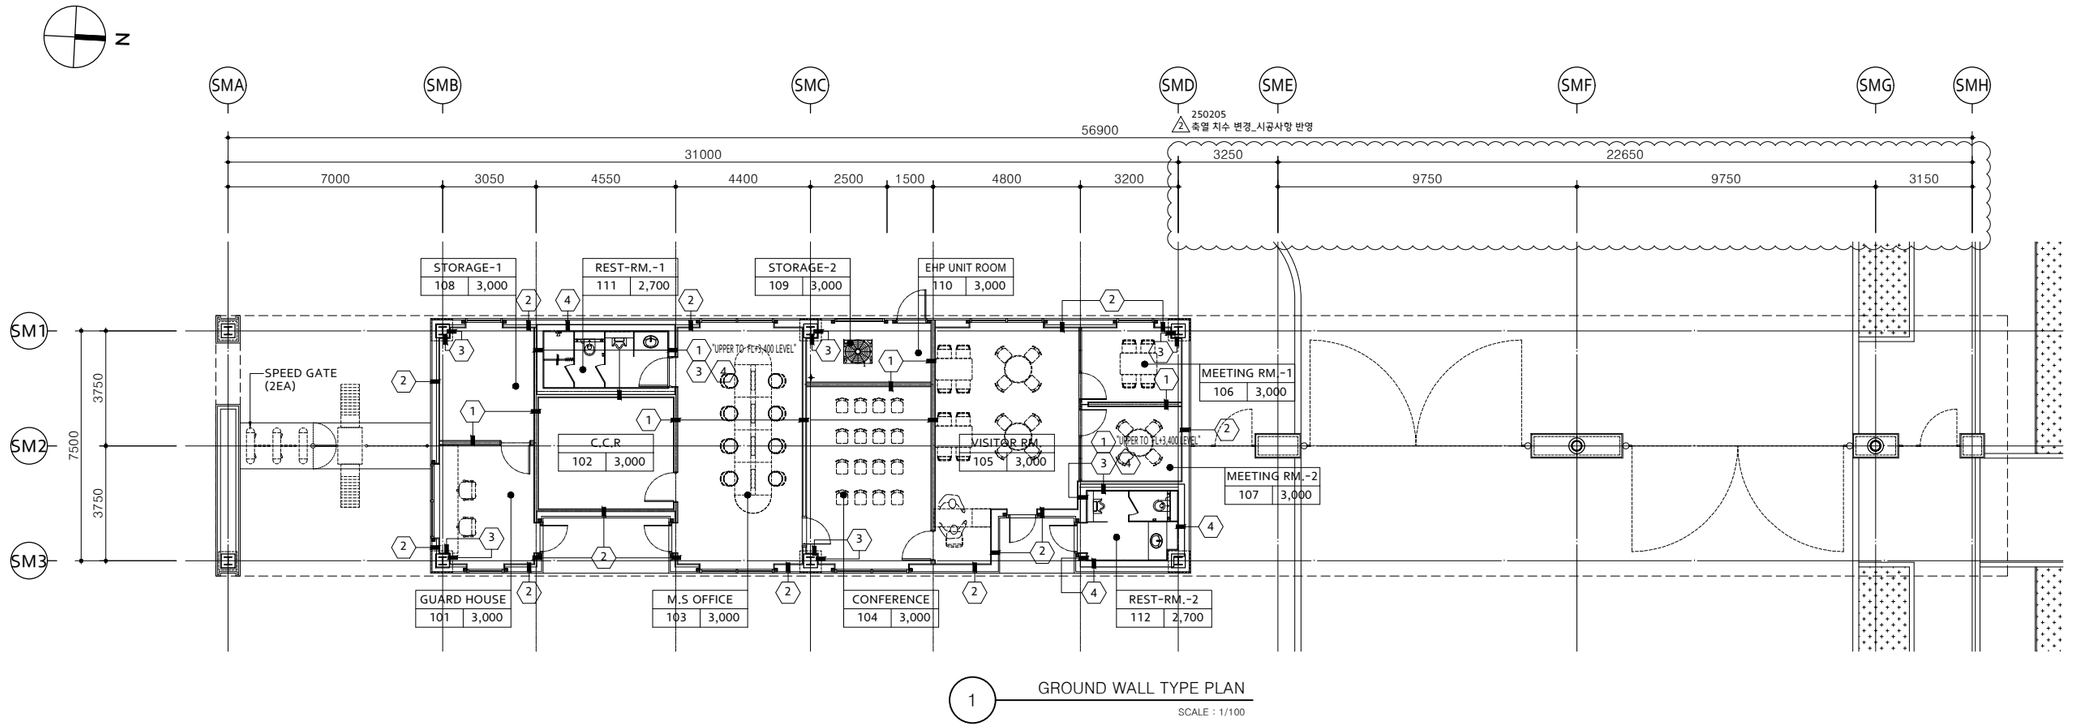

1 GROUND WALL TYPE PLAN

SCALE : 1/100

KEY PLAN


NOTE

WALL TYPE SCHEDULE


WALL NO.	TYPE	STUD SPEC. SHAPE	STUD SPEC. SIZE	STUD SPEC. L	RUNNER	GYP. BD TYPE	HEIGHT (MAX.)	WALL THICKNESS (T)	INSULATION	REMARK
1	GA	C	100*45*0.8	300	102*40*0.8	G	5.60	150		GYP. BD. TYPE -G: GENERAL GYP. BD THK. 12.5 2PLY
2	GB	C	100*45*0.8	300	102*40*0.8	G	5.60	125		
3	GB	C	50*45*0.8	300	52*40*0.8	G	3.63	75		
4	BB	-	-	-	-	-	-	220		

WALL TYPE DETAIL


TYPE-GA

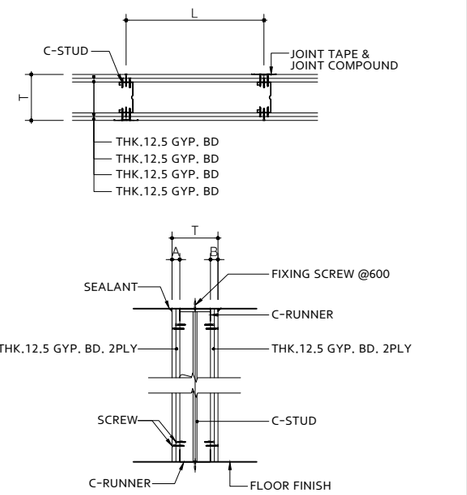


TYPE-GB

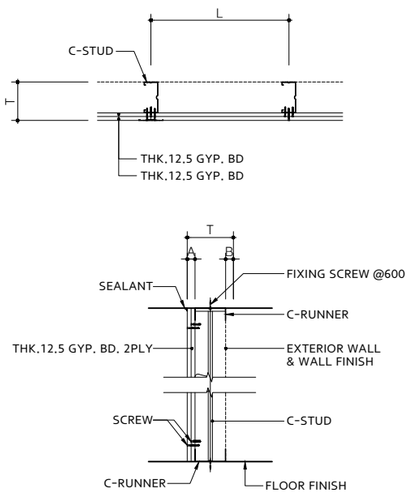

TYPE-BA

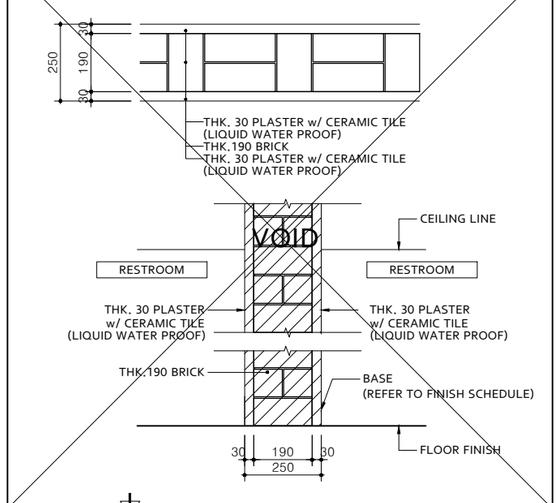

TYPE-BB

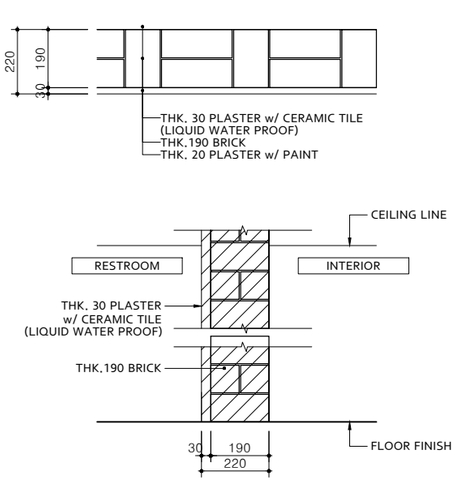

REV.	DESCRIPTION	DRAWN	DATE
2	CD Rev.2	OH.J.S	2025.02.14
1	CD Rev.1	OH.J.S	2024.10.18
0	CONSTRUCTION DRAWING	OH.J.S	2024.07.30
A	DESIGN DEVELOPMENT	OH.J.S	2024.06.28

CLIENT: HYUNDAI

ARCHITECTS & ENGINEERS: JUNGLIM ARCHITECTURE

PROJECT TITLE: PUNE HMI PROJECT

DRAWING TITLE: [MAIN SECURITY OFFICE] WALL TYPE PLAN & DETAIL


SCALE	DRAWN	CHECKED	REVIEWED	APPROVED	APPROVED
A1:1/100 A3:1/200	OH.J.S	HONG.G.D	LEE.S.L	HEC INDIA	PARK.T.S
DATE: 14 FEB.2025					

MAIN CONTRACTOR: HEC INDIA LLP

DRAWING NO.: WA-IPB-645-A-5401

REV.: 2

A1 SIZE (841mm x 594mm)

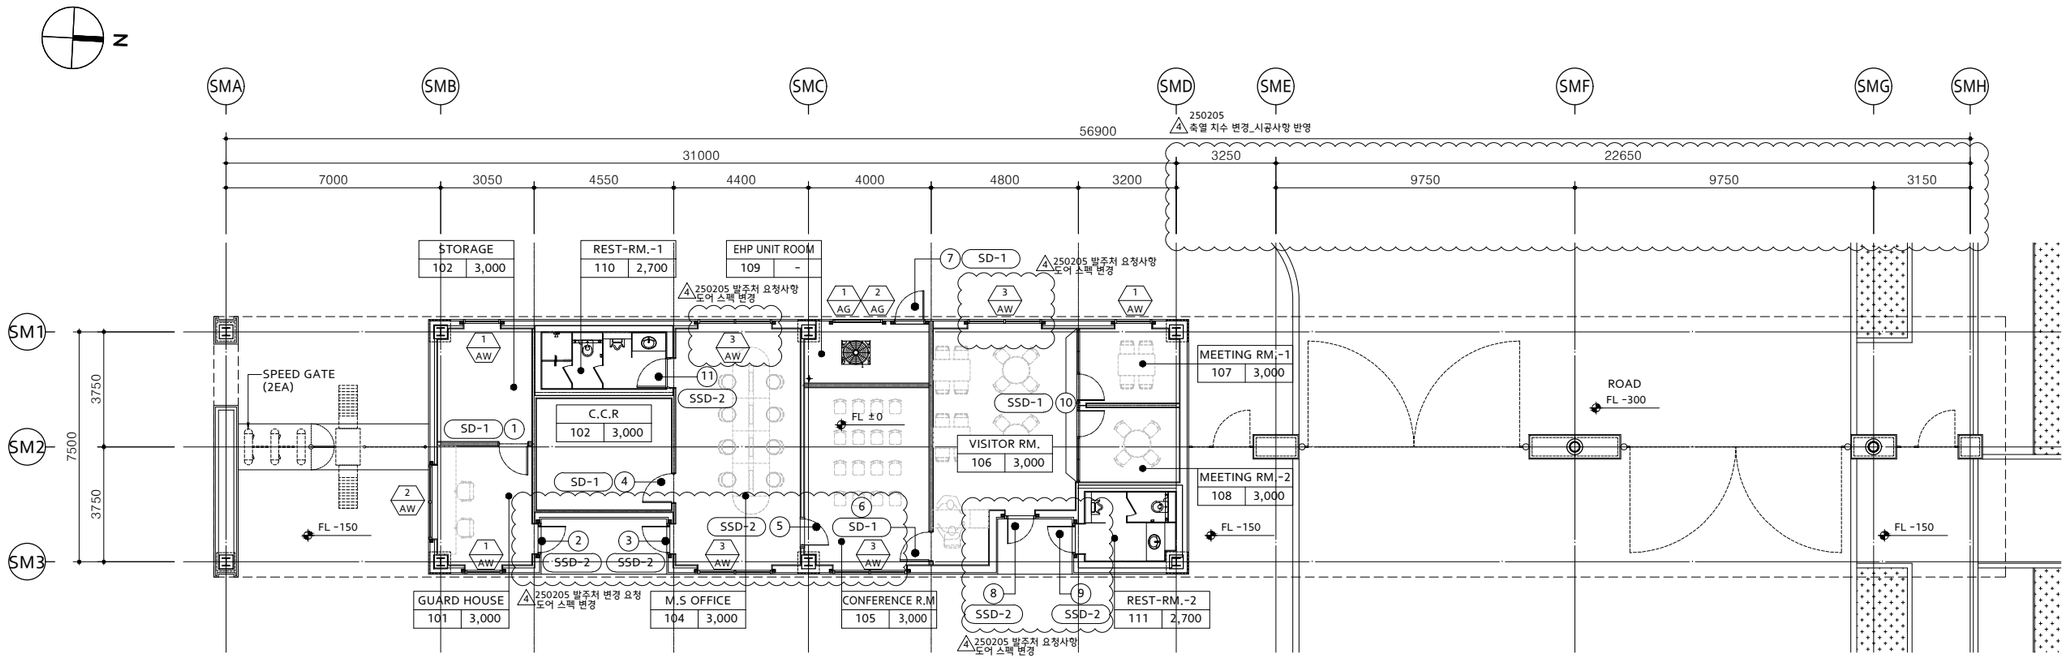


1 GROUND FLOOR DOOR & WINDOW PLAN

SCALE : 1/100

KEY PLAN

NOTE

1. IF APPLICABLE TO EXISITING DOORS, WINDOWS CONSTRUCTION SHALL BE CARRIED OUT CLIENT'S, CONTRACTOR'S APPROVAL.
2. VARIOUS OPENINGS MUST BE DETERMINED IN ADVANCE BY SHOP DWG OF THE RELEVANT WORK TYPE
3. PROVIDE 15mm GAP BETWEEN INSIDE FACE OF STEEL FRAMING AND CLEAR OPENINGS.

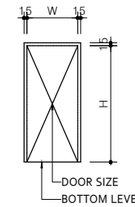


DOOR SHAPE & LEGEND

1	GENERAL NOTE	2	DOOR & WINDOW TYPE



SD	STEEL DOOR	OHD	OVERHEAD DOOR
FSD	FIRE STEEL DOOR	RS	ROOL-UP SHUTTER
SSD	S' STEEL DOOR	RRS	RAPID ROOL-UP SHUTTER
SFD	S' STEEL FOLDING DOOR	AW	ALUMINUM WINDOW
ASD	AUTO SLIDING DOOR	SSW	S' STEEL WINDOW
SLID	SLID DOOR	AG	ALUMINUM GRILL

3 DOOR SHAPE : SINGLE DOOR

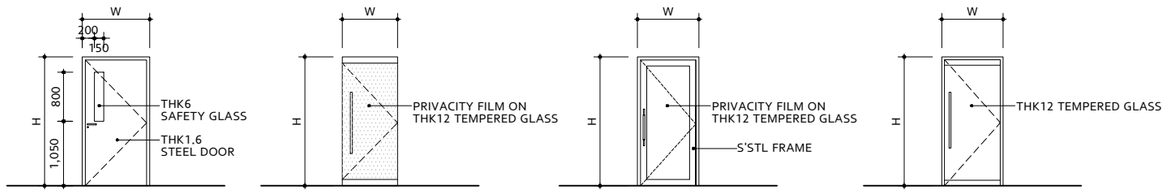


DOOR SHAPE - S1 | DOOR SHAPE - S2 | DOOR SHAPE - S3 | DOOR SHAPE - S4

DOOR SCHEDULE


FLOOR NO.	NO.	DOOR NO.	MATERIAL		DOOR SIZE			SHAPE	MATERIAL			FIRE	KEY SET	HW SET	REMARKS
			DOOR	FRAME	THK	WIDTH	HEIGHT		HEAD	JAMB	SILL				
1F	1	SD-1	STL	STL	45	1,000	2,100	S1	-	-	-	-	-	110	4 250205 발주처 요청사항 도어 스펙 변경
	2	SSD-2	GLASS	S'STL	45	1,000	2,100	S3	-	-	-	-	-	521	
	3	SSD-2	GLASS	S'STL	45	1,000	2,100	S3	-	-	-	-	-	521	
	4	SD-1	STL	STL	45	1,000	2,100	S1	-	-	-	-	-	110	
	5	SSD-2	GLASS	S'STL	45	1,000	2,100	S4	-	-	-	-	-	516	
	6	SD-1	STL	STL	45	1,000	2,100	S1	-	-	-	-	-	110	
	7	SD-1	STL	STL	45	1,000	2,100	S1	-	-	-	-	-	110	4 250205 발주처 요청사항 도어 스펙 변경
	8	SSD-2	GLASS	S'STL	45	1,000	2,100	S3	-	-	-	-	-	521	
	9	SSD-2	GLASS	S'STL	45	1,000	2,100	S3	-	-	-	-	-	521	
	10	SSD-1	REFER TO "DOOR EXTEND ELEVATIONS"											512	
	11	SSD-2	GLASS	S'STL	45	1,000	2,100	S2	-	-	-	-	-	501	

250205 발주처 요청사항 도어 스펙 변경


WINDOW SCHEDULE

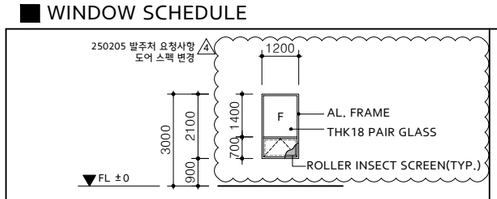


ID	1 AW	ALUMINUM WINDOW	QT'Y	3 EA
GLAZING	THK18 PAIR GLASS			
FRAME	AL.BAR / ELECTROSTATIC POWDER COATING			
HARDWARE	-			

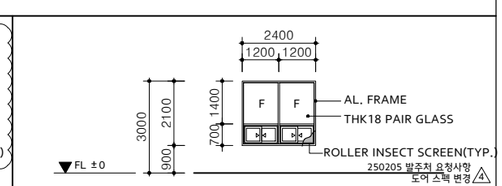


ID	2 AW	ALUMINUM WINDOW	QT'Y	1 EA
GLAZING	THK18 PAIR GLASS			
FRAME	AL.BAR / ELECTROSTATIC POWDER COATING			
HARDWARE	- 4 250205 발주처 요청사항 도어 스펙 변경			

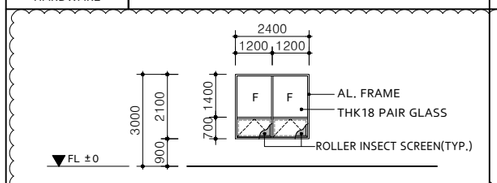

ID	3 AW	ALUMINUM WINDOW	QT'Y	4 EA
GLAZING	THK18 PAIR GLASS			
FRAME	AL.BAR / ELECTROSTATIC POWDER COATING			
HARDWARE	-			

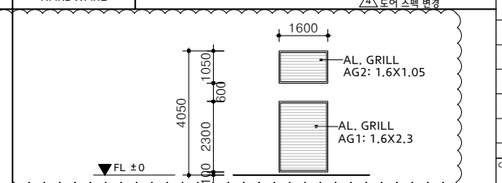

ID	1 AG 2 AG	ALUMINUM GRILL	QT'Y	2 EA
GLAZING	-			
FRAME	AL.BAR / ELECTROSTATIC POWDER COATING			
HARDWARE	-			

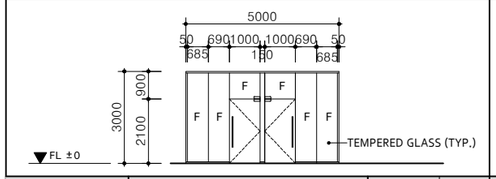

ID	SSD-1	QT'Y	1 EA
GLAZING	THK12 TEMPERED GLASS		
FRAME	100x50x1.5 SST FRAME(HAIR LINE)		
HARDWARE	-		

ID		QT'Y	
GLAZING			
FRAME			
HARDWARE			

REV.	DESCRIPTION	DRAWN	DATE
4	CD Rev.4	OH.J.S	2025. 02.14
3	CD Rev.3	OH.J.S	2025. 01.08
2	CD Rev.2	OH.J.S	2024. 11.29
1	CD Rev.1	OH.J.S	2024. 10.18
0	CONSTRUCTION DRAWING	OH.J.S	2024. 07.30
A	DESIGN DEVELOPMENT	OH.J.S	2024. 06.28

CLIENT: HYUNDAI

ARCHITECTS & ENGINEERS: JUNGLIM ARCHITECTURE

PROJECT TITLE: PUNE HMI PROJECT

DRAWING TITLE: [MAIN SECURITY OFFICE] DOOR, WINDOW PLAN & SCHEDULE

SCALE	DRAWN	CHECKED	REVIEWED	APPROVED	APPROVED
A1:1/100 A3:1/200	OH.J.S	HONG.G.D	LEE.S.L	HEC INDIA	PARK.T.S
DATE: 14 FEB,2025					

MAIN CONTRACTOR: HEC INDIA LLP

DRAWING NO.: WA-IPB-645-A-6101 REV.: 4

A1 SIZE (841mm x 594mm)

HW	ITEM	DESCRIPTION	MANUFACT	MODEL	Q`TY
512	BDL-01	BOTTOM RAIL DEADLOCK	ADAMS RITE	MS1861/SFIC/4066	1 SET
512	DH-35	PUSH PULL HANDLE	ZERO	UNO G5955-01-024	1 SET
512	DPS-01	DUST PROOF STRIKE	IVES	DP1	1 EA
512	FH-07	FLOOR HINGE	CISA	F8500-AB	1 EA
516	BDL-01	BOTTOM RAIL DEADLOCK	ADAMS RITE	MS1861/SFIC/4066	1 SET
516	DH-35	PUSH PULL HANDLE	ZERO	UNO G5955-01-024	1 SET
516	DPS-01	DUST PROOF STRIKE	IVES	DP1	1 EA
516	FH-07	FLOOR HINGE	CISA	F8500-AB	1 EA
516	PF-12	TOP FITTING	CISA	PF20-12-SS	1 EA
516	PF-13	TRANSOM FITTING WITH PIVOT	CISA	PF40-12-SS	1 EA
600	BDL-01	BOTTOM RAIL DEADLOCK	ADAMS RITE	MS1861/SFIC/4066	2 SET
600	DH-35	PUSH PULL HANDLE	ZERO	UNO G5955-01-024	2 SET
600	DPS-01	DUST PROOF STRIKE	IVES	DP1	2 EA
600	FH-07	FLOOR HINGE	CISA	F8500-AB	2 EA
601	BDL-01	BOTTOM RAIL DEADLOCK	ADAMS RITE	MS1861/SFIC/4066	2 SET
601	DH-35	PUSH PULL HANDLE	ZERO	UNO G5955-01-024	2 SET
601	DPS-01	DUST PROOF STRIKE	IVES	DP1	2 EA
601	FH-08	FLOOR HINGE	CISA	F5500-AB	2 EA
611	BDL-01	BOTTOM RAIL DEADLOCK	ADAMS RITE	MS1861/SFIC/4066	2 SET
611	DH-35	PUSH PULL HANDLE	ZERO	UNO G5955-01-024	2 SET
611	DPS-01	DUST PROOF STRIKE	IVES	DP1	2 EA
611	FH-07	FLOOR HINGE	CISA	F8500-AB	2 EA
611	PF-12	TOP FITTING	CISA	PF20-12-SS	2 EA
611	PF-13	TRANSOM FITTING WITH PIVOT	CISA	PF40-12-SS	2 EA
620	BDL-01	BOTTOM RAIL DEADLOCK	ADAMS RITE	MS1861/SFIC/4066	2 SET
620	DH-05	PUSH PULL HANDLE	ZERO	UNO T67	2 SET
620	DPS-01	DUST PROOF STRIKE	IVES	DP1	2 EA
620	FH-08	FLOOR HINGE	CISA	F5500-AB	2 EA
623	BDL-01	BOTTOM RAIL DEADLOCK	ADAMS RITE	MS1861/SFIC/4066	2 SET
623	DH-35	PUSH PULL HANDLE	ZERO	UNO G5955-01-024	2 SET
623	DPS-01	DUST PROOF STRIKE	IVES	DP1	2 EA
623	FH-08	FLOOR HINGE	CISA	F5500-AB	2 EA
700	DH-02	PUSH PULL HANDLE	ZERO	UNO PH001SS	1 SET
700	SDH-31	SLIDING DAMPING SET	BRIO	QR120S-S1PK W/ 120SCT	1 EA
700	SDL-01	SLIDING DOOR LOCK	ADAMS RITE	MS1890/SFIC/4066	1 SET
700	SDT-01	SLIDING DOOR TRACK-2M	BRIO	120F-2M	1 EA
701	DH-02	PUSH PULL HANDLE	ZERO	UNO PH001SS	1 SET
701	SDH-31	SLIDING DAMPING SET	BRIO	QR120S-S1PK W/ 120SCT	1 EA
701	SDT-02	SLIDING DOOR TRACK-3M	BRIO	120F-3M	1 EA

1 250205 발주처 변경 요청: 도어 스팩 추가

521	BDL-01	BOTTOM RAIL DEADLOCK	ADAMS RITE	MS1861/SFIC/4066	1 SET
521	DH-01	PUSH PULL HANDLE	ZERO	UNO T5955-01-024	1 SET
521	DPS-01	DUST PROOF STRIKE	IVES	DP1	1 EA
521	FH-07	FLOOR HINGE	CISA	F8500-AB	1 EA

HW	ITEM	DESCRIPTION	MANUFACT	MODEL	Q`TY

KEY PLAN

NOTE

REV.	DESCRIPTION	DRAWN	DATE
1	CD Rev.1	OH.J.S	2025. 02.14
0	CONSTRUCTION DRAWING	OH.J.S	2024. 11.29

CLIENT

HYUNDAI

ARCHITECTS & ENGINEERS

JUNGLIM ARCHITECTURE

PROJECT TITLE

PUNE HMI PROJECT

DRAWING TITLE

[MAIN SECURITY OFFICE]
DOOR HARDWARE LIST-3

SCALE A1:1/100 A3:1/200	DRAWN	CHECKED	REVIEWED	APPROVED	APPROVED
	OH.J.S	HONG.G.D	LEE.S.I.	HEC INDIA	PARK.T.S
DATE					
14 FEB,2025					

MAIN CONTRACTOR

HEC

DRAWING NO.	REV.
WA-IPB-645-A-6104	1

A1 SIZE (841mm x 594mm)

구 분	AUTO FLUSH BOLT	ARMOR PLATE	BOTTOM RAIL DEADLOCK	BUTT HINGE(SST'L) 5"X4"	BUTT HINGE(SST'L) 4"X4"	DIGITAL LOCK	PUSH PULL PLATE	⚠1 250205 발주처 변경 요청: 도어 스팩 추가		
모 델	FB31P-12-MD	8400-42X36"	MS1861/SFIC/4066	AH500-5X4"	AH500-4X4"	S-8100	8302-4X16"			
제조업체	IVES	IVES	ADAMS RITE	BRITON	BRITON	SCHLAGE	IVES			
비 고	AFB-01	AP-01	BDL-01	BH-49	BH-56	CK-05	PP-01			
구 분	DOOR CLOSER NHO	DOOR CLOSER NHO	FLOOR STOP	WALL BUMPER	FLOOR STOP	FLUSH BOLT-12"/24"	DUST PROOF STRIKE	PUSH PULL HANDLE	PUSH PULL HANDLE	PUSH PULL HANDLE
모 델	SC71A-RW/PA	SC81A-RW/PA	FS436	WS401/402CVX	FS444	FB458-MD	DP1	UNO T5955-01-024	UNO G5955-01-024	UNO PH001SS
제조업체	FALCON	FALCON	IVES	IVES	IVES	IVES	IVES	ZERO	ZERO	ZERO
비 고	DC-01	DC-06	DS-01	DS-05	DS-09	FB-02, 03	DPS-01	DH-01	DH-35	DH-02
구 분	FLOOR HINGE	FLOOR HINGE	GLASS DEADLOCK	MORTISE DEADLOCK	MORTISE LOCKSET-PASSAGE	MORTISE LOCKSET-ENTRANCE	MORTISE LOCKSET-CLASSROOM	MORTISE LOCKSET-STOREROOM	MORTISE DUMMY TRIM	
모 델	F8500-AB	F5500-AB	MS1850/SFIC/4066	M64L/SFIC	M10 07B	M56L/SFIC/07B	M70L/SFIC/07B	M80L/SFIC/07B	M172 07B	
제조업체	CISA	CISA	Adans Rite	SCHLAGE	SCHLAGE	SCHLAGE	SCHLAGE	SCHLAGE	SCHLAGE	
비 고	FH-07	FH-08	GDL-01	MDL-001	MDL-049	MDL-051	MDL-053	MDL-054	MDT-008	
구 분	PATCH LOCK	BOTTOM FITTING	TOP FITTING	TRANSOM FITTING WITH PIVOT	PIVOT HINGE(OFFSET HUNG)	INTERMEDIATE PIVOT HINGE	SLIDING DAMPING SET	SLIDING DOOR LOCK	SLIDING DOOR TRACK-2M	PUSH PULL HANDLE
모 델	PL10-12-SS-CY	PF10-12-SS-G	PF20-12-SS	PF40-12-SS	6200-SET-SS	6200-INT-SS	QR120S-S1PK W/ 120SCT	MS1890/SFIC/4066	120F-2M	UNO T67
제조업체	CISA	CISA	CISA	CISA	BRITON	BRITON	BRIO	ADAMS RITE	BRIO	ZERO
비 고	PF-06	PF-10	PF-12	PF-13	PH-03	PH-04	SDH-31	SDL-01	SDT-01	DH-05
구 분	SLIDING DOOR TRACK-3M	SPECIAL HINGE	INTERMEDIATE PIVOT	DOOR COORDINATOR						
모 델	120F-3M	7237F-SET	7230F-7237F INT	COR Serise						
제조업체	BRIO	IVES	IVES	IVES						
비 고	SDT-02	SH-10	SH-10A	CO-01, 07						

KEY PLAN

NOTE

REV.	DESCRIPTION	DRAWN	DATE
1	CD Rev.1	OH.J.S	2025. 02.14
0	CONSTRUCTION DRAWING	OH.J.S	2024. 11.29

CLIENT

HYUNDAI

ARCHITECTS & ENGINEERS

JUNGLIM ARCHITECTURE

PROJECT TITLE

PUNE HMI PROJECT

DRAWING TITLE

[MAIN SECURITY OFFICE]
DOOR HARDWARE LIST-4

SCALE A1:1/100 A3:1/200	DRAWN	CHECKED	REVIEWED	APPROVED	APPROVED
	OH.J.S	HONG.G.D	LEE.S.L	HEC INDIA	PARK.T.S
DATE 14 FEB,2025					


MAIN CONTRACTOR

HEC INDIA LLP

DRAWING NO. WA-IPB-645-A-6105


REV. 1

A1 SIZE (841mm x 594mm)

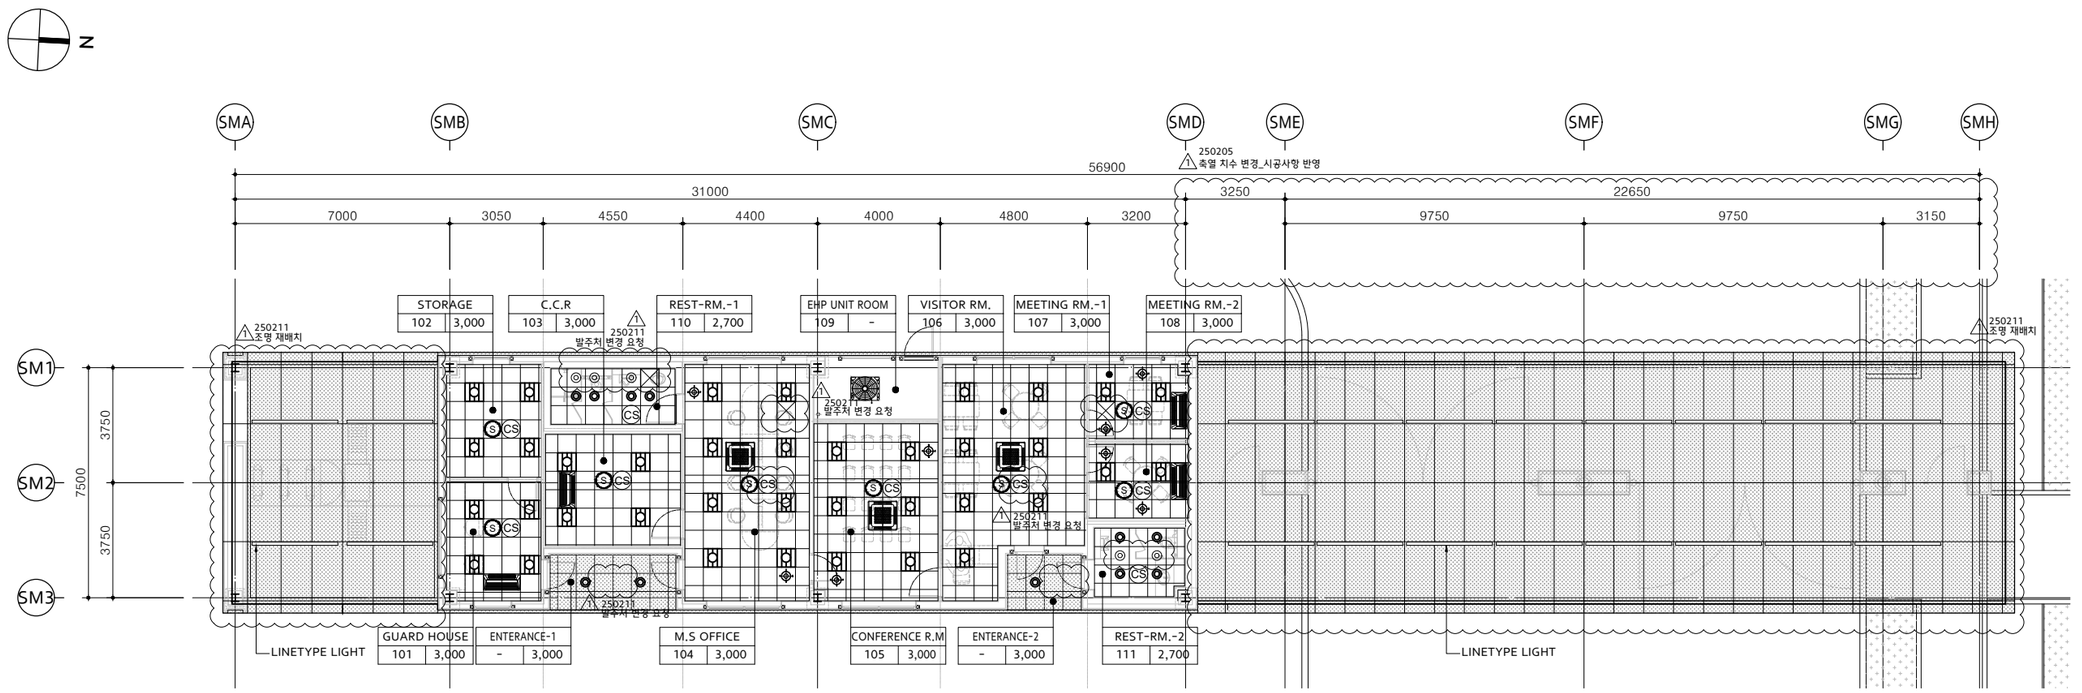

1 GROUND FLOOR CEILING PLAN

SCALE : 1/100

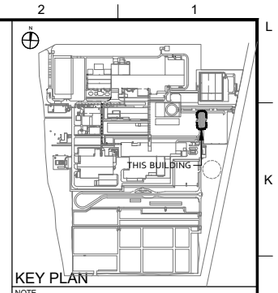

KEY PLAN

NOTE

1. GROUND FLOOR LEVEL
   -GROUND FLOOR FL ±0.00 = EL+659.50

2. LEVEL(T.O.C) OF GROUND FLOOR, WHICH IS THE BASE LEVEL OF ALL LEVEL DIMENSIONS.

3. THIS DRAWING SHOULD BE APPROVED BY HEC & HMI BEFORE APPLICATION

4. REFER TO DRAWING NUMBER "000-G-0001~0900" FOR GENERAL NOTES AND STANDARDS DETAIL.

5. SITE SURVEY FOR THIS DRAWING SHALL BE REQUIRED AND SUPERVISOR'S APPROVAL SHALL BE OBTAINED PRIOR TO CONSTRUCTION.

6. IF THE DRAWING IS DIFFERENT FROM CURRENT SITE, SUPERVISORS AND DESIGNER'S APPROVAL SHALL BE OBTAINED PRIOR TO CONSTRUCTION.

7. STRUCTURES IN THE BUILDING SHOULD BE ALKYD ENAMEL PAINT ON ANTI- RUST PAINT.

8. ALL SEALANT SHALL BE SUBMITTED TO THE MANUFACTURING ENGINEERING TEAM AND APPROVED PRIOR TO THE INSTALLATION BY THEM.

*LEGEND

: AL. SHEET

: ACOUSTIC CEILING TILE

: LINE TYPE LIGHT

■ CEILING FIXTURE LEGEND-M

SYMBOL	DESCRIPTION
	EHP (1WAY-TYPE)
	EHP (4WAY-TYPE)
	SUPPLY AIR
	EXHAUST AIR
	ROUND PAN DIFFUSER
	SERVICE OPENING

△1 250211 발주처 변경 요청

■ CEILING FIXTURE LEGEND-E

SYMBOL	DESCRIPTION
	LED 1/40W
	LED 1/15W

■ CEILING FIXTURE LEGEND-F

SYMBOL	DESCRIPTION
	K-FACTOR 80 QRS TYPE
S	COMBINATION DETECTOR 57° C
CS	3 WATT CEILING SPEAKER

REV.	DESCRIPTION	DRAWN	DATE
△1	CD Rev.1	OH.J.S	2025. 02.14
△0	CONSTRUCTION DRAWING	OH.J.S	2024. 11.29

CLIENT

HYUNDAI

ARCHITECTS & ENGINEERS

JUNGLIM ARCHITECTURE

PROJECT TITLE

PUNE HMI PROJECT

DRAWING TITLE

[MAIN SECURITY OFFICE]
GROUND FLOOR CEILING PLAN

SCALE	DRAWN	CHECKED	REVIEWED	APPROVED	APPROVED
A1: 1/100 A3:1/200	OH.J.S	HONG.G.D	LEE.S.L	HEC INDIA	PARK.T.S
DATE 14 FEB.2025					


MAIN CONTRACTOR

HEC INDIA LLP

DRAWING NO. WA-IPB-645-A-7001


REV. 1

A1 SIZE (841mm x 594mm)

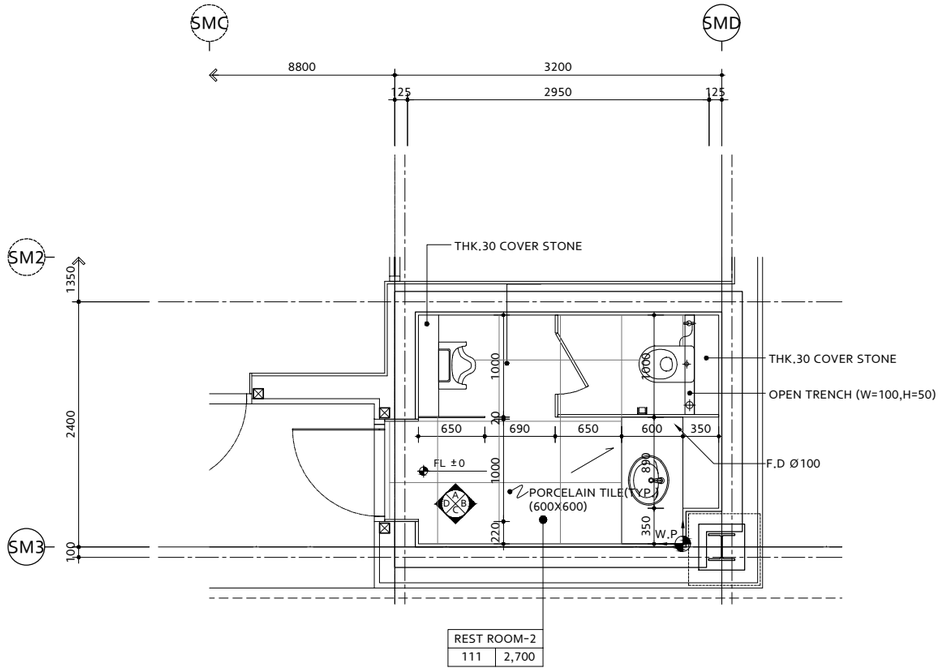


1 RESTROOM-2 FLOOR PLAN


SCALE : 1/30

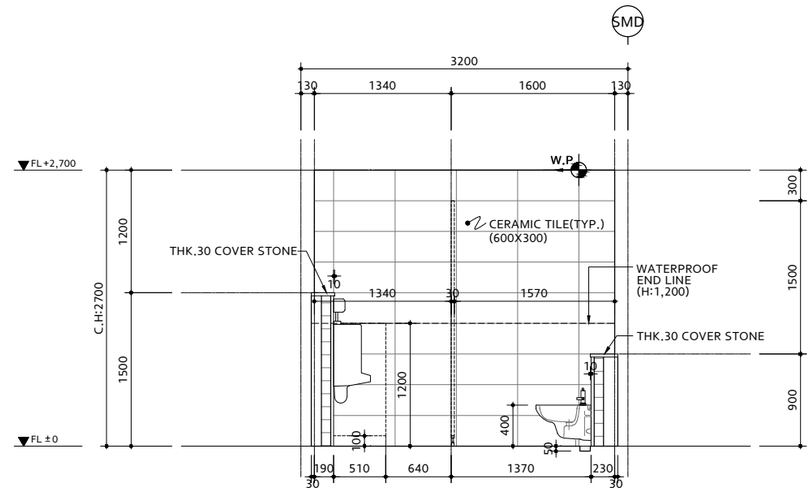


1 ELEVATION - A

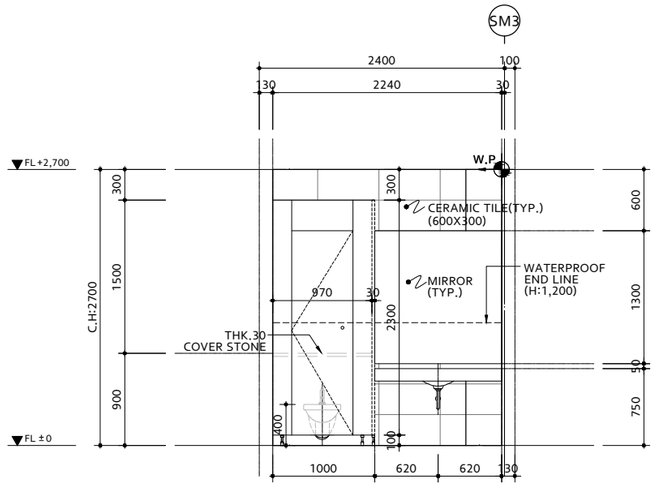

2 ELEVATION - B

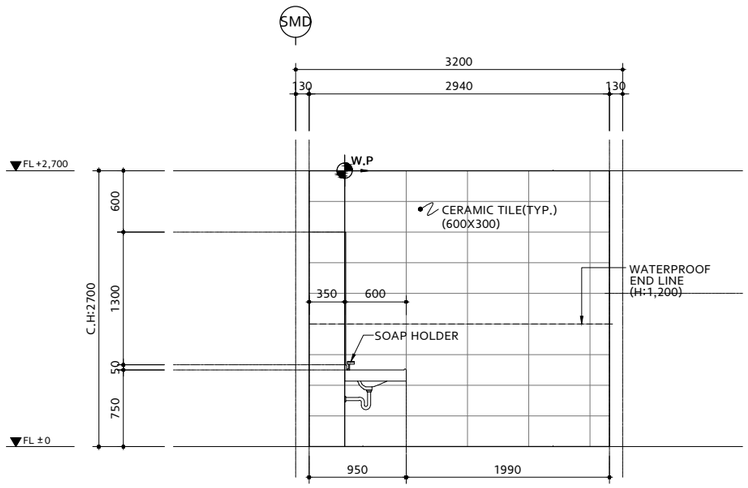

3 ELEVATION - C

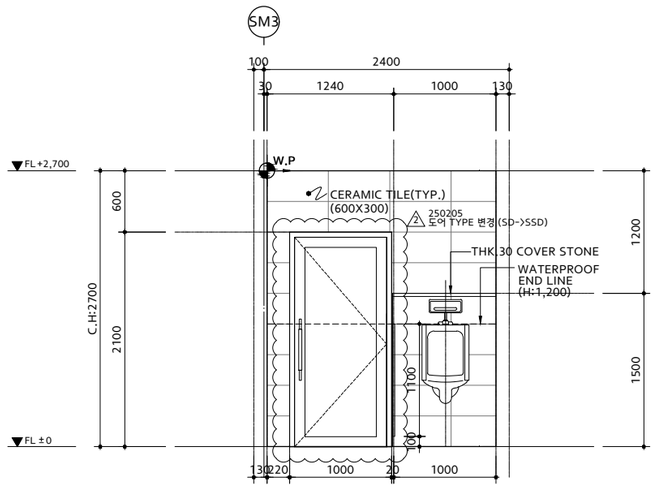

4 ELEVATION - D

KEY PLAN

NOTE

REV.	DESCRIPTION	DRAWN	DATE
2	CD Rev.2	OH.J.S	2025. 02.14
1	CD Rev.1	OH.J.S	2024. 11.29
0	CONSTRUCTION DRAWING	OH.J.S	2024. 07.30

CLIENT

HYUNDAI

ARCHITECTS & ENGINEERS

JUNGLIM ARCHITECTURE

PROJECT TITLE

PUNE HMI PROJECT

DRAWING TITLE

[MAIN SECURITY OFFICE]
RESTROOM ENLARGED PLAN & ELEVAITON-2

SCALE	DRAWN	CHECKED	REVIEWED	APPROVED	APPROVED
A1:1/30 A3:1/60	OH.J.S	HONG.G.D	LEE.S.L	HEC INDIA	PARK.T.S
DATE 14 FEB,2025					


MAIN CONTRACTOR

HEC KOREA LLP


DRAWING NO. WA-IPB-645-A-7502

REV. 2


A1 SIZE (841mm x 594mm)

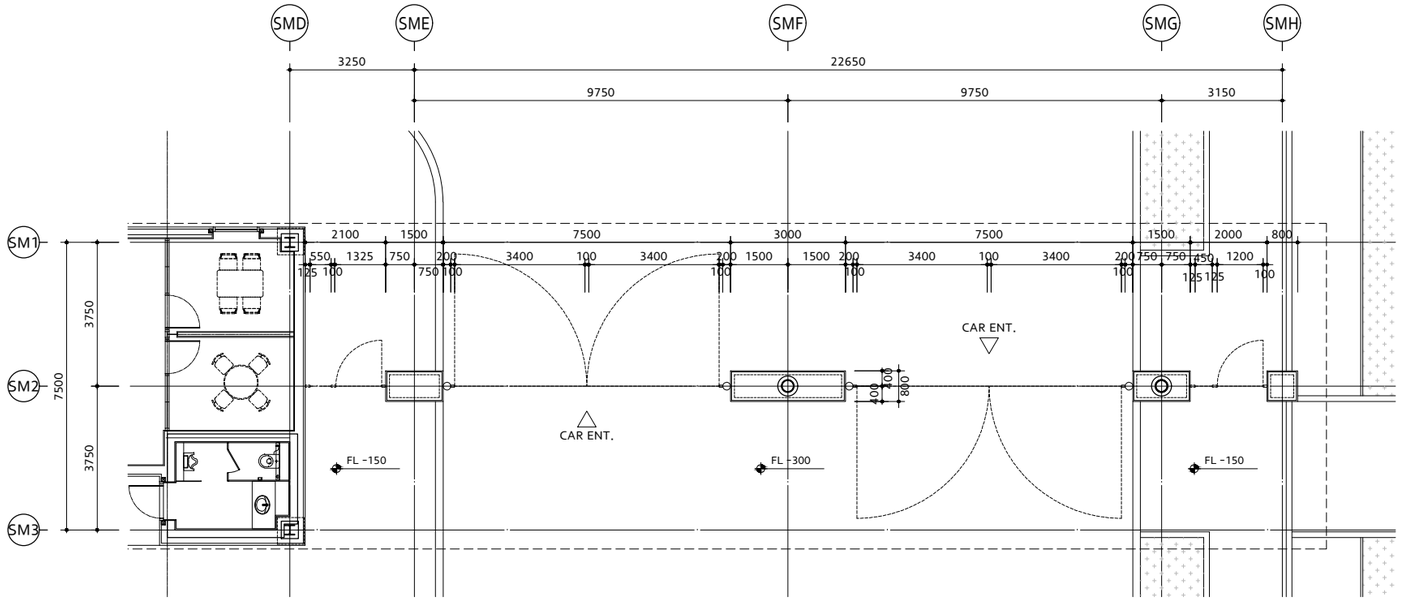


1 DOOR PLAN
SCALE : 1/80

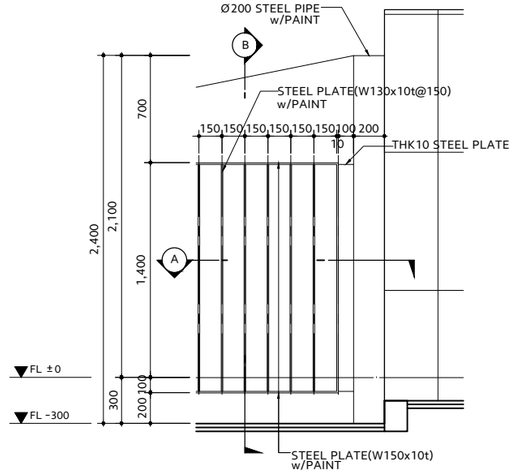


3 DETAIL-1
SCALE : NONE

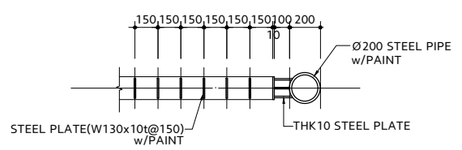


4 SECTION-A
SCALE : NONE

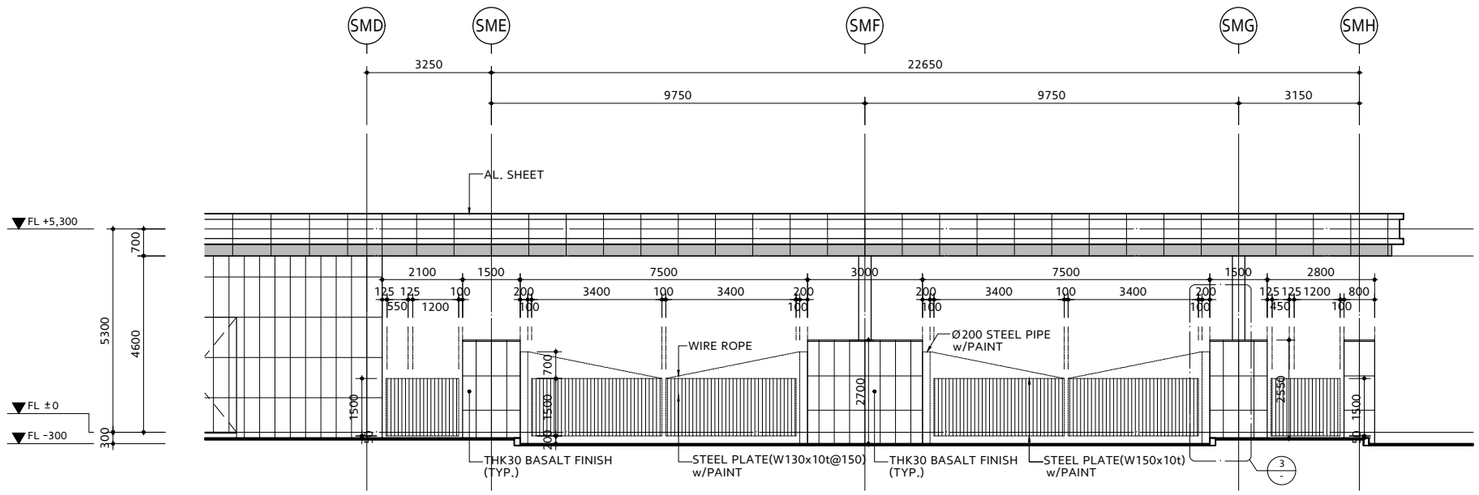

2 DOOR ELEVATION
SCALE : 1/80

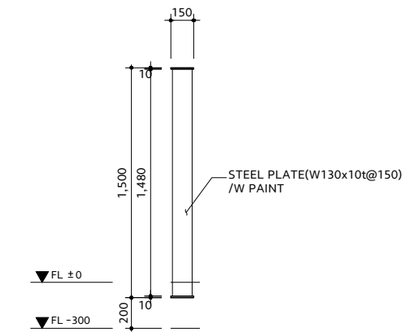

5 SECTION-B
SCALE : NONE

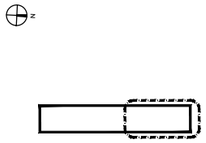

KEY PLAN

NOTE

1. GROUND FLOOR LEVEL
   -GROUND FLOOR FL ±0.00 = EL+659.50
2. LEVEL(T.O.C) OF GROUND FLOOR, WHICH IS THE BASE LEVEL OF ALL LEVEL DIMENSIONS.
3. THIS DRAWING SHOULD BE APPROVED BY HEC & HMI BEFORE APPLICATION
4. REFER TO DRAWING NUMBER "000-G-0001~0900" FOR GENERAL NOTES AND STANDARDS DETAIL.
5. SITE SURVEY FOR THIS DRAWING SHALL BE REQUIRED AND SUPERVISOR'S APPROVAL SHALL BE OBTAINED PRIOR TO CONSTRUCTION.
6. IF THE DRAWING IS DIFFERENT FROM CURRENT SITE, SUPERVISORS AND DESIGNER'S APPROVAL SHALL BE OBTAINED PRIOR TO CONSTRUCTION.
7. STRUCTURES IN THE BUILDING SHOULD BE ALKYD ENAMEL PAINT ON ANTI- RUST PAINT.
8. ALL SEALANT SHALL BE SUBMITTED TO THE MANUFACTURING ENGINEERING TEAM AND APPROVED PRIOR TO THE INSTALLATION BY THEM.

REV.	DESCRIPTION	DRAWN	DATE
0	CONSTRUCTION DRAWING	OH.J.S	2025. 02.14

CLIENT

HYUNDAI

ARCHITECTS & ENGINEERS

JUNGLIM ARCHITECTURE

PROJECT TITLE

PUNE HMI PROJECT

DRAWING TITLE

[MAIN SECURITY OFFICE] ENTRANCE DOOR DETAIL

SCALE	DRAWN	CHECKED	REVIEWED	APPROVED	APPROVED
A1: 1/80 A3:1/160	OH.J.S	HONG.G.D	LEE.S.L	HEC INDIA	PARK.T.S
DATE 14 FEB.2025					

MAIN CONTRACTOR

HEC INDIA LLP

DRAWING NO.	REV.
WA-IPB-645-A-7601	0

A1 SIZE (841mm x 594mm)