




VIEW V1-V1

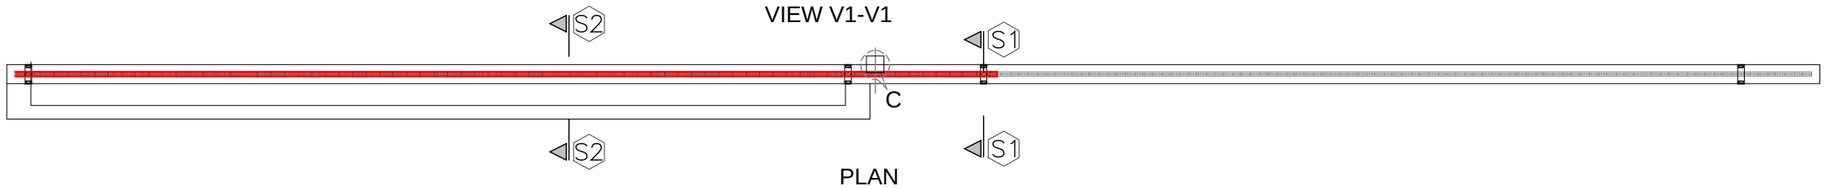


PLAN

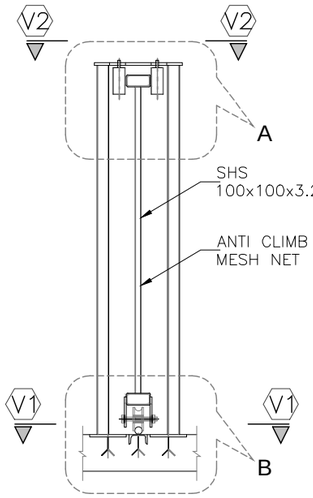

SECTION S1-S1

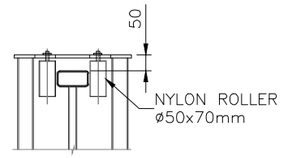


DETAILS AT A

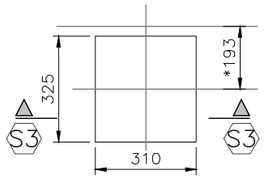


DETAILS AT C


*TO BE CONFIRMED WITH DRIVE MANUFACTURER

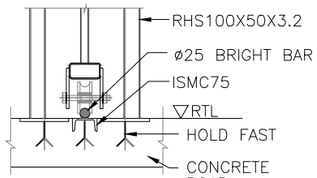

DETAILS AT B

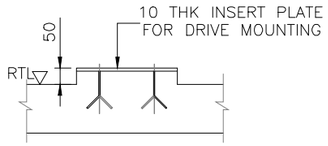

SECTION S3-S3

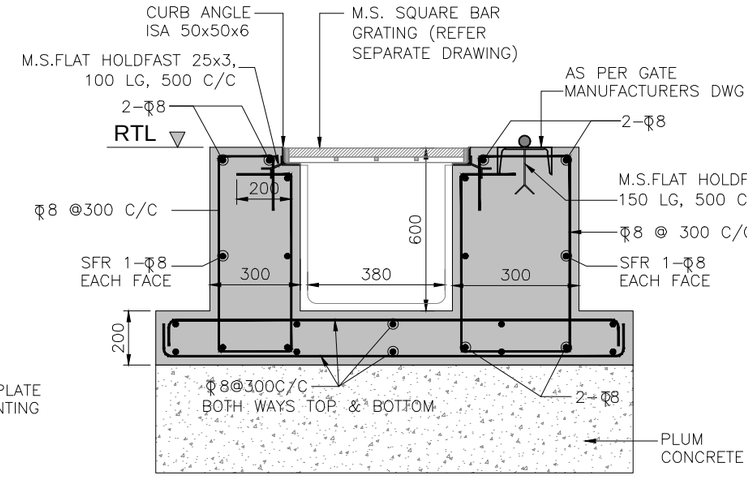


SECTION S2-S2

FOR TENDER


DATE : 07.06.2021

LEGENDS

FGL = FINISH GROUND LEVEL
SFR = SIDE FACE REINFORCEMENT
CP = COPING TOP
EJ = EXPANSION JOINT
I/S = INSIDE
O/S= OUTSIDE
FL= FOUNDING LEVEL

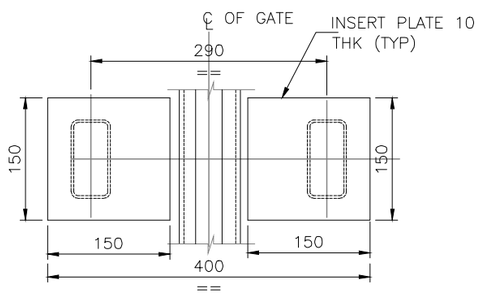

VIEW V1-V1

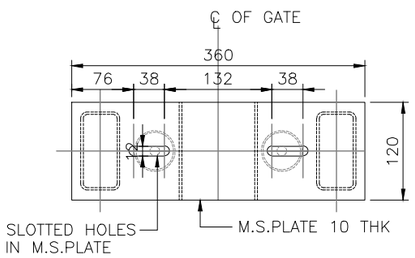

VIEW V2-V2

NOTES

1) ALL DIMENSIONS ARE IN mm AND LEVELS ARE IN METER.
2) DO NOT SCALE THE DRAWING.
3) READ THIS DRG IN CONJUNCTION WITH RELEVANT ARCH./STR. DRGS.
4) ANY DISCREPANCY/OMMISSION SHALL BE NOTIFIED TO US PRIOR TO EXECUTION.
5) READ GENERAL SPECIFICATION, GENERAL NOTES & CONTRACT SCHEDULE BEFORE EXECUTION.
6) CONCRETE GRADE M20 & STEEL GRADE Fe 500

THE FOUNDING LEVEL SHALL BE AT A DEPTH INDICATED IN THE DRAWING.
EXTRA EXCAVATION OVER THE DEPTH IF REQUIRED TO MEET THE SPECIFIED HARD STRATA
(SANDY SILTY GRAVEL) SHALL BE MADE UP BY PLUM CONCRETE AS PER SPECS.
(BLACK COTTON SOIL IF ANY SHALL BE REMOVED COMPLETELY)
(CONTRACTOR SHOULD GET THE LEVELS CHECKED FROM CONSULTANT PRIOR TO CONCRETING)

CLIENT : KSH INFRA PARK-IV PVT.LTD.	DRN. BY	NND	07.06.2021	REV
PROJECT : PROPOSED VARALE INDUSTRIAL & LOGISTICS PARK (PARK-A)	CHKD BY			R0
TITLE : DETAILS OF SLIDING COMPOUND GATE	APRD BY	NKY		

Associated Engineering Consultants.
313,'Siddhartha Towers'Building No.1,12/3B,Kothrud,Pune-29,Tele.Fax-25453863/64

DRG NO. AEC/2102/210607/04

SHEET 1 / 1

DO NOT SCALE THE DRAWING.

IN CASE OF DOUBT, PLEASE ASK US.

CAD FILE NAME: