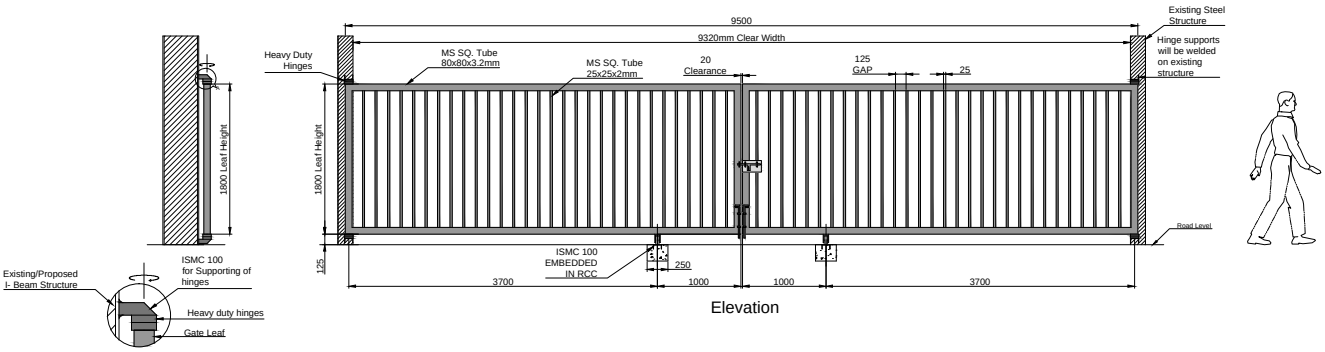
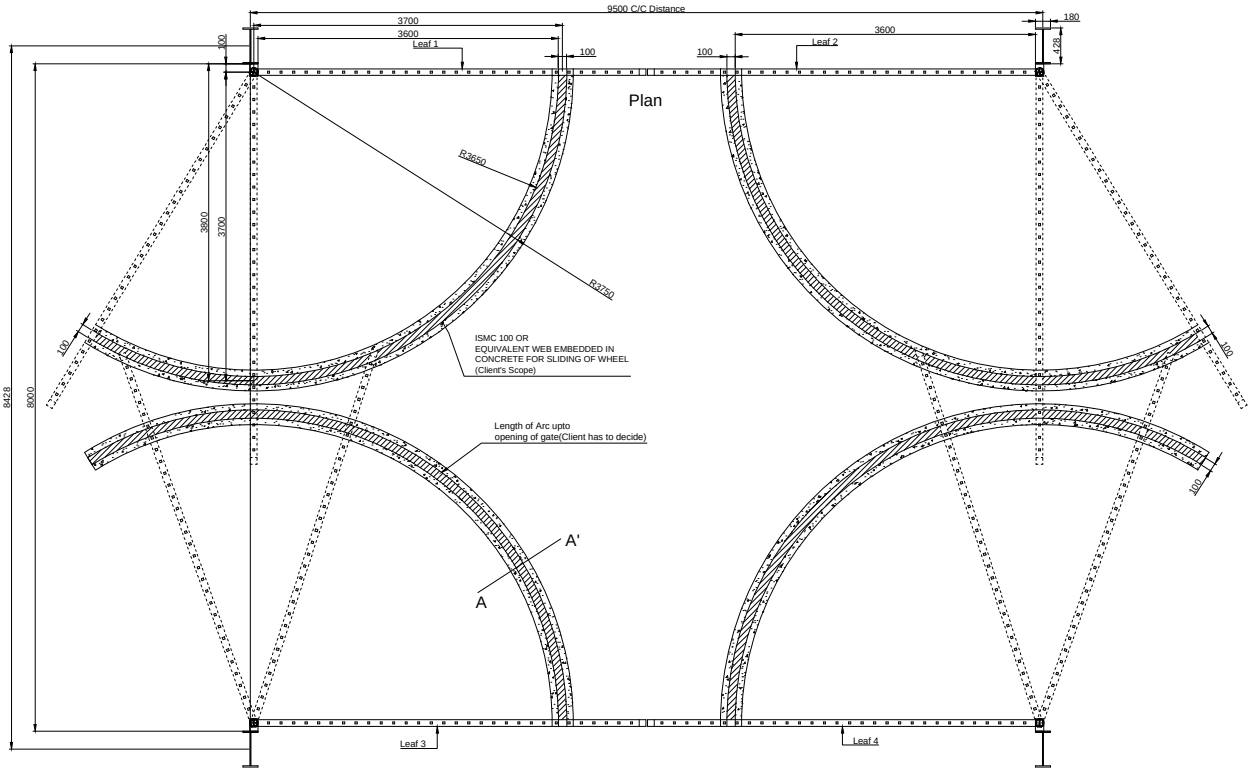
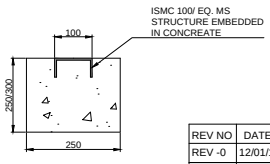



SECTION AA'

Color- 1. For Outer Boundry Golden Yellow RAL 1004
2. For Inner Tubes Marine blue RAL 5002

Color Shade are as per previously approved gates. Client has to confirm the same.

| REV NO | DATE | DESCRIPTION |
|---|---|---|
| REV -0 | 12/01/18 | INITIAL DRAWING |
| REV -1 | 15/02/18 | LOCKS,HINGES FIXING,TRACK DETAILS ADDED. |

NOTE-
1. ALL REQUIRED CIVIL WORK WILL BE IN CLIENTS SCOPE.
2. ONE COAT OF RED OXIDE & TWO COAT OF APPROVED RAL SHADE WILL BE GIVEN TO THE GATE.

| SR NO | TUBE SPECIFICATION | |
|---|---|---|
| 01 | MS 80X80X3.2mm | OUTER FRAME |
| 02 | MS 25X25X2mm | INNER PATTERN |

This drawing & design is the property of NIHVA TECHNOLOGIES. Not to be sold or copied to any other concern.

TITLE

Gate 1(Boom gate)

CLIENT APPROVAL

ALL DIMENSION ARE IN mm

NIHVA TECHNOLOGIES PVT. LTD.

NIHVA TECHNOLOGIES PVT. LTD. PUNE
Tel : 020 66304033
Email:- info@nihva.com
Website:- www.nihva.com

| | SIGN | DATE | |
|---|---|---|---|
| DRAWN | OMKAR | 12/01/18 | CLIENT - Tata Projects |
| CHECK | SHEKHAR | 12/01/18 | PROJECT - Alstom |
| REV. | | | SITE - Madhepura, Bihar |
| APPRD. | SHEKHAR | 12/01/18 | DWG. NO. -NIHVA/17-18/0335/R01 — Rev- 1 |
| MFG | | | SCALE: NTS — WT: — SHEET: 01 OF 01 |
| Ref. No. | | | If any queries contact : design@nihva.com |