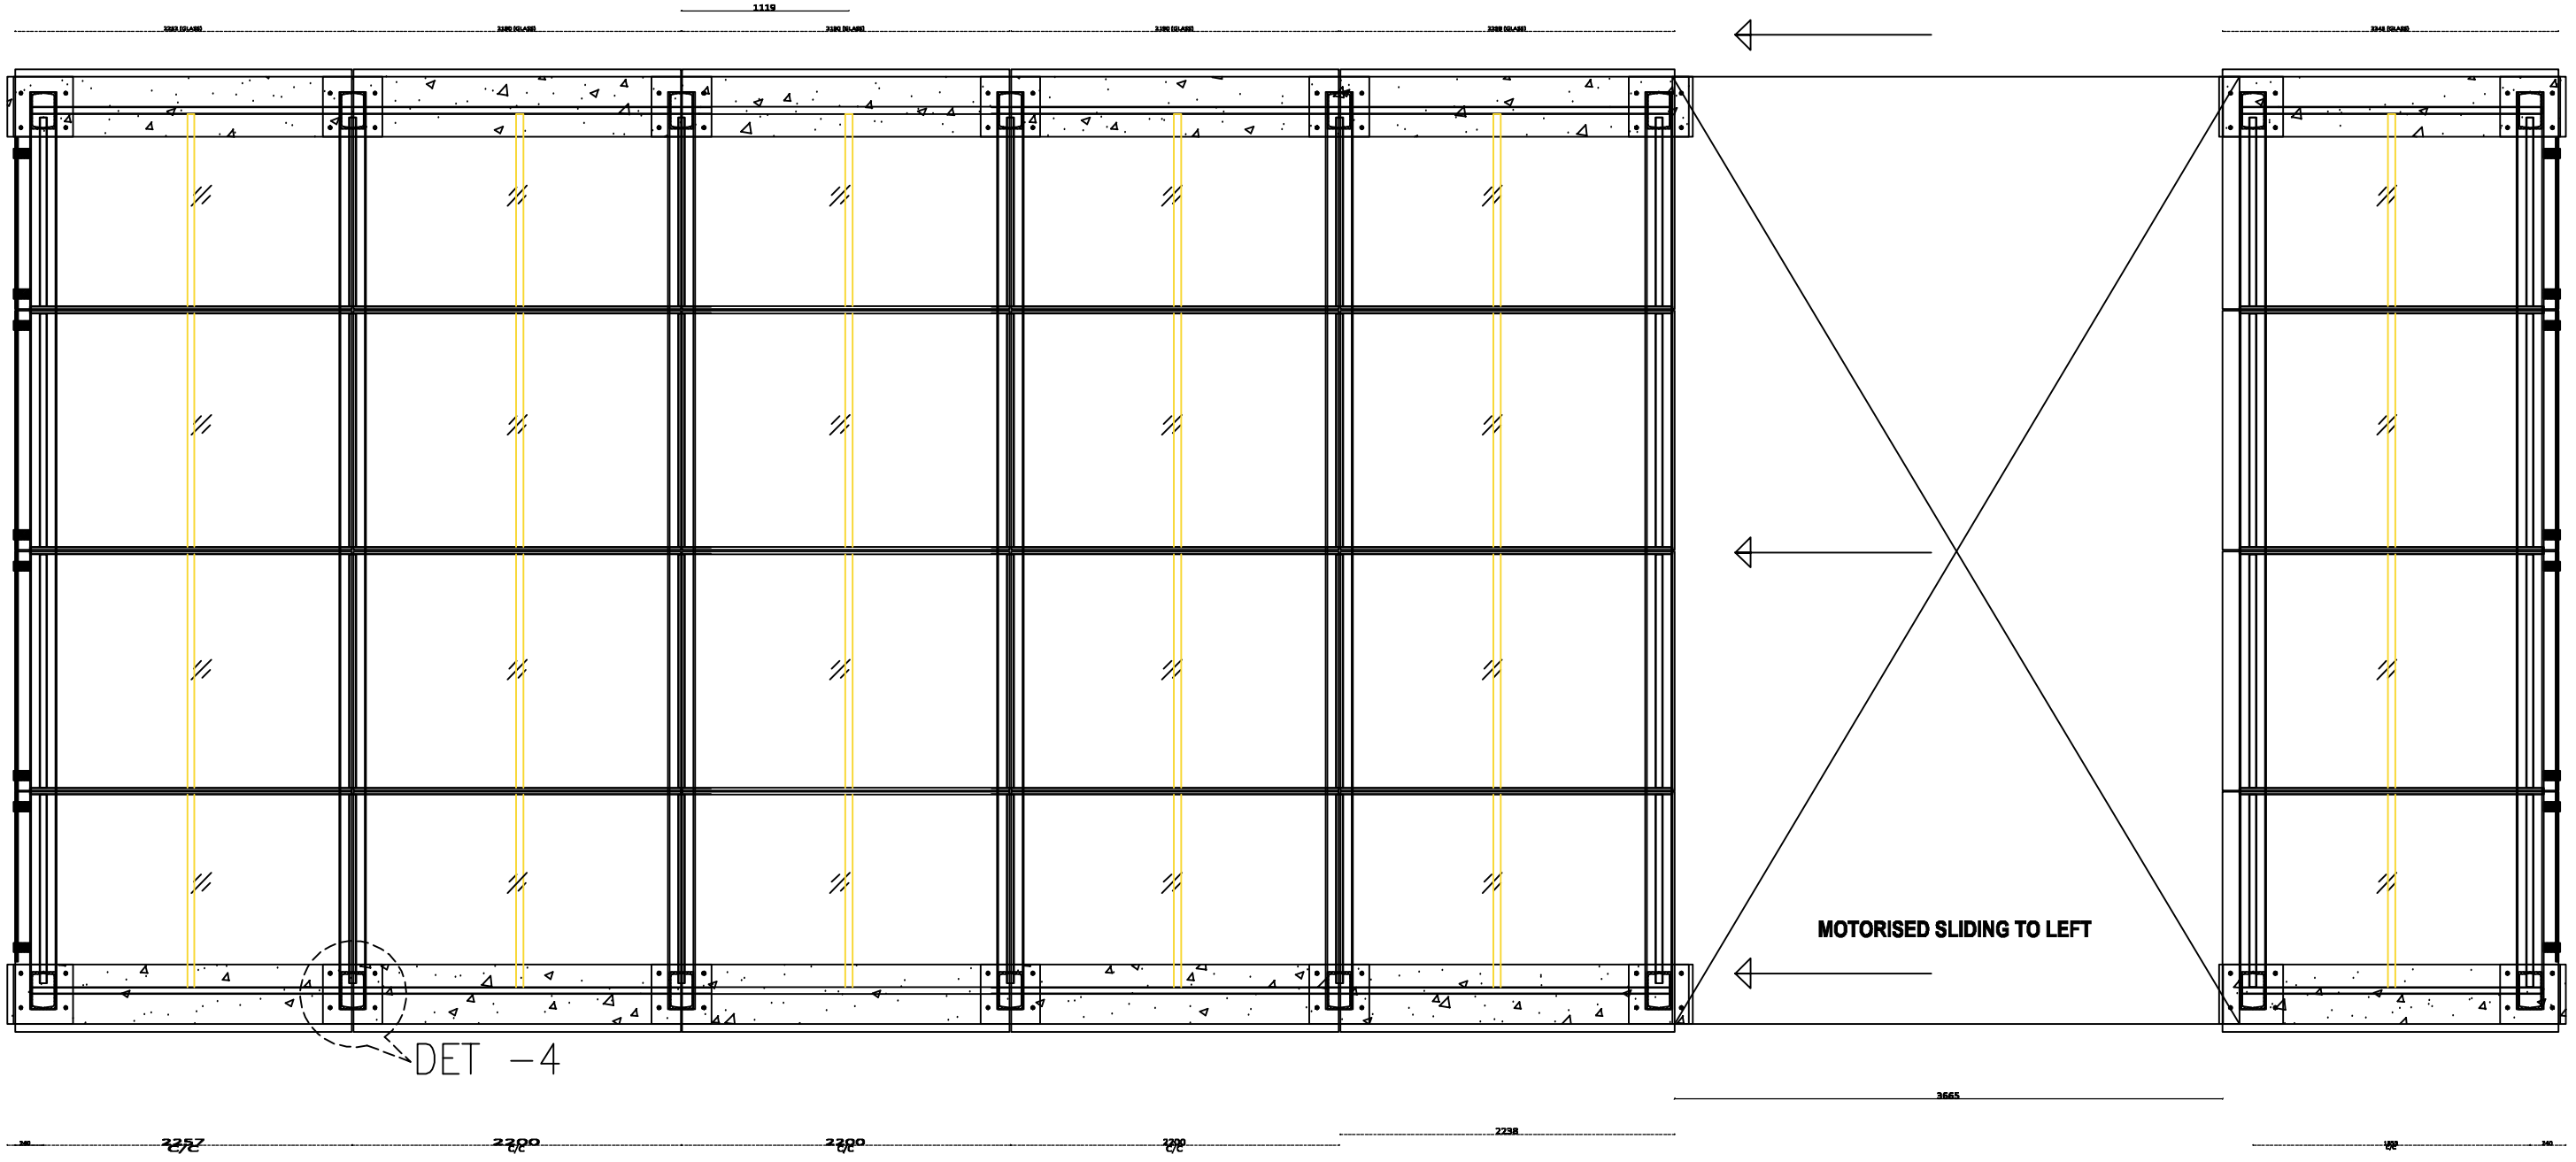



# TOP VIEW

| | | | | | |
|---|---|---|---|---|---|
| S NO : 19 | PROJECT : AM RESIDENCY | DRAWN BY : SUMAN | DRAWING NO : MFE-MEIL-09 | DATE: 09.06.21 | MATRIX FACADE ENGINEERING |
| | DRAWING TITTLE : TERRACE GLAZING GLAZING DETAILS | CHECKED BY : RAJESH LAHOTI | | SIGNATURE: | TEL : 04042307775/04042307776 E-mail : matrixacp@gmail.com |