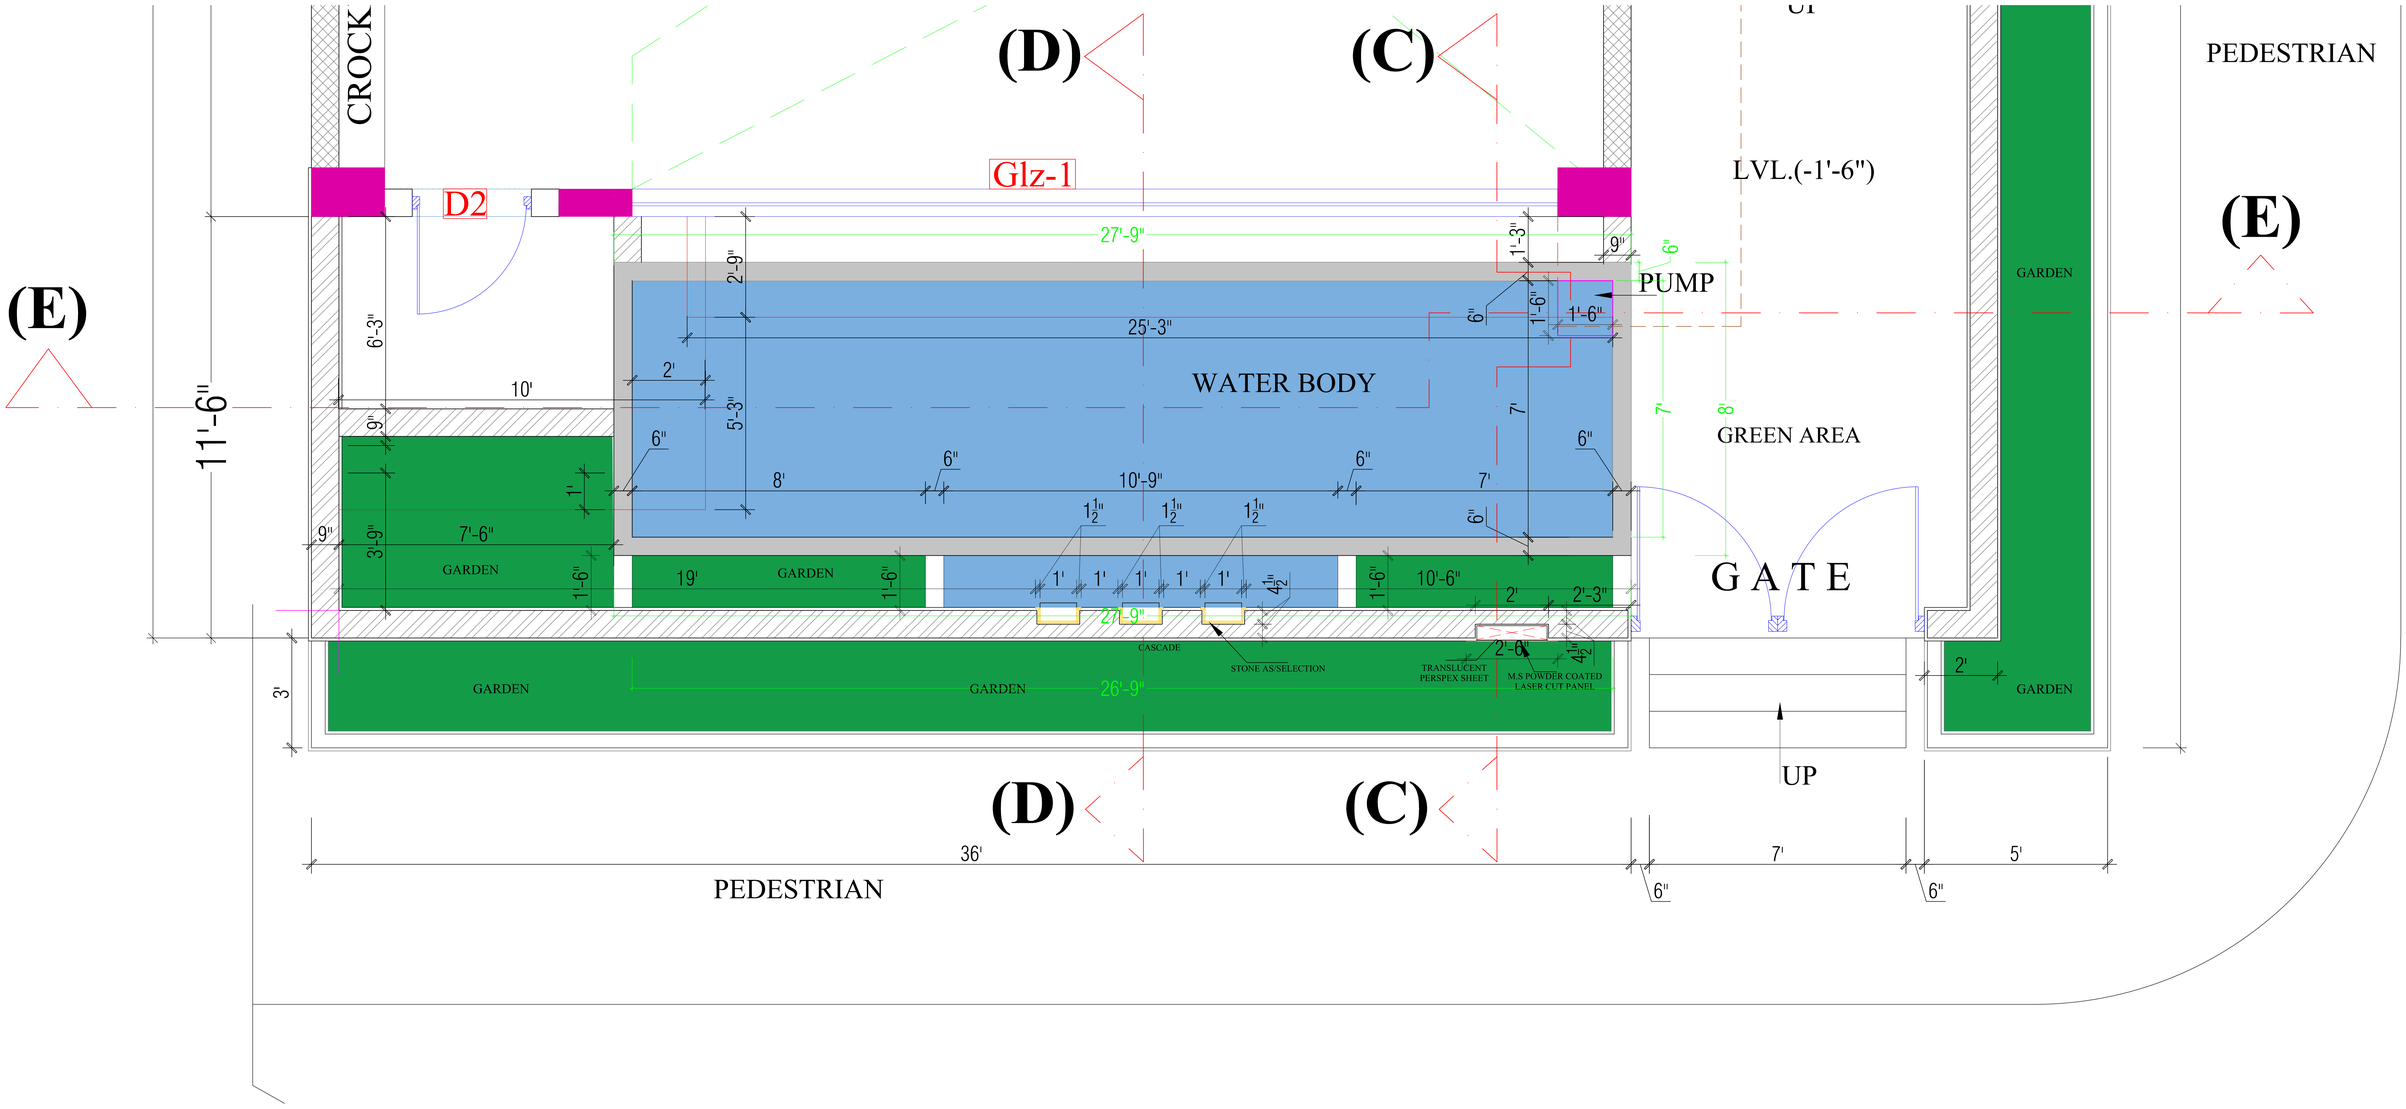

(E)
(D)
(C)
(E)
CROCK
D2
Glz-1
LVL.(-1'-6")
PEDESTRIAN
GARDEN
PUMP
WATER BODY
GREEN AREA
GATE
11'-6"
27'-9"
25'-3"
10'
2'
6'-3"
2'-9"
5'-3"
3'-9"
7'-6"
10'-9"
8'
19'
10'-6"
2'-3"
1'-3"
1'-6"
9"
6"
7'
1'
4½"
CASCADE
STONE AS SELECTION
TRANSLUCENT PERSPEX SHEET
M.S POWDER COATED LASER CUT PANEL
26'-9"
3'
UP
36'
7'
5'
PEDESTRIAN