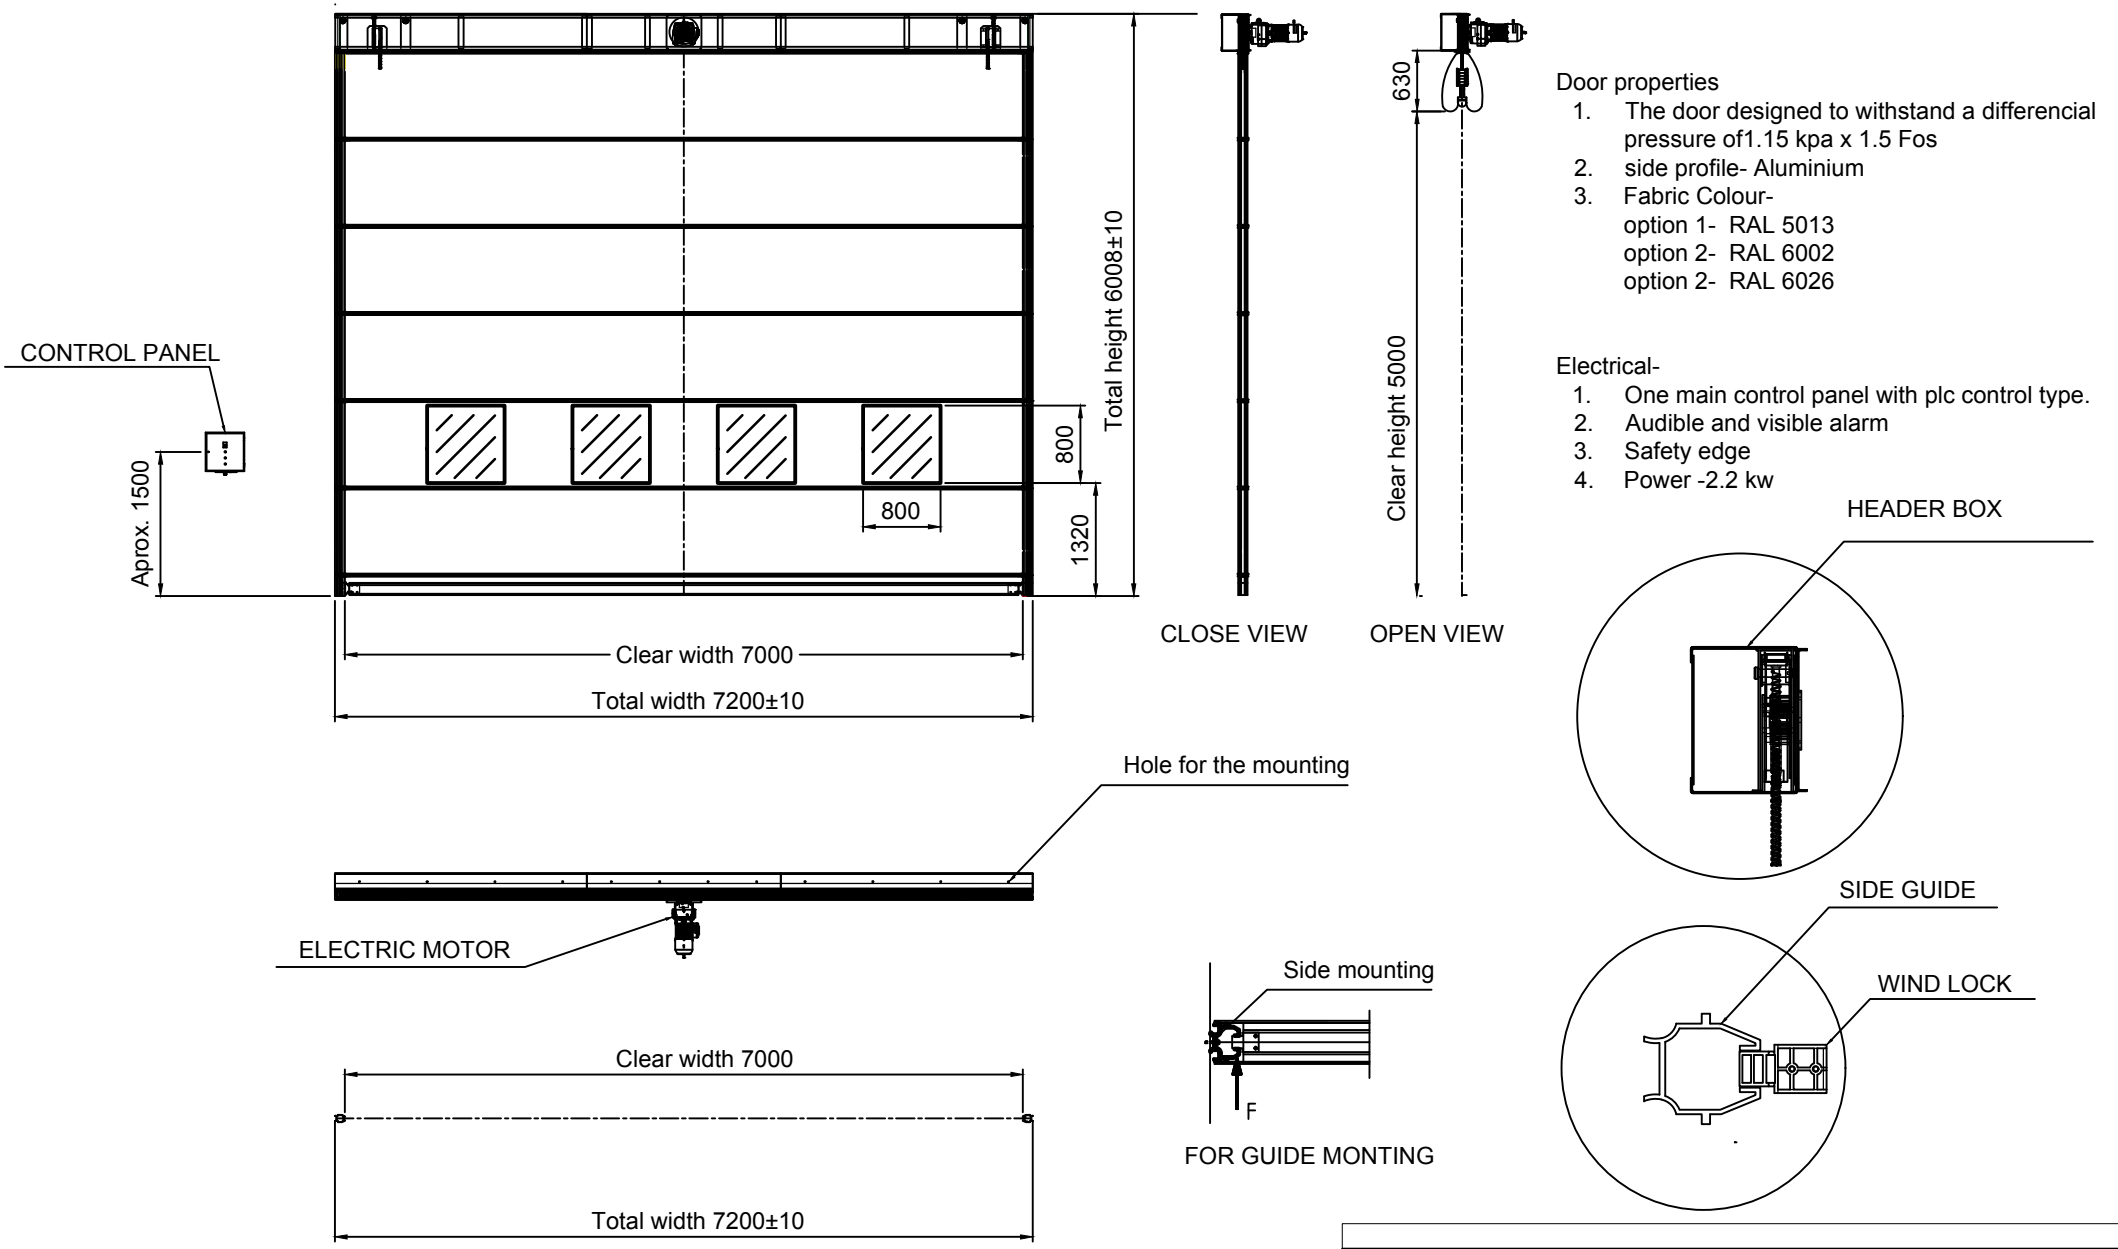


Door properties

1. The door designed to withstand a differencial pressure of1.15 kpa x 1.5 Fos
2. side profile- Aluminium
3. Fabric Colour-
   option 1- RAL 5013
   option 2- RAL 6002
   option 2- RAL 6026

Electrical-

1. One main control panel with plc control type.
2. Audible and visible alarm
3. Safety edge
4. Power -2.2 kw

Date	Revised By

TITLE:-
VERTICAL FABRIC DOOR

NIHVA TECHNOLOGIES PVT. LTD.

NIHVA TECHNOLOGIES PVT. LTD. PUNE
Tel : 020 66304033
Email:- info@nihva.com
Website:- www.nihva.com

	NAME	DATE	SIGN
DRAWN	KISHAN	19/05/2022	
CHECK	P. JAIN	19/05/2022	
APPRD.	V. TARAK	19/05/2022	

If any queries contact : design@nihva.com

ALL DIMENSION ARE IN mm

CLIENT - POSCO STEEL
LOCATION - MANGAON
PRODUCT - VERTICAL FABRIC DOOR
DWG NO:-NIHVA/22-23/CLT/0043 REV- 0
SCALE: NTS SCALE:-- 1:1 SHEET: 01 OF 01