

DWG.NO: SALT_1729_GA_01_R0

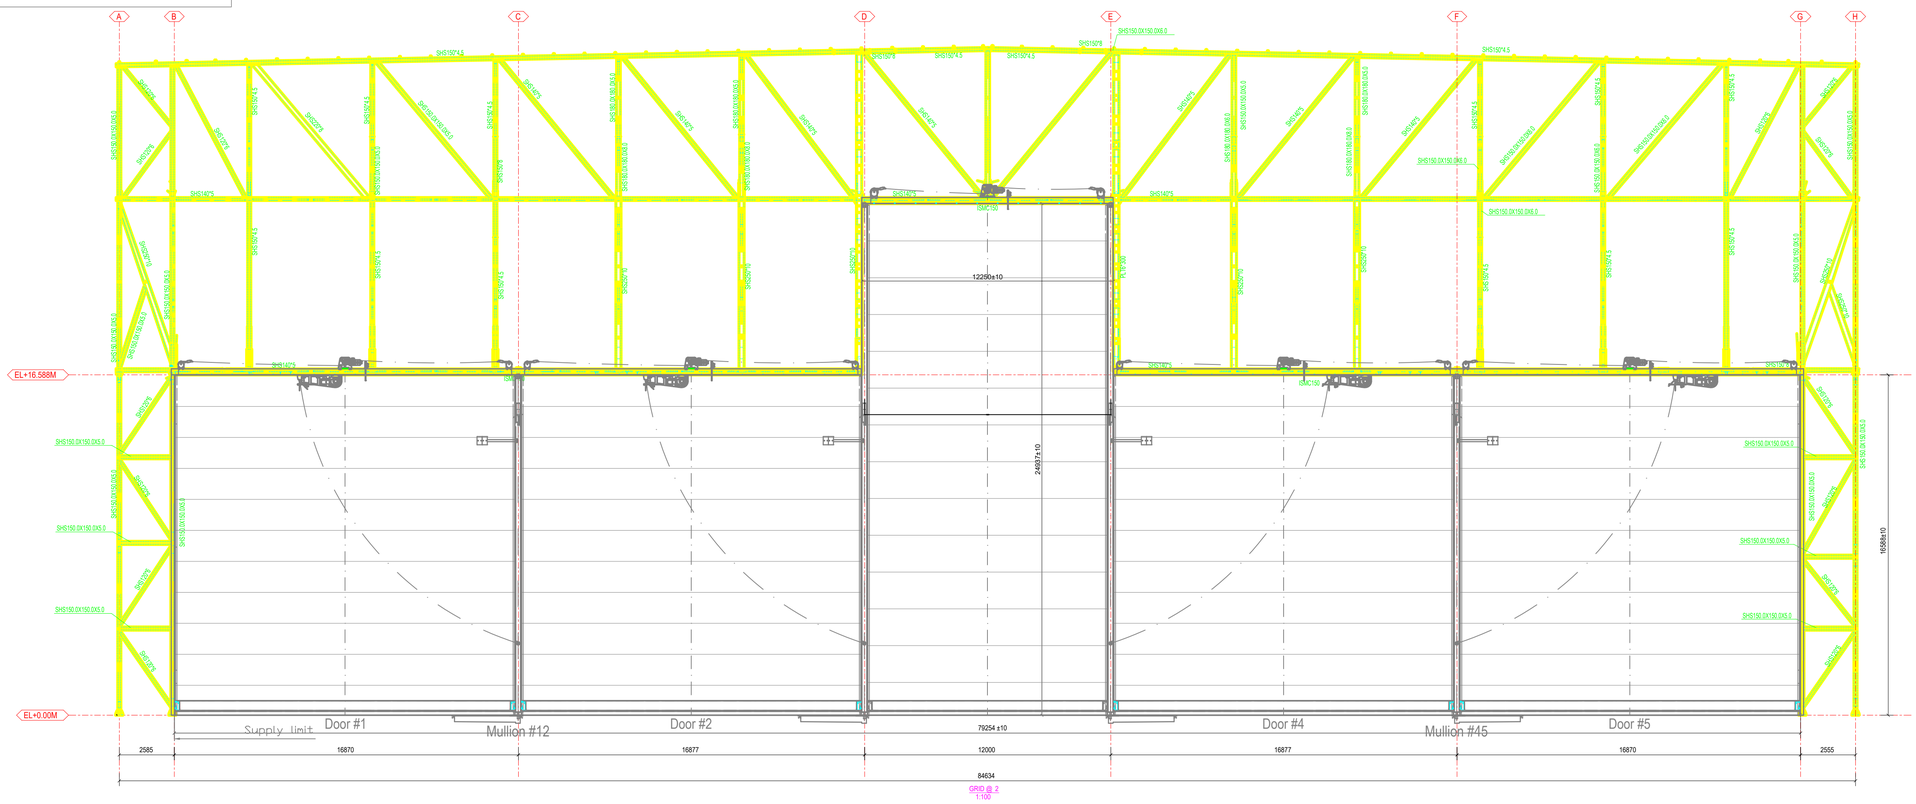

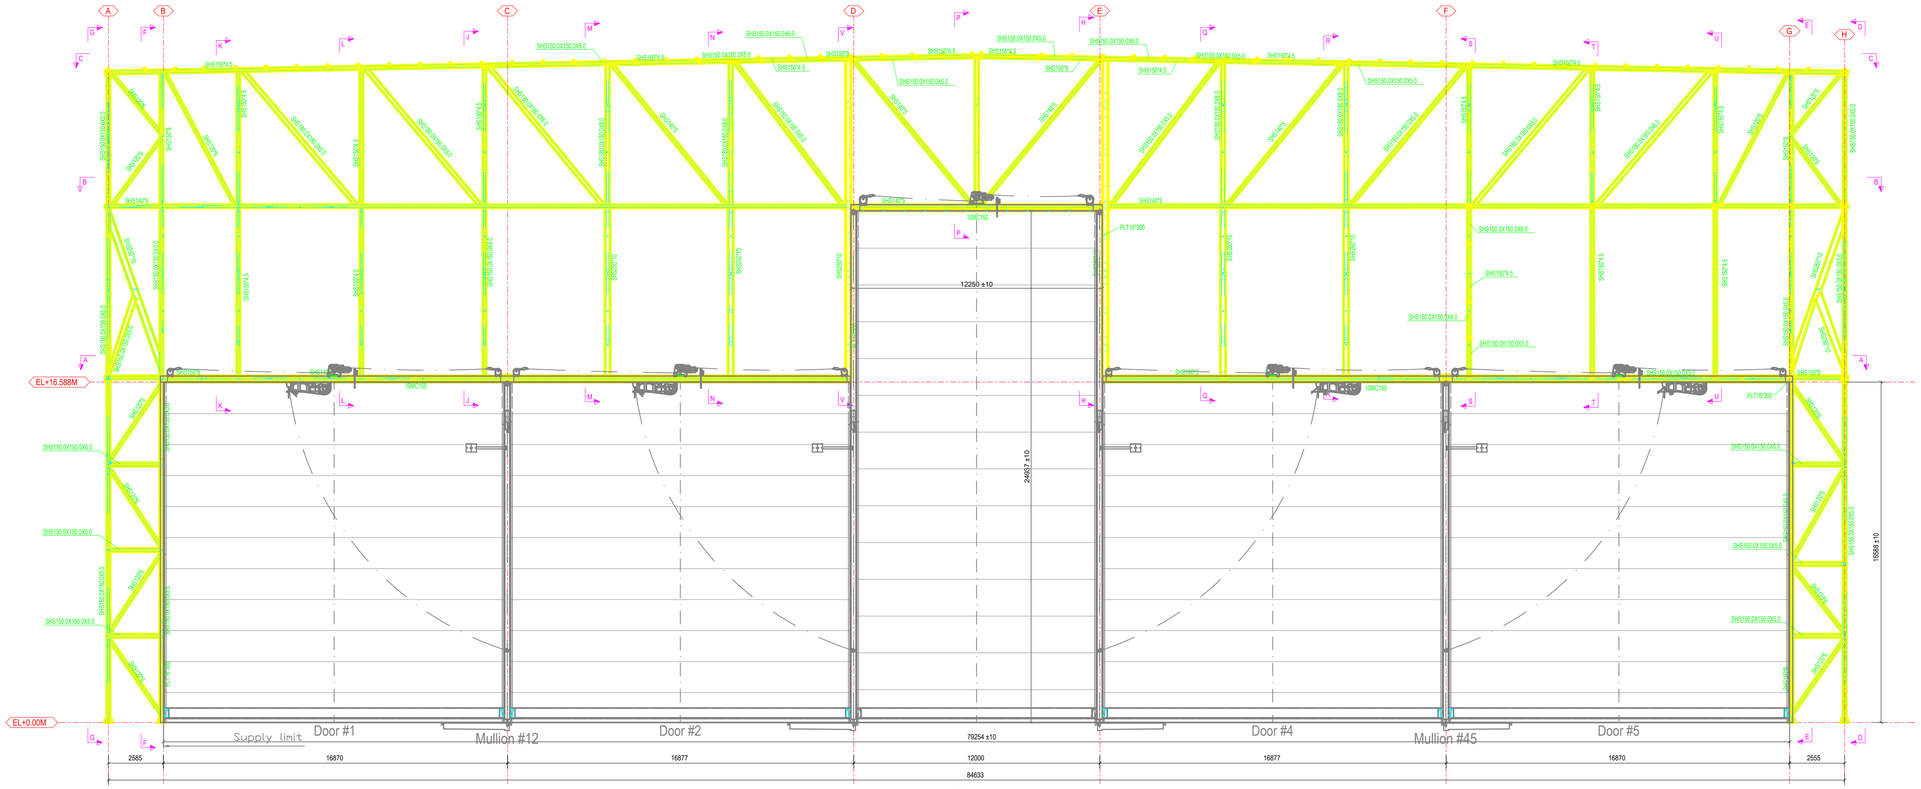

REV.NO.	DESCRIPTION.	REV.DATE	DRAWN.	CHKD.	APPD.
0	GA DRAWING FOR APPROVAL	05.11.22	RRK	HAB	HAB

DWG.TITLE :- GA DRAWING FOR DOOR FRAME(84M)

PROJECT	MEGADOOR INSTALLATION AT HYDRABAD AIRPORT
CLIENT	GMR

SALT Design Services
NIHVA TECHNOLOGIES PVT. LTD.

SALT DESIGN SERVICES
NIHVA TECHNOLOGIES PVT. LTD. PUNE
Tel : 020 66304033
Email:- info@nihva.com
Website:- www.nihva.com

DRAWN :RRK	CHECKED : HAB	SCALE: 1:100
APPROVED : HAB	JOB CODE. : 1729	DATE: 05.11.2022
DWG.NO: SALT_1729_GA_01_R0	(SH-1OF3)	REV. - R0 SIZE. - A0

A1 (841 x 594)