



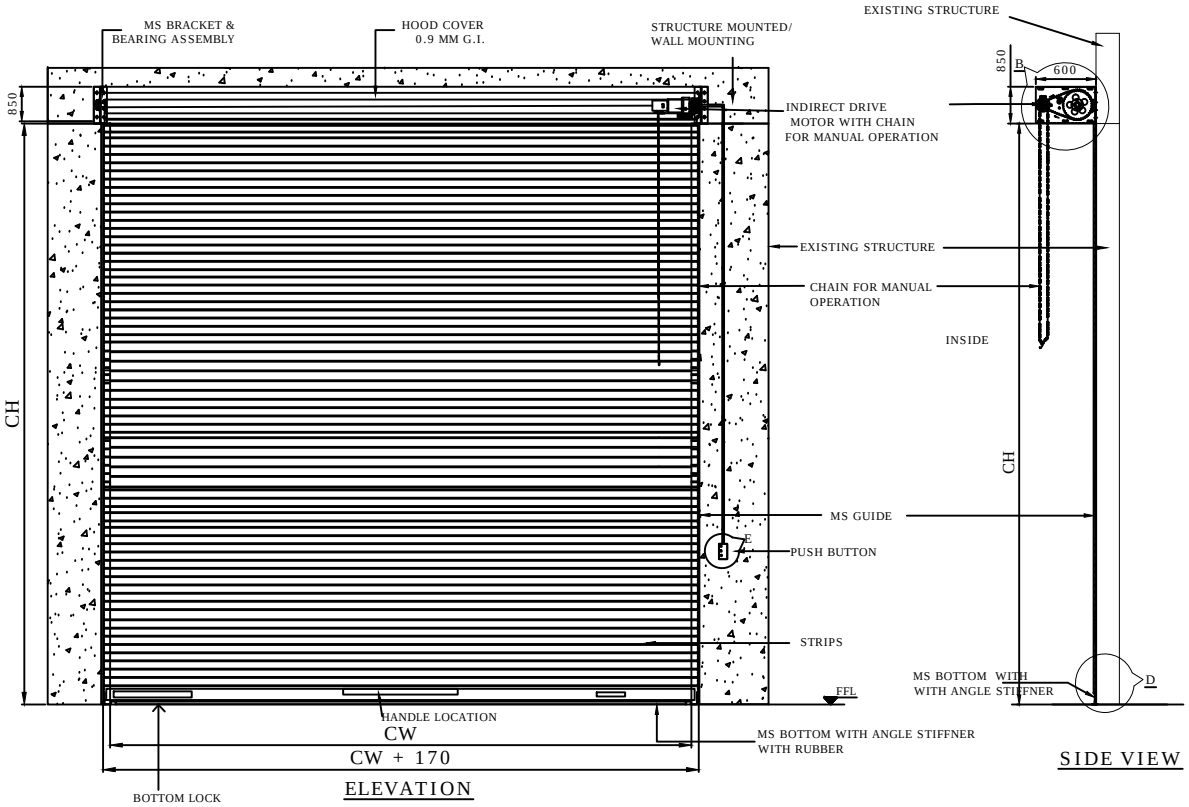


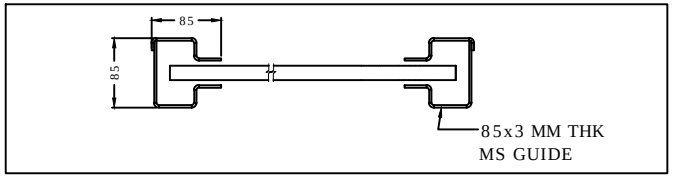

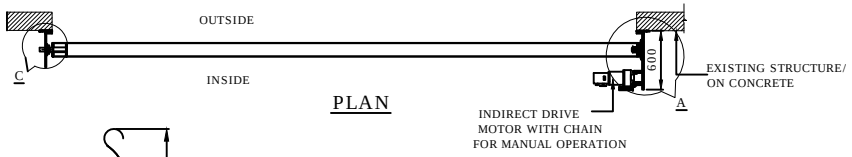


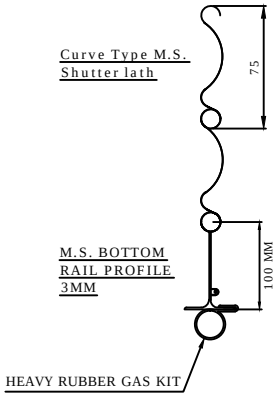

DETAILS : D

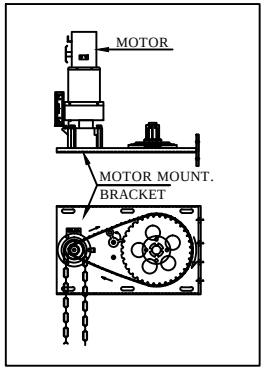

DETAILS : A & B

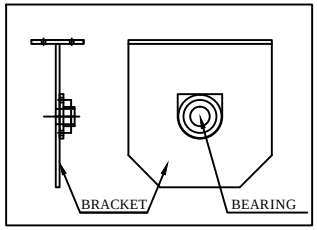

DETAILS : C

4500	4000	1	RAL 9002
CLEAR WIDTH (CW)	CLEAR HEIGHT (CH)	QUANTITY	RAL COLOR POWDER COATED

This drawing & design is the property of NIHVA TECHNOLOGIES. Not to be sold or copied to any other concern.

TITLE: MOTORIZED ROLLING SHUTTER

	NAME	SIGN	DATE
DRAWN	S.M.S.		26.10.2020
CHECK	K.P.		26.10.2020
APPRD.			

NIHVA TECHNOLOGIES PVT. LTD.
NIHVA TECHNOLOGIES PVT. LTD. PUNE
Tel : 020 66304033
Email:- info@nihva.com
Website:- www.nihva.com

CLIENT -

PROJECT -

SITE LOCATION - PUNE

If any queries contact : projectsupport@nihva.com

DWG. NO. : NIHVA/20-21/VDR/0076 REV- R00

ALL DIMENSION ARE IN mm | SCALE: NTS | WT: | SHEET: