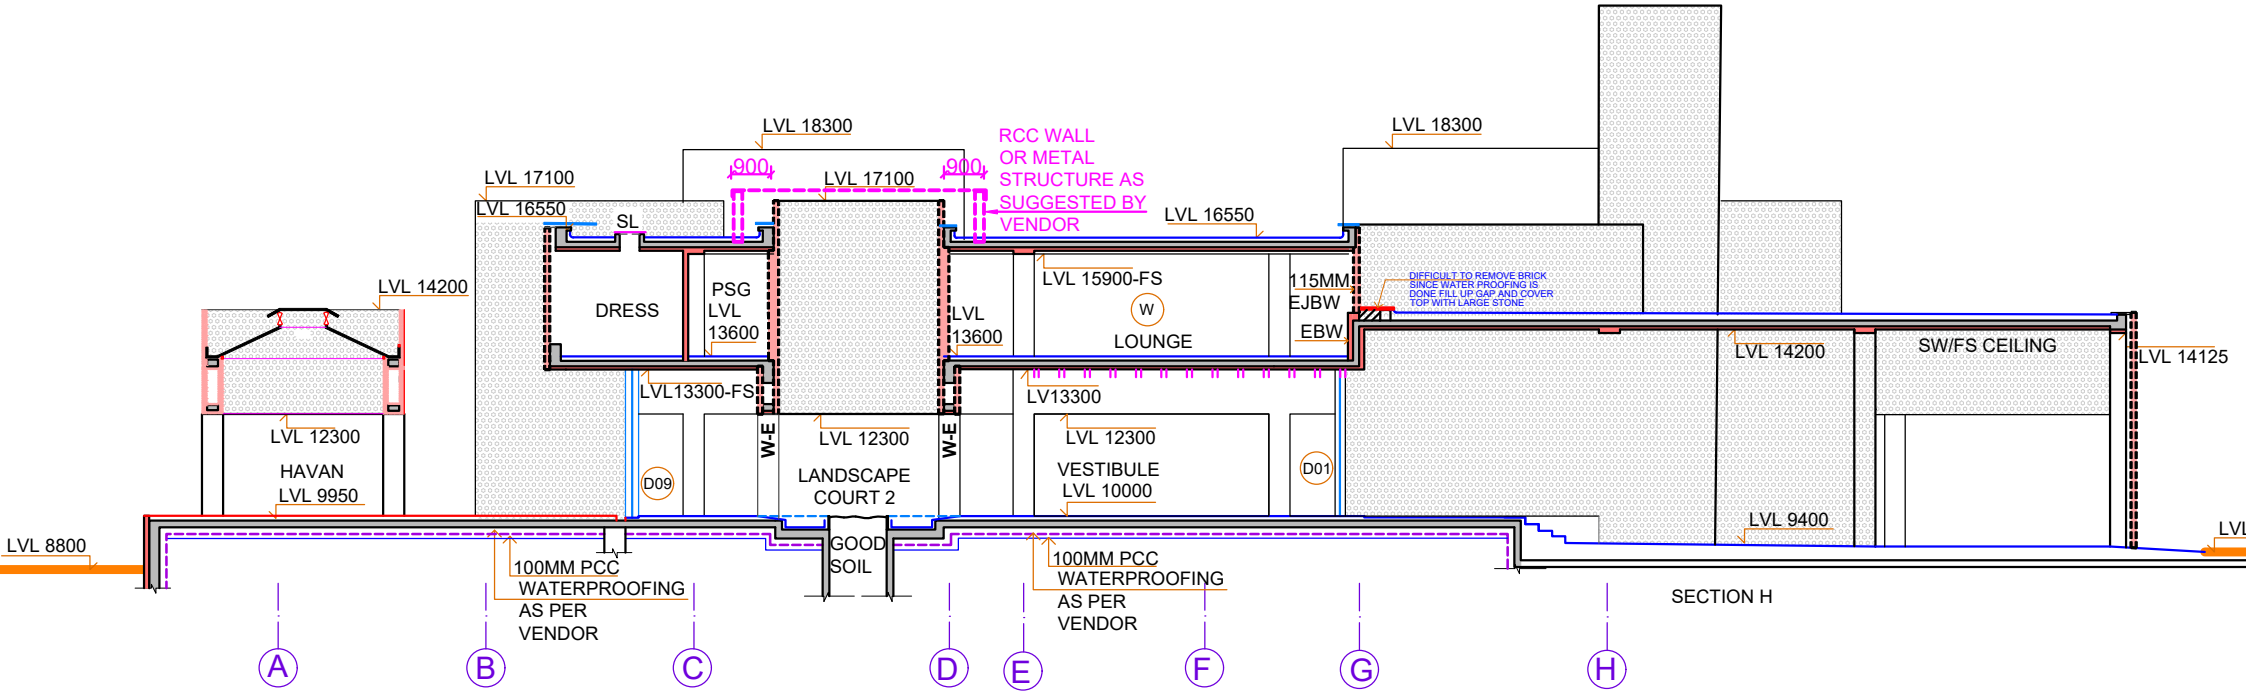

LVL 18300
RCC WALL
OR METAL
STRUCTURE AS
SUGGESTED BY
VENDOR
900
900
LVL 17100
LVL 17100
LVL 16550
SL
LVL 16550
LVL 18300
LVL 14200
DRESS
PSG
LVL
13600
LVL
13600
LVL 15900-FS
W
LOUNGE
115MM
EJBW
EBW
DIFFICULT TO REMOVE BRICK
SINCE WATER PROOFING IS
DONE FILL UP GAP AND COVER
TOP WITH LARGE STONE
LVL 14200
SW/FS CEILING
LVL 14125
LVL13300-FS
LV13300
LVL 12300
HAVAN
LVL 9950
D09
W-E
LVL 12300
LANDSCAPE
COURT 2
W-E
LVL 12300
VESTIBULE
LVL 10000
D01
LVL 9400
LVL 8800
GOOD
SOIL
100MM PCC
WATERPROOFING
AS PER
VENDOR
100MM PCC
WATERPROOFING
AS PER
VENDOR
SECTION H
A
B
C
D
E
F
G
H