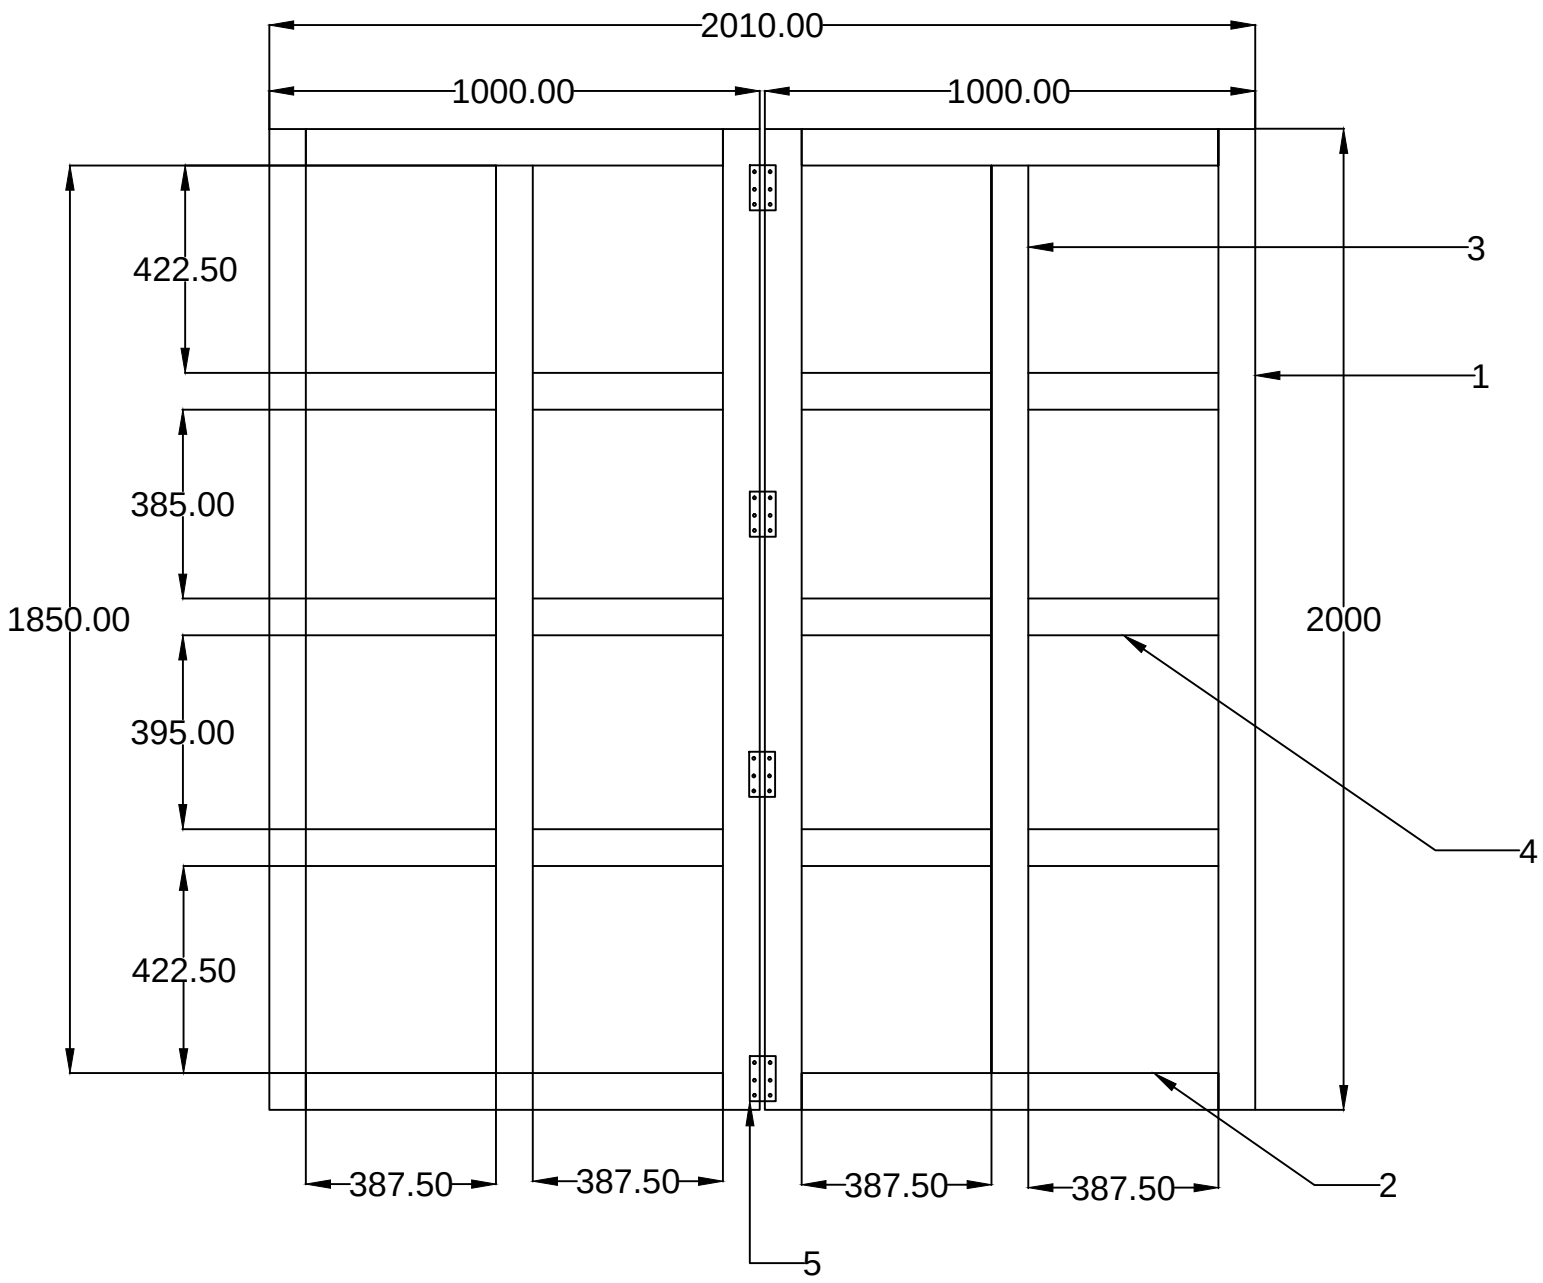

SR. NO.	DESCRIPTION	SPECIFICATION	QTY
1	SQ. TUBE	75 X 75 X 3.2, 2000 LENGTH	4 NOS
2	SQ. TUBE	75 X 75 X 3.2, 850 LENGTH	4 NOS
3	SQ. TUBE	75 X 75 X 3.2, 1850 LENGTH	2 NOS
4	SQ. TUBE	75 X 75 X 3.2, 387.5 LENGTH	12 NOS
5	DOOR SUPPORTING HINGES	4" HEAVY DUTY HINGES	8 NOS
6	NYLON WHEEL	4" NYLON WHEEL	2 NOS

This drawing & design is the property of NIHVA TECHNOLOGIES. Not to be sold or copied to any other concern.

TITLE
BIFOLD DECK FRAME

NIHVA TECHNOLOGIES PVT. LTD.

NIHVA TECHNOLOGIES PVT. LTD. PUNE
Tel : 020 66304033
Email:- info@nihva.com
Website:- www.nihva.com

	NAME	SIGN	DATE
DRAWN	G.P.		31.12.21
CHECK	A.K.		31.12.21
APPRD.	V.T.		31.12.21

If any queries contact : design@nihva.com

ALL DIMENSION ARE IN mm

CLIENT - NIHVA TECHNOLOGIES
LOCATION - DELHI
PRODUCT - BIFOLD DECK
NIHVA\21-22\MFG\012 REV- 00
SCALE: NTS SHEET: 01 OF 01