




SIDE VIEW

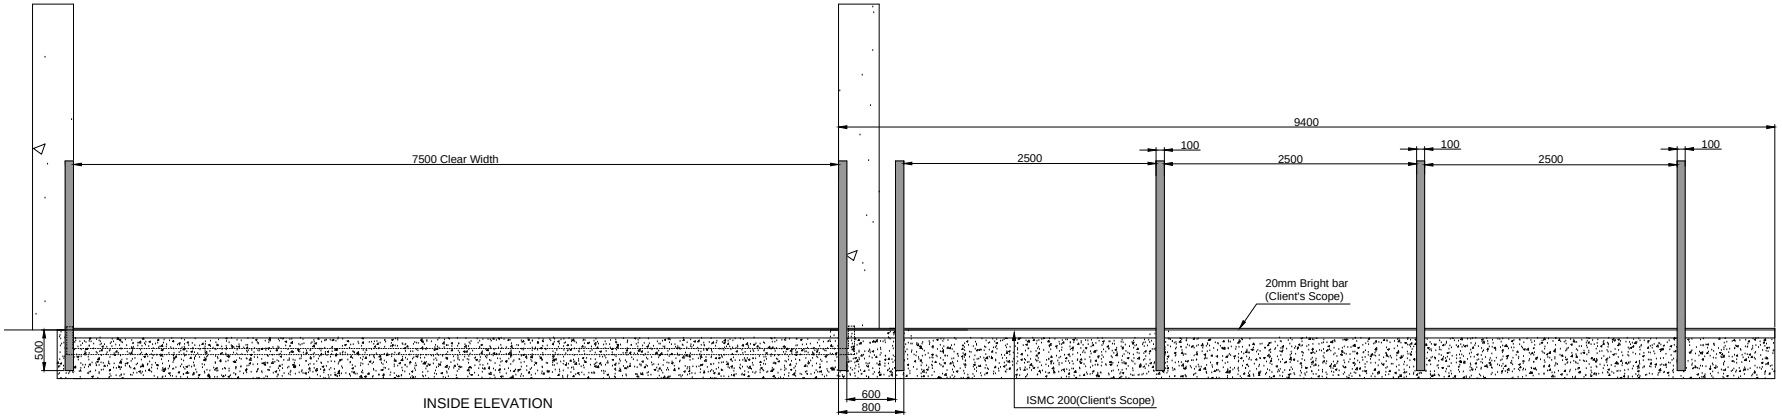

INSIDE ELEVATION

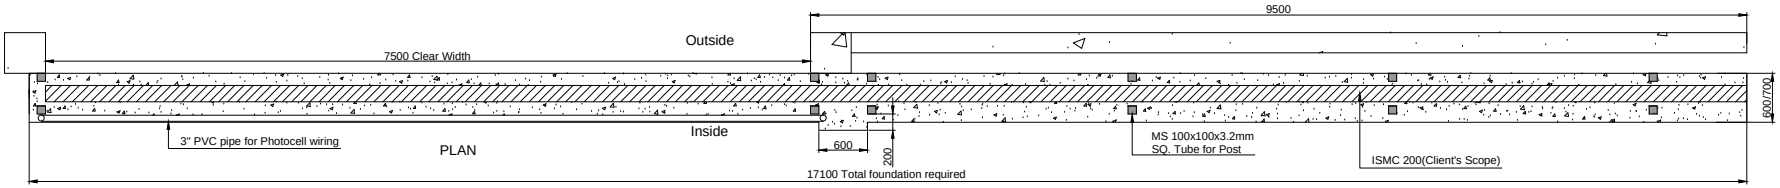

PLAN

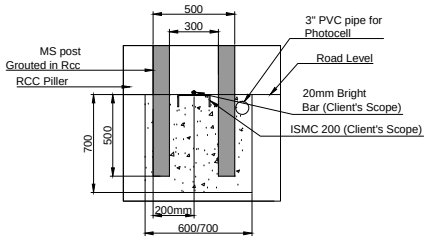

Detailed View of A

REV NO	DATE	DESCRIPTION
REV -0	10/01/18	INITIAL DRAWING
REV -1	13/01/18	Clear width revised from 9400 to 7500mm.

CLEAR WIDTH	CLEAR HEIGHT	QUANTITY
7500mm	1800mm	1 NOS

This drawing & designing is the property of NIHVA TECHNOLOGIES. Not to be sold or copied to any other concern.

TITLE
Foundation of Motorised Sliding gate 7.5x1.8m

	SIGN	DATE
DRAWN	Omkar	10/01/18
CHECK	Shekhar	10/01/18
APPROVAL	Shekhar	10/01/18

If any queries contact : design@nihva.com

ALL DIMENSION ARE IN mm

NIHVA
NIHVA TECHNOLOGIES PVT. LTD.
NIHVA TECHNOLOGIES PVT. LTD. PUNE
Tel : 020 66304033
Email:- info@nihva.com
Website:- www.nihva.com

CLIENT - Zamil Construction India Pvt. Ltd.

PROJECT - Kapci

SITE LOCATION - Banglore

DWG. NO. : NIHVA/17-18/0333/R01 | Rev- 1

SCALE: NTS | WT: | SHEET: 01 OF 01