
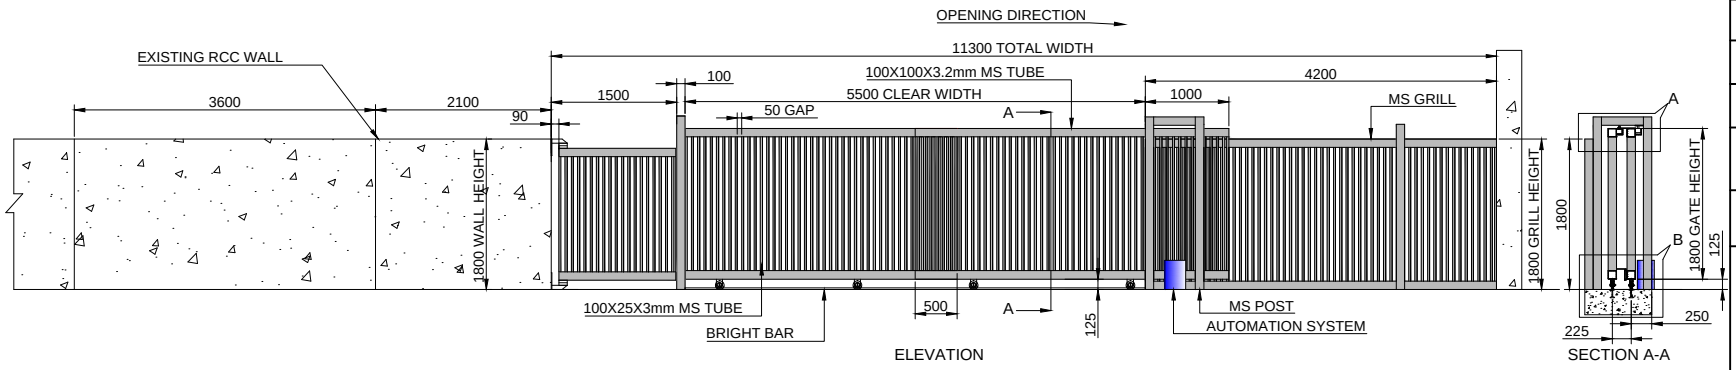
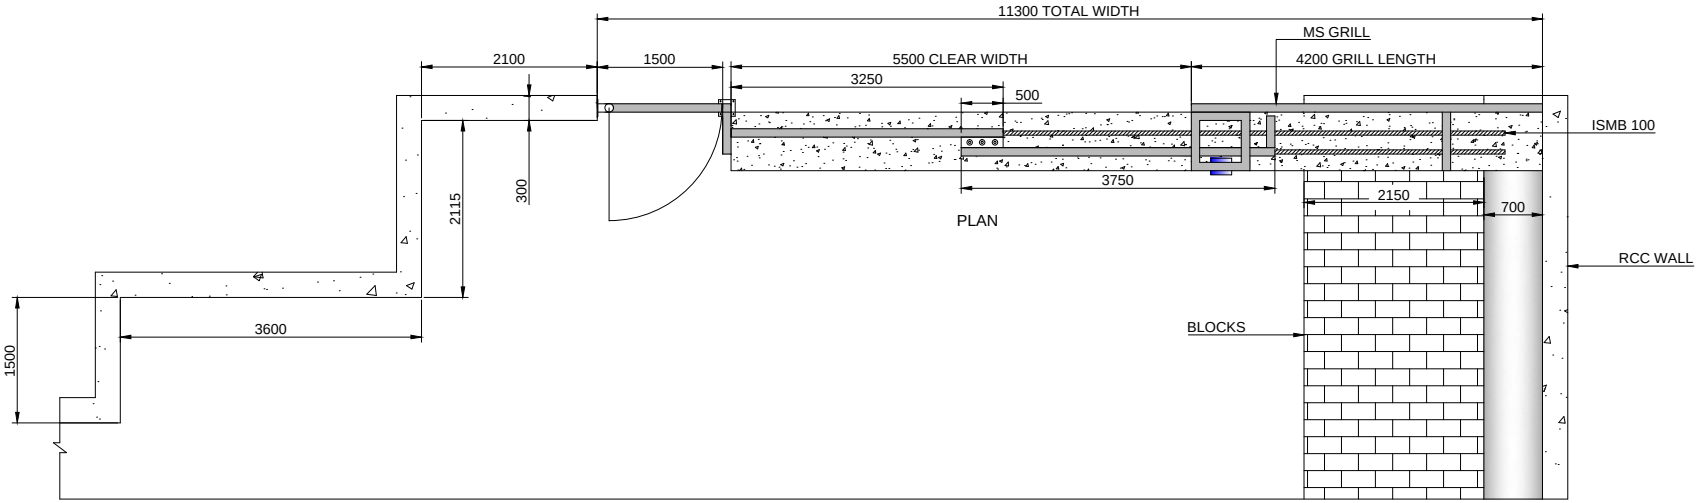
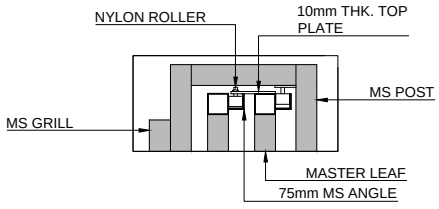



DETAILED VIEW OF A

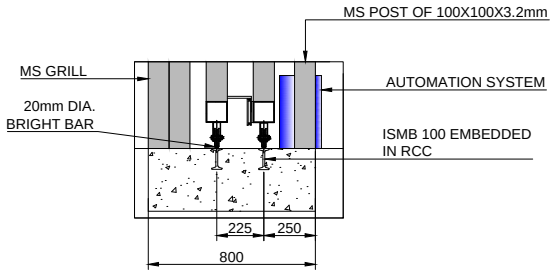


DETAILED VIEW OF B

DIMENSION :

| CLEAR WIDTH | CLEAR HEIGHT | QUANTITY |
|---|---|---|
| 5500 mm | 1800 mm | 01 NOS. |
| 1500 mm | 1800 mm | 01 NOS. |

MATERIAL :

THICKNESS :

NIHVA TECHNOLOGIES PVT. LTD.

NIHVA TECHNOLOGY PVT. LTD. PUNE
Email:- info@nihva.com
Website:- www.nihva.com

TITLE:

# TWO LEAF TELESCOPIC GATE & WICKET GATE

CLIENT'S APPROVAL :

CLIENT - LUPIN LIMITED

PROJECT -

SITE LOCATION - SUS ROAD,PUNE

DWG. NO. : NIHVA/16-17/110

| SCALE: NTS | WT: | SHEET:1 OF 1 |
|---|---|---|

| DRAWN BY: OMKAR | DATE: 05-12-2016 |
|---|---|
| CHECK : SAGAR P. | DATE: 05-12-2016 |

If any queries contact : projects@nihva.com

NOTE: ALL DIMENSION ARE IN mm

THIS DRAWING & DESIGNING IS THE PROPERTY OF NIHVA TECHNOLOGIES. NOT BE SOLD OR COPY TO ANY OTHER CONCERN.