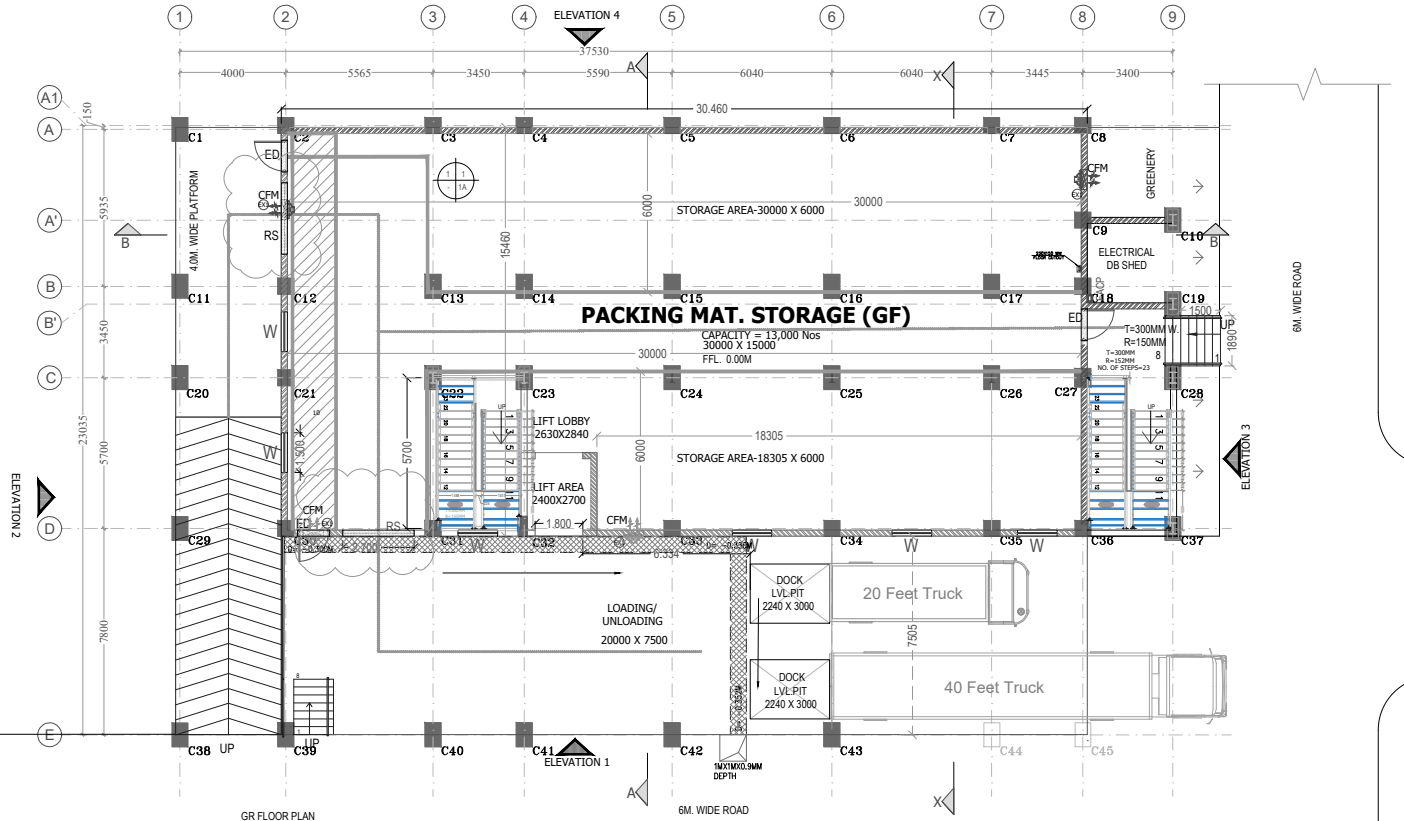


NON FIRE RATED BUILDING

DOOR & WINDOW SCHEDULE

S.NO.	SYMBOL	TYP.	SIZE	DESCRIPTION	SILL	LINTEL	QTY
1		RS	2700 X 3500	FIRE RATED MOTORIZED ROLLING SHUTTER	000	3500	2
2	D	D	1200 X 2100	FIRE RATED SINGLE SHUTTER HMPS (Hollow Metal Pressed Steel..) WITH VISION PANEL	000	2100	0
3	ED	ED	1200 X 2100	FIRE RATED EMERGENCY DOOR WITH VISION PANEL & PANIC BAR	000	2100	4
4		W	1500 X 1200	NON FIRE RATED WINDOWS	900	2100	11
5		EX1	1000 X 1000	EXHAUST CUT OUT 1000 X 1000MM ON WALL FROM BEAM BOTTOM	900	2100	11

2HRS FIRE RATED WALL

NON FIRE RATED WALL

FINISHING SCHEDULE

SR.NO.	DESCRIPTION
EW	EXTERNAL WALL
1	230MM. THK 2HRS FIRE RATED WALL
IW	INTERNAL WALL
1	230MM THK BRICK WALL WITH 12MM THK INTERNAL PLASTER WITH OBD
2	VITRIFIED TILE DADO 1.8 @ WASH AREA & 2.1H. @ PANTRY
3	75 MM.THK PARTITION
C/R	CEILING / ROOFING
1	RCC SLAB, 12MM THK INTERNAL PLASTER WITH OBD
2	ALUMINIUM METAL GRID FALSE CEILING IN OFFICE AREA , LAB AREA & PANTRY
3	
4	
F	FLOORING
1	TRIMIX SLAB WITH EPOXY FLOORING FINISH / TILE
1A	IPS FLOORING FINISH
2	600 X 600 MM VITRIFIED FLOORING AS PER SPECS
3	ANTI SKID VITRIFIED TILES
4	KOTA STONE FLOORING