| Revision | | Date | By | Appr. |
|---|---|---|---|---|
| A | Clear Height was 47500. Measures, ballons and information added | 2022-01-14 | FV | |

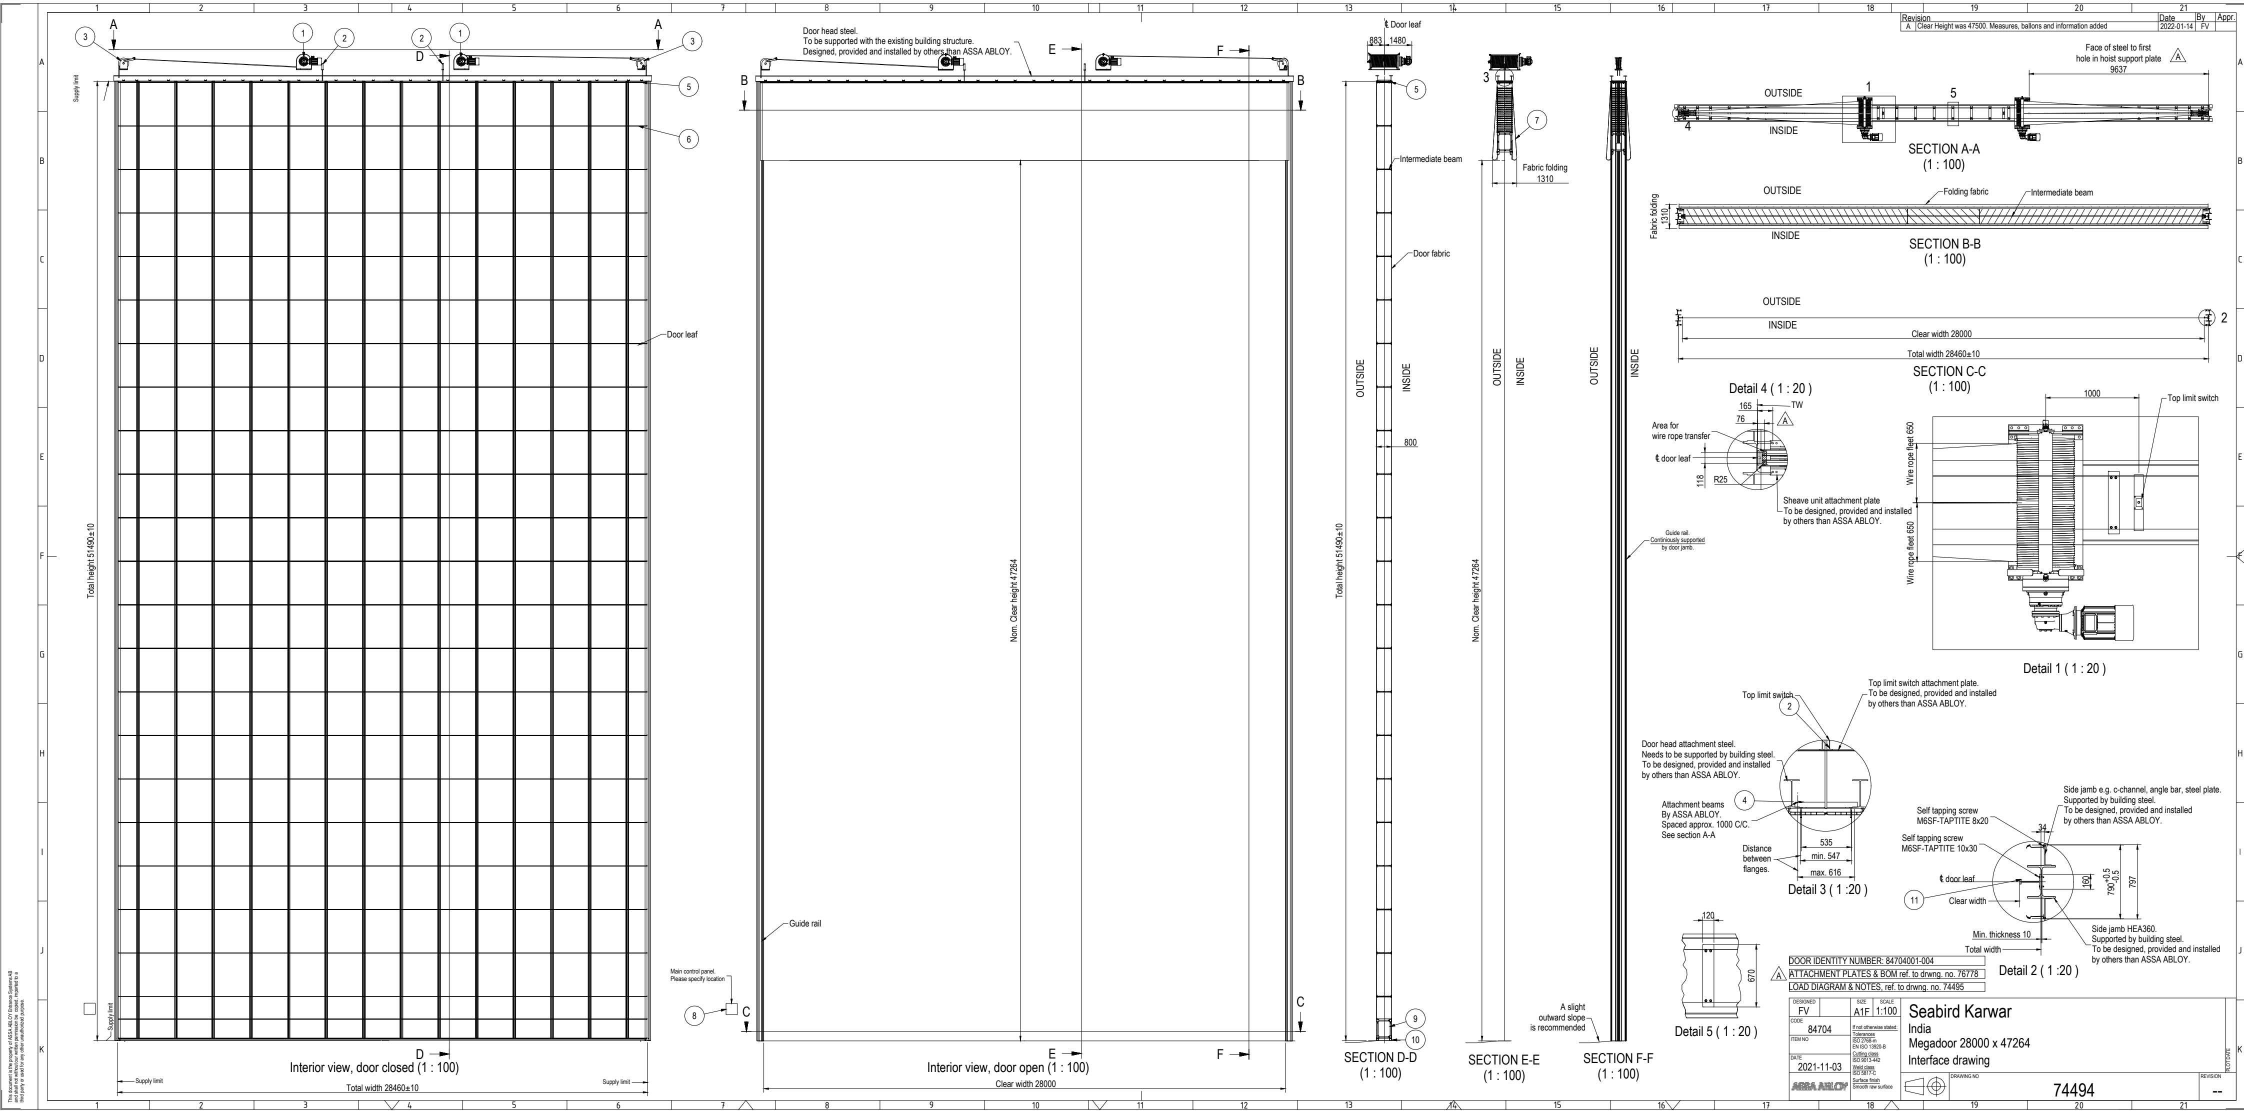
A
1
2
3
D
Supply limit
Total height 51490±10
5
6
Door leaf
Interior view, door closed (1 : 100)
Total width 28460±10
Door head steel.
To be supported with the existing building structure.
Designed, provided and installed by others than ASSA ABLOY.
E
F
B
Nom. Clear height 47264
Guide rail
Main control panel.
Please specify location
8
C
Interior view, door open (1 : 100)
Clear width 28000
℄ Door leaf
883
1480
Intermediate beam
Door fabric
OUTSIDE
INSIDE
800
9
10
SECTION D-D
(1 : 100)
7
Fabric folding
1310
SECTION E-E
(1 : 100)
Guide rail.
Continiously supported
by door jamb.
A slight
outward slope
is recommended
SECTION F-F
(1 : 100)
Face of steel to first
hole in hoist support plate
9637
4
SECTION A-A
(1 : 100)
Folding fabric
Fabric folding
SECTION B-B
(1 : 100)
Clear width 28000
Total width 28460±10
SECTION C-C
(1 : 100)
Detail 4 ( 1 : 20 )
165
76
TW
Area for
wire rope transfer
℄ door leaf
118
R25
Sheave unit attachment plate
To be designed, provided and installed
by others than ASSA ABLOY.
1000
Top limit switch
Wire rope fleet 650
Wire rope fleet 650
Detail 1 ( 1 : 20 )
Top limit switch
Top limit switch attachment plate.
To be designed, provided and installed
by others than ASSA ABLOY.
Door head attachment steel.
Needs to be supported by building steel.
To be designed, provided and installed
by others than ASSA ABLOY.
Attachment beams
By ASSA ABLOY.
Spaced approx. 1000 C/C.
See section A-A
Distance
between
flanges.
535
min. 547
max. 616
Detail 3 ( 1 :20 )
Side jamb e.g. c-channel, angle bar, steel plate.
Supported by building steel.
To be designed, provided and installed
by others than ASSA ABLOY.
Self tapping screw
M6SF-TAPTITE 8x20
Self tapping screw
M6SF-TAPTITE 10x30
34
160
790+0.5-0.5
797
11
Clear width
Min. thickness 10
Total width
Side jamb HEA360.
Supported by building steel.
To be designed, provided and installed
by others than ASSA ABLOY.
Detail 2 ( 1 :20 )
120
670
Detail 5 ( 1 : 20 )

DOOR IDENTITY NUMBER: 84704001-004

A ATTACHMENT PLATES & BOM ref. to drwng. no. 76778

LOAD DIAGRAM & NOTES, ref. to drwng. no. 74495

| DESIGNED | SIZE | SCALE |
|---|---|---|
| FV | A1F | 1:100 |

CODE 84704

ITEM NO

DATE 2021-11-03

If not otherwise stated:
Tolerances
ISO 2768-m
EN ISO 13920-B
Cutting class
ISO 9013-442
Weld class
ISO 5817-C
Surface finish
Smooth raw surface

ASSA ABLOY

# Seabird Karwar
India
Megadoor 28000 x 47264
Interface drawing

DRAWING NO 74494

REVISION --

PLOT DATE

This document is the property of ASSA ABLOY Entrance Systems AB and shall not without our written permission be copied, imparted to a third party or used for any other unauthorized purpose.