




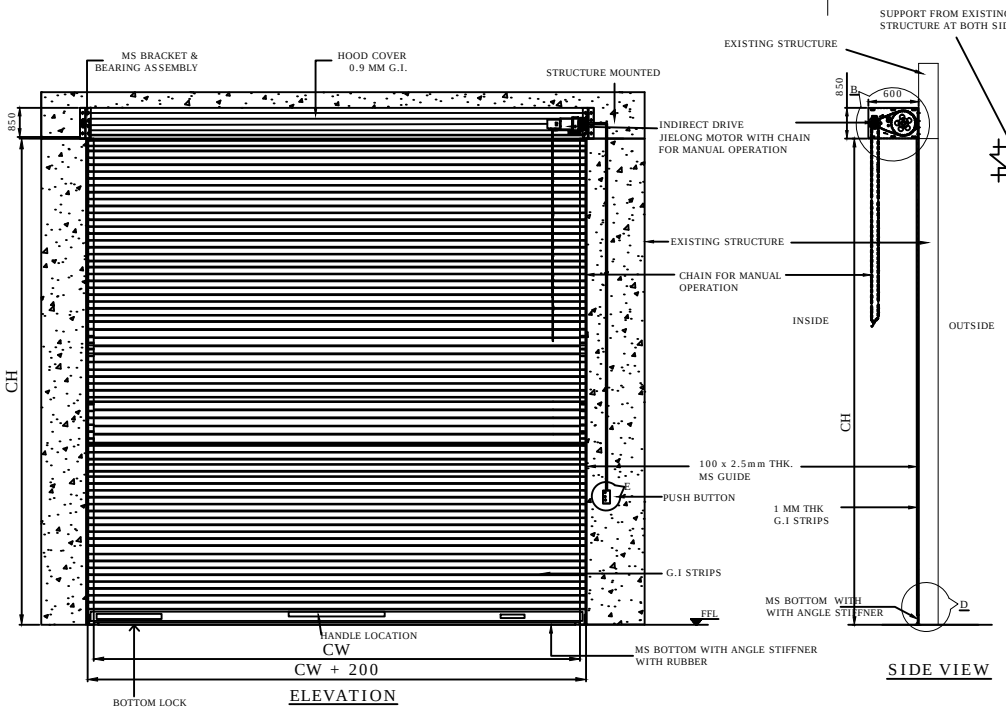


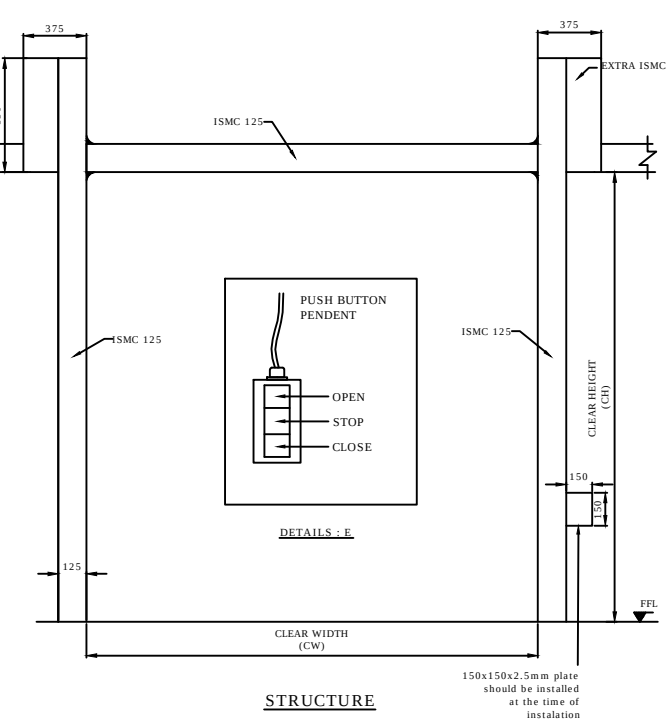


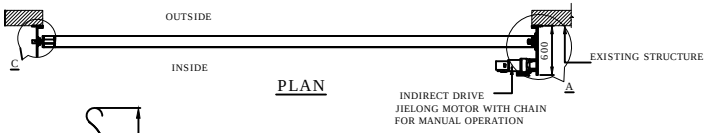

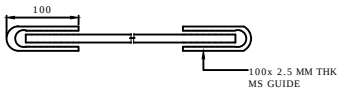

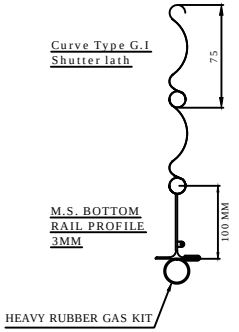

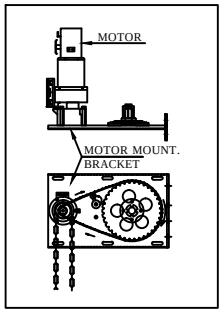

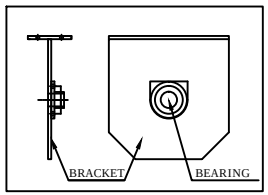

(NOTE: REQUIRED TECHNICAL STRUCTURE & CIVIL WORK FOR SHUTTER IN CLIENT SCOPE)

4500	5000	1	
CLEAR WIDTH (CW)	CLEAR HEIGHT (CH)	QUANTITY	RAL COLOR

This drawing & design is the property of NIHVA TECHNOLOGIES. Not to be sold or copied to any other concern.

TITLE: MOTORIZED ROLLING SHUTTER

	NAME	SIGN	DATE
DRAWN	S.M.S.		23.10.2020
CHECK	P.V.A.		23.10.2020
APPRD.			

NIHVA TECHNOLOGIES PVT. LTD.
NIHVA TECHNOLOGIES PVT. PUNE
Tel : 020 66304033
Email:- info@nihva.com
Website:- www.nihva.com

CLIENT - SPACONS EPC PVT LTD
PROJECT - SPACONS EPC PVT LTD
SITE LOCATION - PUNE
DWG. NO. : NIHVA/20-21/0067 REV- R01
If any queries contact : projectsupport@nihva.com
ALL DIMENSION ARE IN mm
SCALE: NTS WT: SHEET: