


PRODUCED BY AN AUTODESK EDUCATIONAL PRODUCT

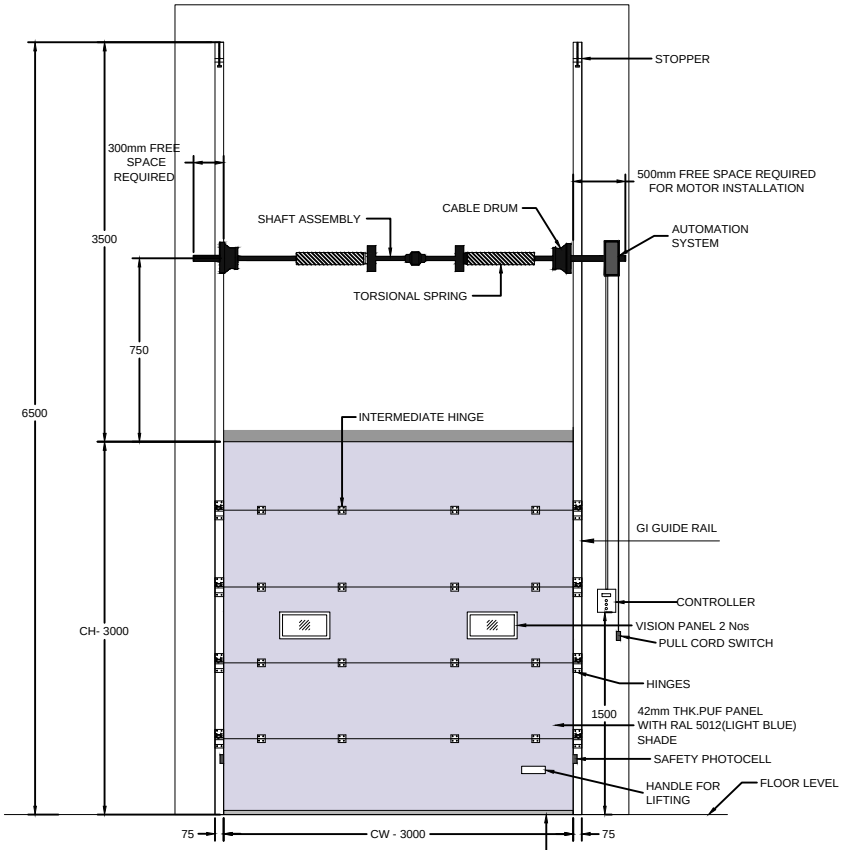


INSIDE ELEVATION

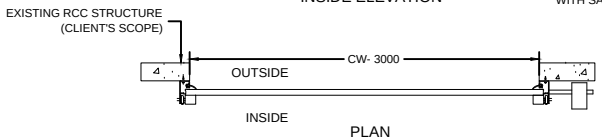

PLAN

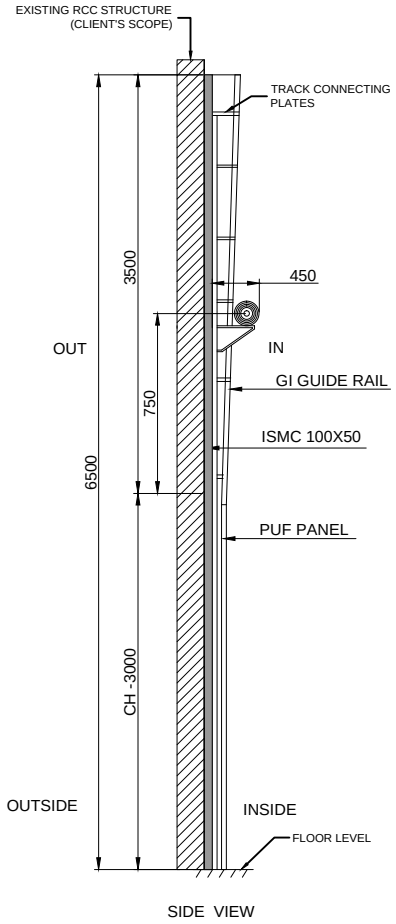

SIDE VIEW

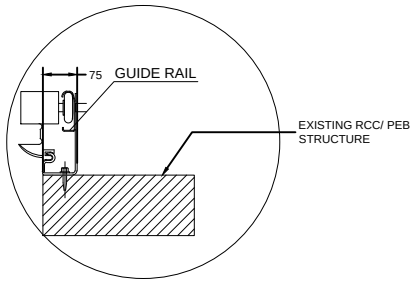

TRACK DETAILS

SR NO	CLEAR WIDTH (CW)	CLEAR HEIGHT (CH)	QUANTITY
1	3000	3000	2

DIMENSION :

CLEAR WIDTH	CLEAR HEIGHT	QUANTITY
3000 mm	3000 mm	2

TECHNICAL DATA :

COMPONENTS	MATERIALS	SPECIFICATIONS
DOOR PANELS	GI & PUF	42mm CFC- FREE POLYURETHANE WITH 0.5mm THK, GI PRECOATED PANELS.
DOOR HINGE	——	HEAVY DUTY HINGES FOR INTERLOCKING OF PANELS
SHAFT ASSEMBLY	STD.	TORSIONAL SPRING WITH SHAFT & BEARING PLATES
FINISH		RAL 9002 GREY WHITE

IMPORTANT NOTES:

1. REQUIRED STRUCTURE FOR DOOR SHALL BE IN CLIENT'S SCOPE.
2.SINGLE PHASE POWER SUPPLY REQUIRED AT DOOR LOCATION.
3.ALL CIVIL WORK SHALL BE CLIENT'S SCOPE.

NIHVA TECHNOLOGIES PVT. LTD. PUNE
Email:- info@nihva.com
Website:- www.nihva.com

TITLE:

SECTIONAL DOOR VL (MOTORIZED)
3x3m

CLIENT'S APPROVAL :

CLIENT - NESCO

PROJECT -

SITE LOCATION - MUMBAI

DWG. NO. : NIHVA/17-18/0298 | REV- 0

SCALE: NTS | WT: | SHEET:1 OF 1

DRAWN BY: OMKAR | DATE: 29-11-2017

CHECK BY: SHEKHAR | DATE: 29-11-2017

APPROVED BY : SHEKHAR | DATE: 29-11-2017

If any queries contact : projects@nihva.com

NOTE: ALL DIMENSIONS ARE IN mm

PRODUCED BY AN AUTODESK EDUCATIONAL PRODUCT

PRODUCED BY AN AUTODESK EDUCATIONAL PRODUCT

PRODUCED BY AN AUTODESK EDUCATIONAL PRODUCT