

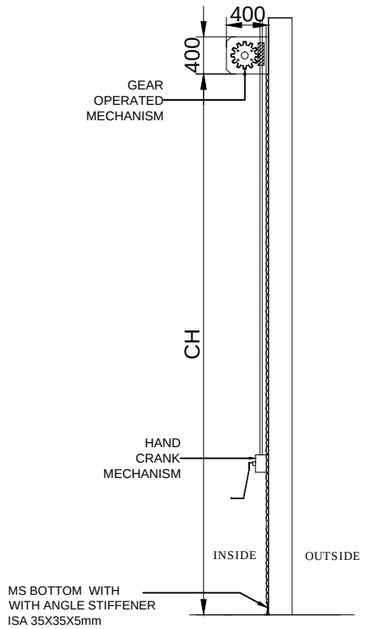



SIDE VIEW

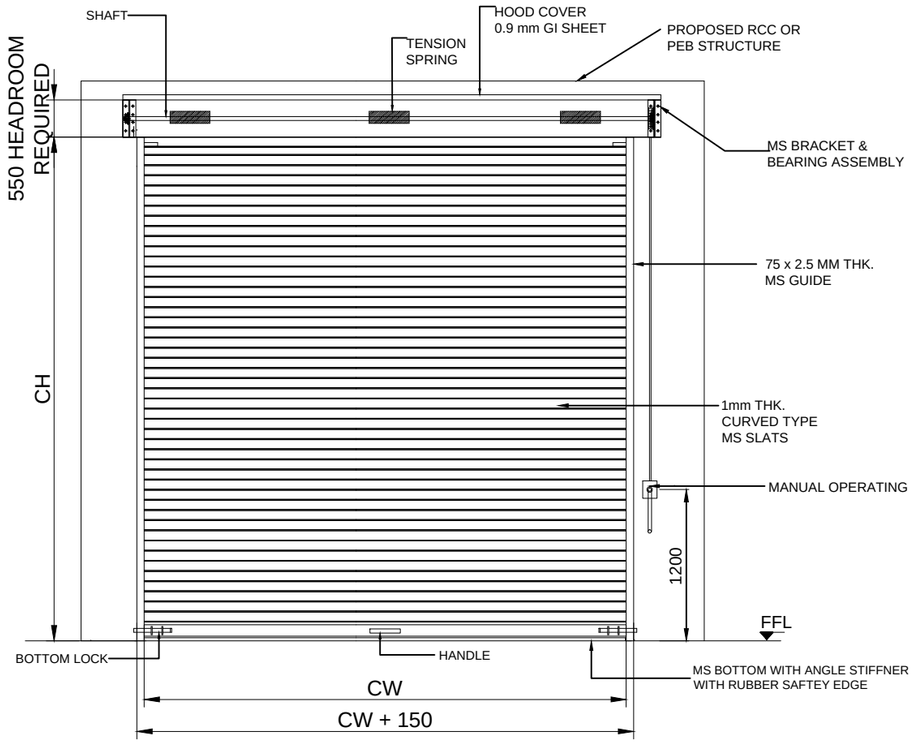


INSIDE ELEVATION

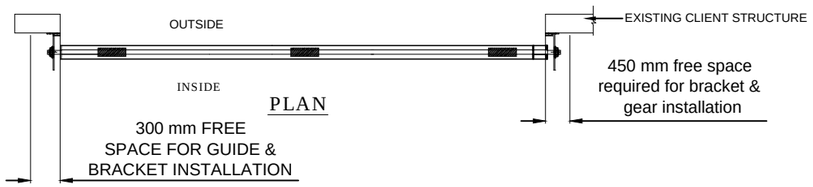


PLAN

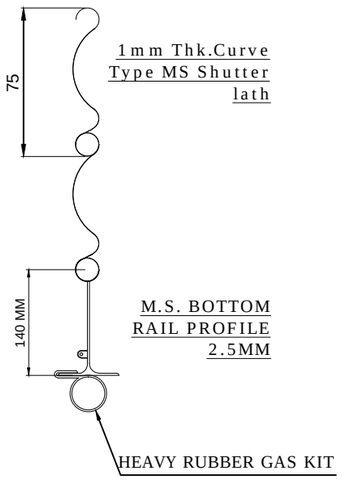

M.S. BOTTOM RAIL PROFILE 2.5MM

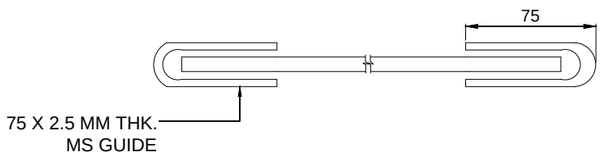

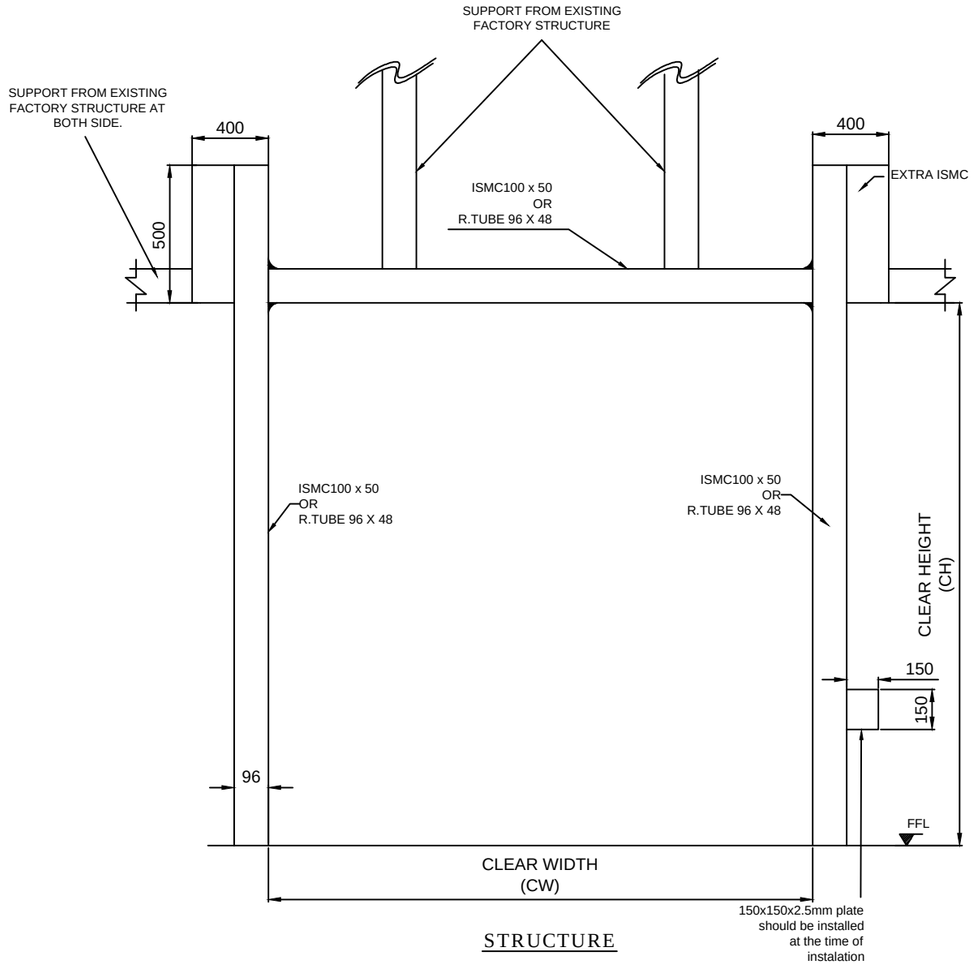

STRUCTURE

NOTE-
1. ALL CIVIL WORK WILL BE CLIENT'S SCOPE.
2. STRUCTURE REQUIRED FOR SHUTTER IS IN CLIENT'S SCOPE.

SR NO	(CW) CLEAR WIDTH	(CH) CLEAR HEIGHT	QUANTITY
1	3000	3010	01 NO

	RAL CODE	RAL COLOR	APPROVED
	RAL 9002	GREY WHITE	APPROVED

TOLERANCE - ±10mm

This drawing & design is the property of NIHVA TECHNOLOGIES. Not to be sold or copied to any other concern.

TITLE
GEAR OPERATED ROLLING SHUTTER

	NAME	SIGN	DATE
DRAWN	S.S.		14.09.2020
CHECK	P.A		14.09.2020
APPRD.			

If any queries contact : design@nihva.com

ALL DIMENSION ARE IN mm

NIHVA TECHNOLOGIES PVT. LTD.
Website:- www.nihva.com
NIHVA TECHNOLOGIES PVT. LTD. PUNE
Tel : 020 66304033
Email:- info@nihva.com

CLIENT - KAIZEN AIRTECH SOLUTIONS

PROJECT - VARROC ENGINEERING LTD.

SITE LOCATION - PUNE.

DWG. NO. : NIHVA/20-21/0054 | REV- R00

SCALE: NTS | WT: | SHEET: 01 OF 01