

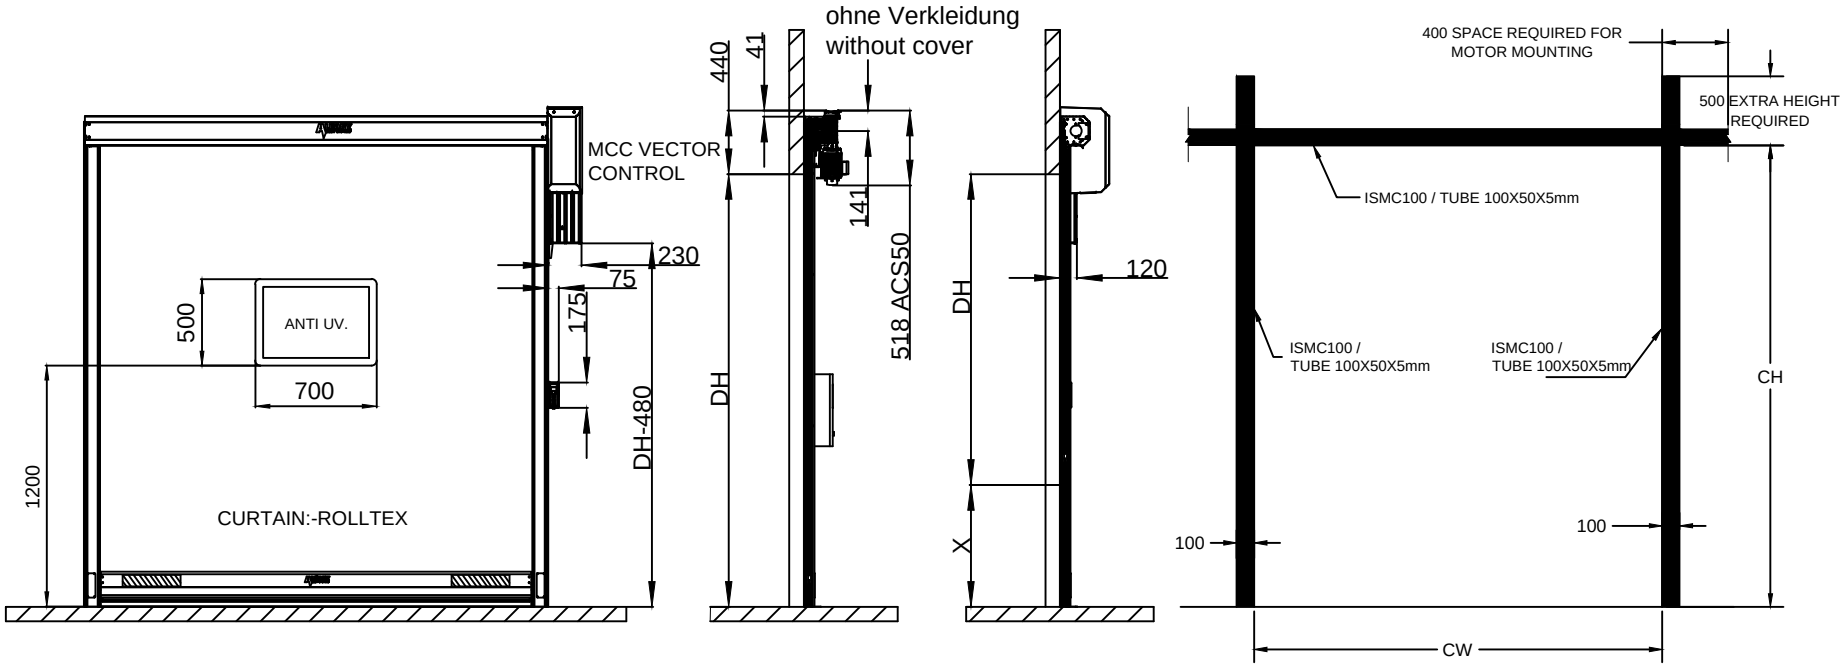


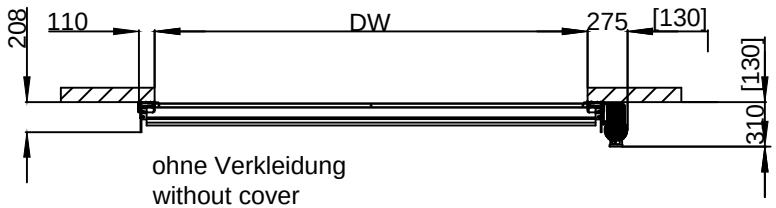

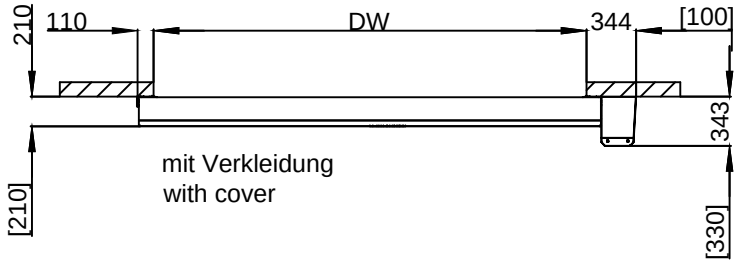

Tolerance ±3 mm (for all dimensions)
Dimensions in [ ] ==> clearance for installation

RAL : 5002 BLUE
CURTAIN:- ROLLTEX +

1800mm	2000mm	02 NOS
CLEAR WIDTH	CLEAR HEIGHT	QTY

NOTE : ALL REQ. CIVIL & TECHNICAL M.S STRUCTURAL WORK WILL BE IN CLIENT SCOPE.

This drawing & design is the property of NIHVA TECHNOLOGIES. Not to be sold or copied to any other concern.

TITLE	HIGH SPEED DOOR RP300 & STRUCTURE		
	NAME	SIGN	DATE
DRAWN	P.A		12.09.20
CHECK	G.J		12.09.20
APPV'ED			

NIHVA TECHNOLOGIES PVT. LTD.
NIHVA TECHNOLOGIES PVT. LTD. PUNE
Tel : 020 66304033
Email:- info@nihva.com
Website:- www.nihva.com

CLIENT :-
PROJECT :-
LOCATION :-

If any queries contact : design@nihva.com
ALL DIMENSION ARE IN mm

DWG. NO. :- NIHVA/20-21/VDR/0063 REV:-R00
SCALE: NTS WT: SHEET: 01 OF 01