


DRAWING

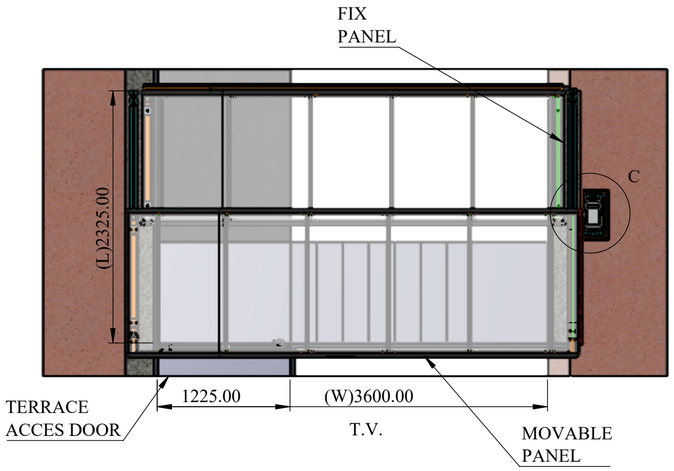


T.V.

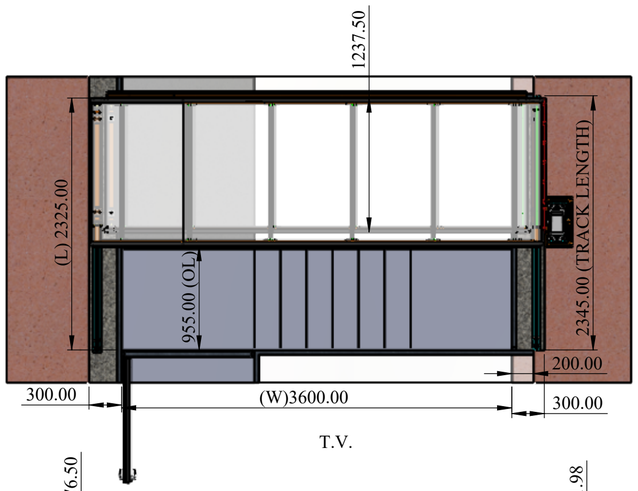


T.V.

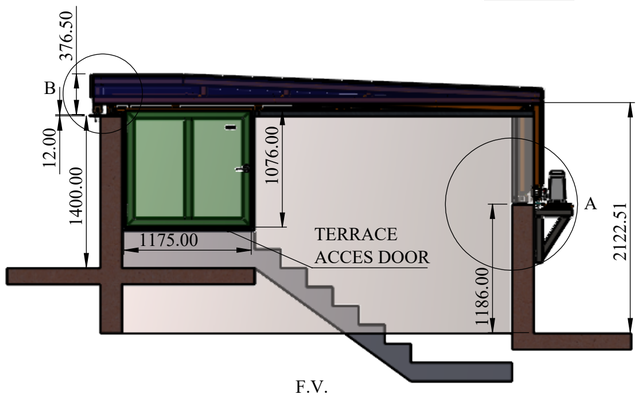

F.V.

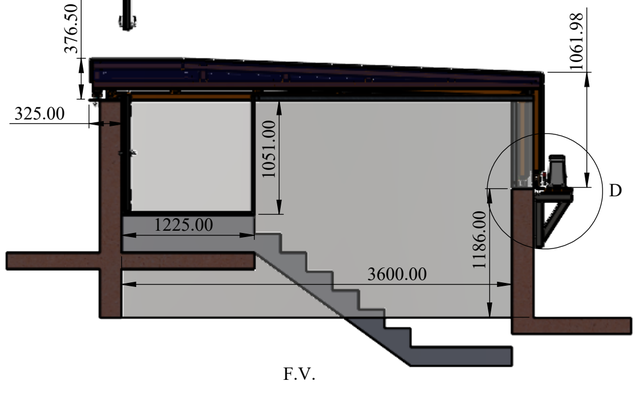


F.V.

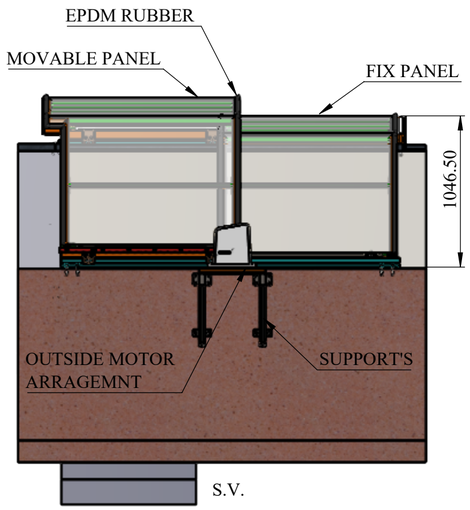


S.V.

CLOSE VIEW

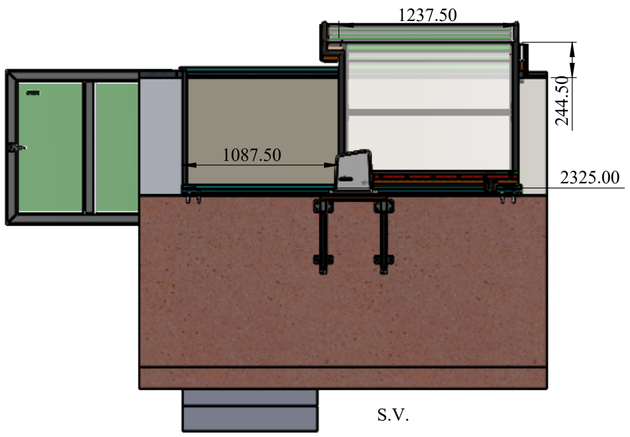


S.V.


OPEN VIEW

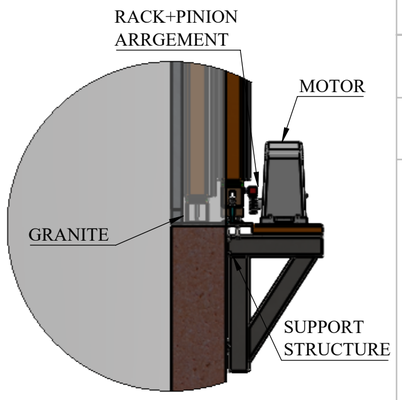


DETAIL A
SCALE 1 : 16

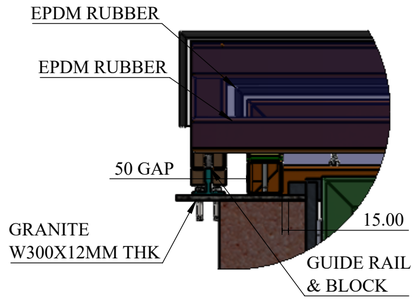

DETAIL B
SCALE 1 : 10

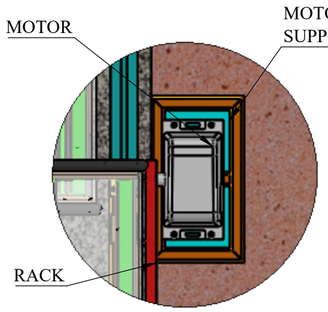

DETAIL C
SCALE 1 : 12

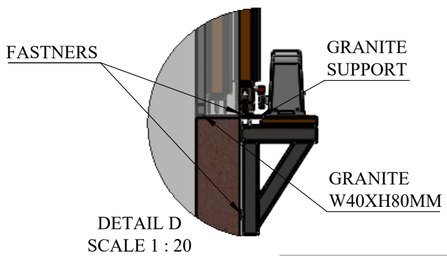

DETAIL D
SCALE 1 : 20

MOTOR MOUNTING
ARRANGEMENT

REV DESCRIPTION	DATE	REV NO
	19-08-2026	REV 00
1.		

NOTE :

THIS DRAWING IS ONLY FOR CLIENT APPORVAL
REQUIRED TRACK MOUNTING BASE STRUCTURE IN CLIENT SCOPE
EPDM RUBBER FLAPPER IS PROVIDED FOR AIR & WATER SEAL
TOTAL SYSTEM WEIGHT - 2,040 KG

SPECIAL INSTRUCTION'S :

PLEASE NOTE THAT IN CASE THE MOTOR NEEDS TO BE OPERATED MANUALLY,
YOU WILL HAVE TO ACCESS THE TERRACE THROUGH THE TERRACE DOOR & OPERATE
THE PANEL MANUALLY FROM OTSIDE.

This drawing & design is the property of NIHVA TECHONOLOGIES PVT. LTD. Not to be sold or copied to any other concern

TITLE - ROOF AUTOMATION

DWG NO - NTPL-

NIHVA TECHNOLOGIES PVT.LTD.PUNE
Website - www.nihva.com

	NAME	SIGNATURE	DATE
DRAWN	V.W.		19-08-2026
CHK'D	S.P.		21-08-2026
APPV'D	V.T.		21-08-2026

PRODUCT - RECTRACTABLE ROOF
CLIENT NAME - LODHA GROUP.
SITE LOCATION - MUMBAI - VIKROLI.
MATRIAL - QTY - 1

If any queries contact - info@nihva.com
ALL DIMENSION ARE IN mm A2
PROJECTION METHOD:
SCALE :
SHEET 1 OF 1