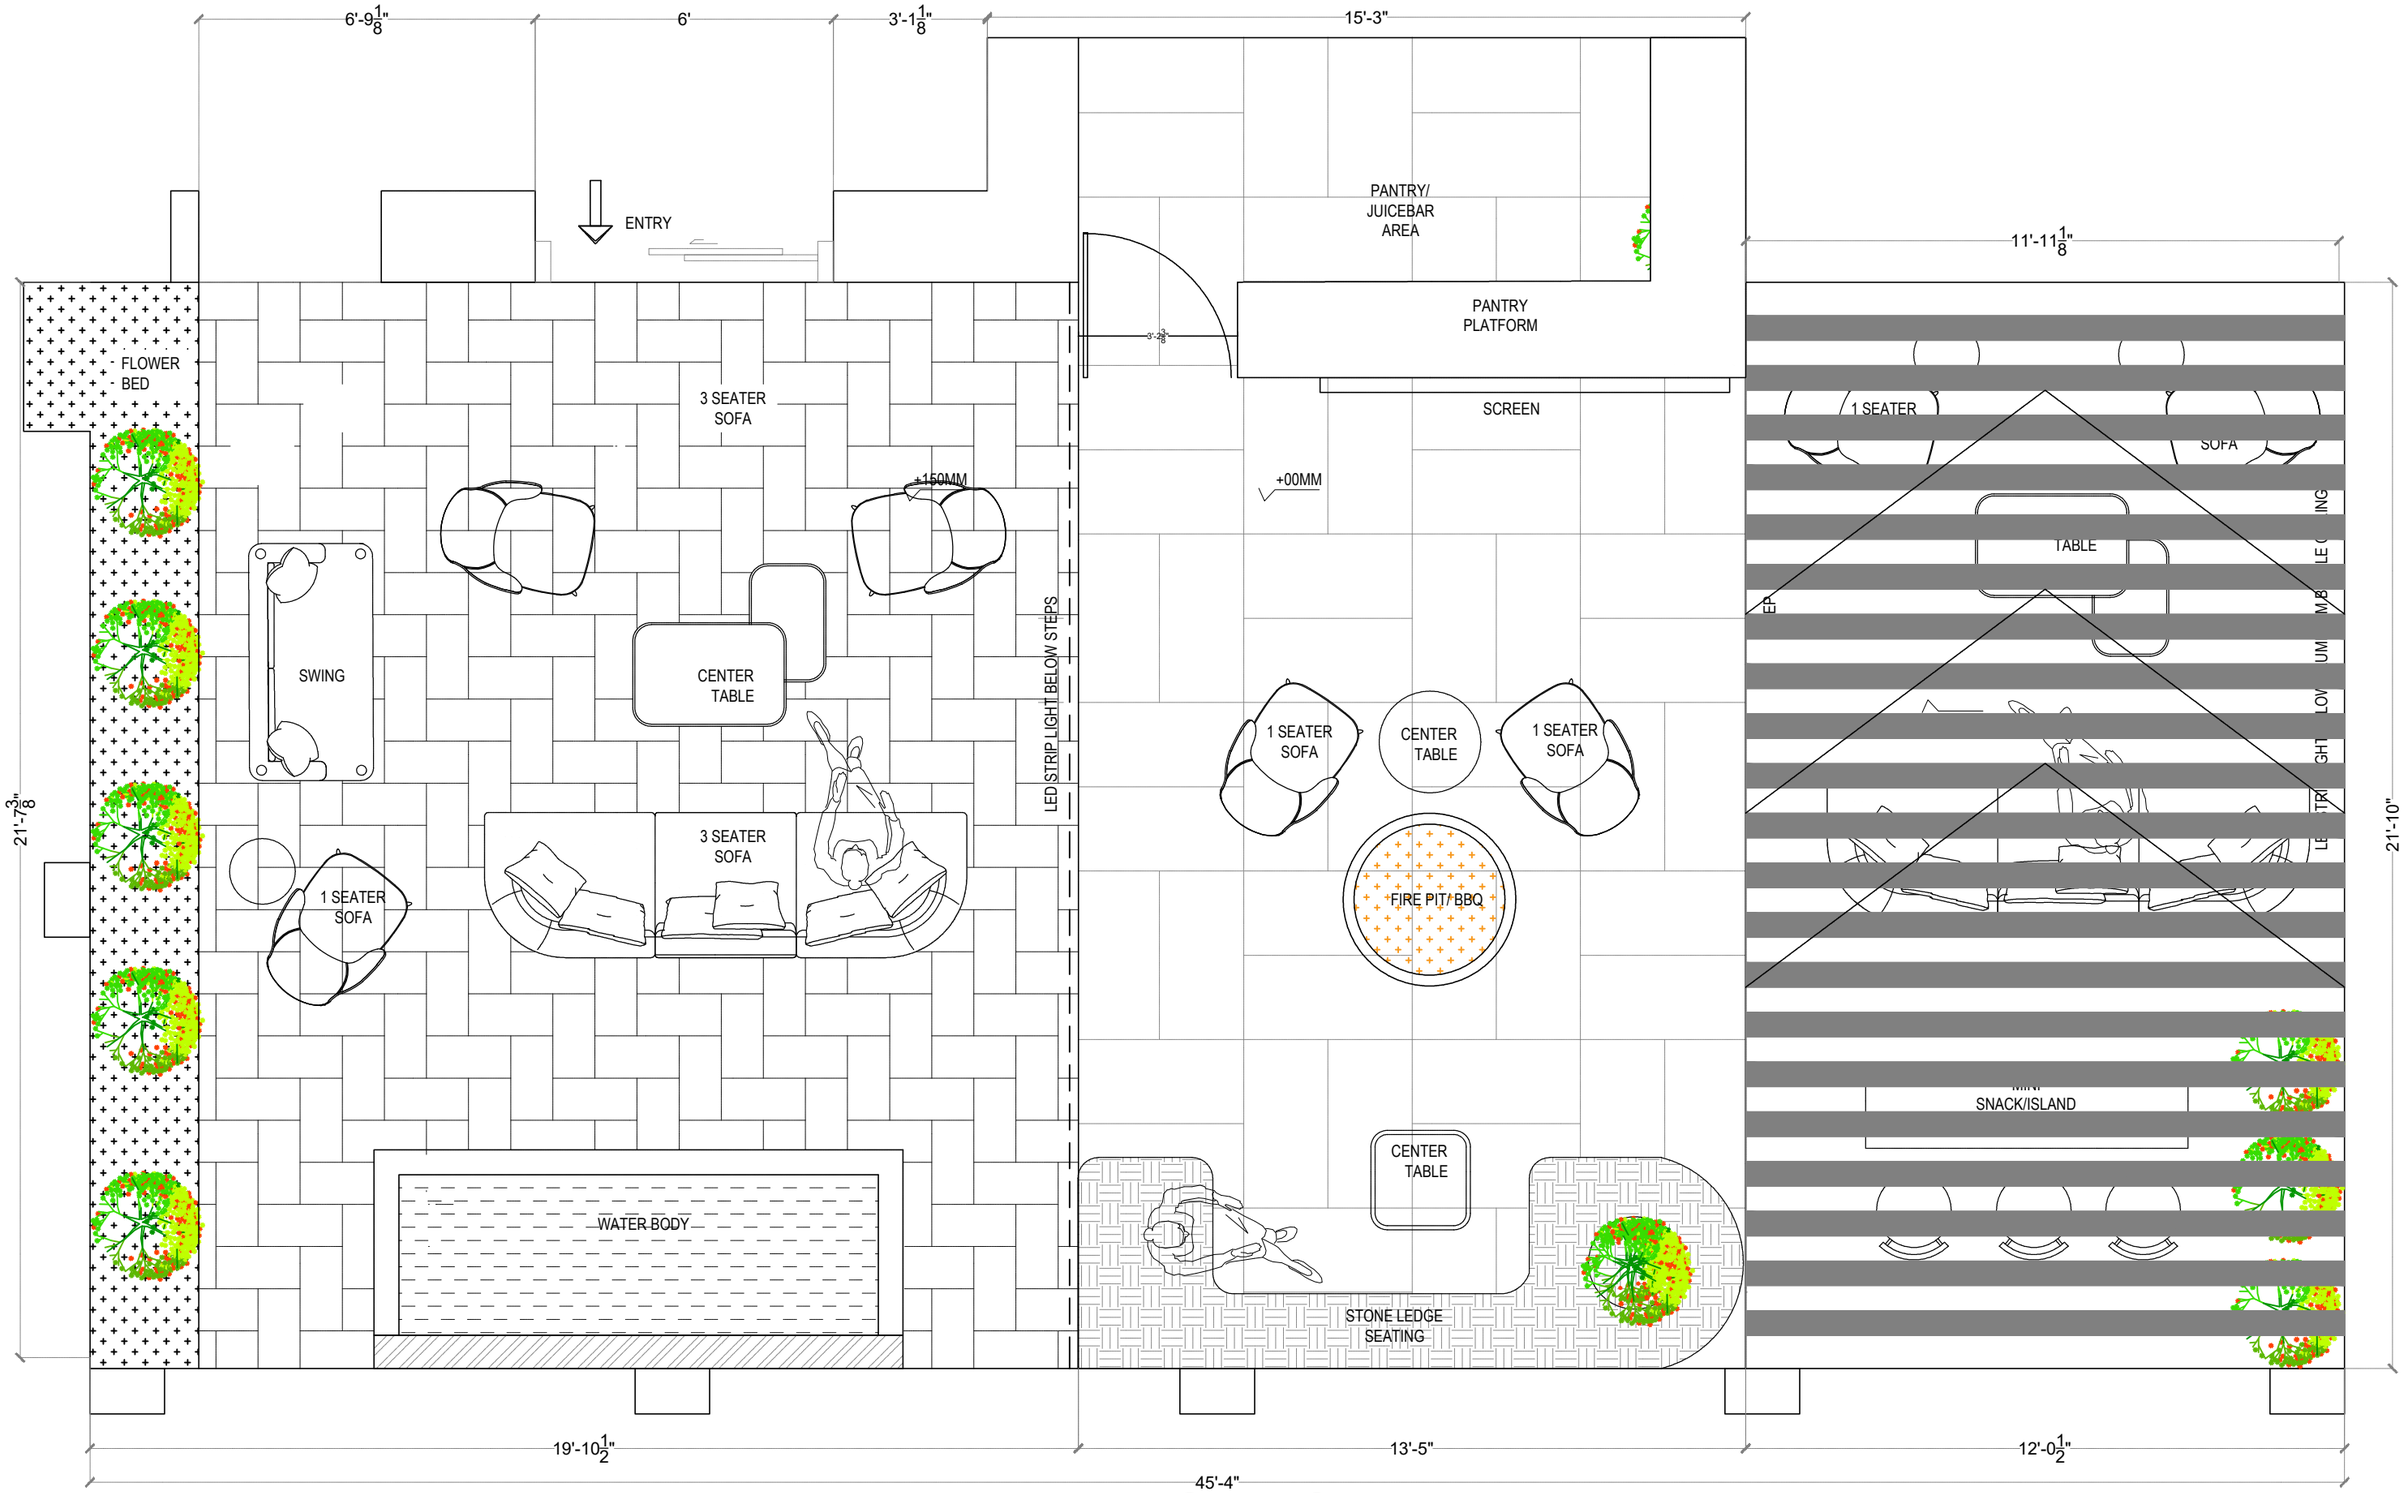


OPTION-01

CLIENT

FOR TENDERING ONLY
NOT FOR EXECUTION

AANTARIK DESIGN
ARCHITECTS & DESIGNERS

REFER TO COLOUR & MATERIAL SCHEDULE
REFER TO LOOSE FURNITURE DRAWING
REFER TO FITTINGS & SANITARY SCHEDULE
REFER TO ARTWORK SCHEDULE
LATEST REVISION OF DRAWING / SCHEDULE

REVISION	DESCRIPTION	DATE
R-01	REVISED LAYOUT	

ALL DIMENSIONS ARE IN FT.INCHES UNLESS SPECIFIED.DONOT SCALE DRAWINGS FOLLOW WRITTERN DIMENSIONS ONLY
CONTRACTOR MUST VERIFY THE MEASUREMENTS ON SITE AND REPORT ANY DISCREPENCY TO THE ARCHITECT.
THIS DRAWING SHOULD BE READ IN CONJUNCTION WITH ALL RELEVANT CONSULTANT'S DRAWINGS.
THIS DRAWING IS PROPERTY OF AANTARIK DESIGN AND IS NOT TO BE REPRODUCED, COPIED, HANDED OVER TO A THIRD PARTY OR USED FOR ANY PURPOSED.

PROJECT: —

DWG NO.: ID : 2297 | DD | LA 01

DATE: 08 MAY 2025 | SCALE: 3/16" = 1' @ A3 | REVISION: 00

DRAWN BY: AMIT | CHECKED BY: RAKESH | APPROVED BY: RAKESH

TITLE: TERRACE LAYOUT