


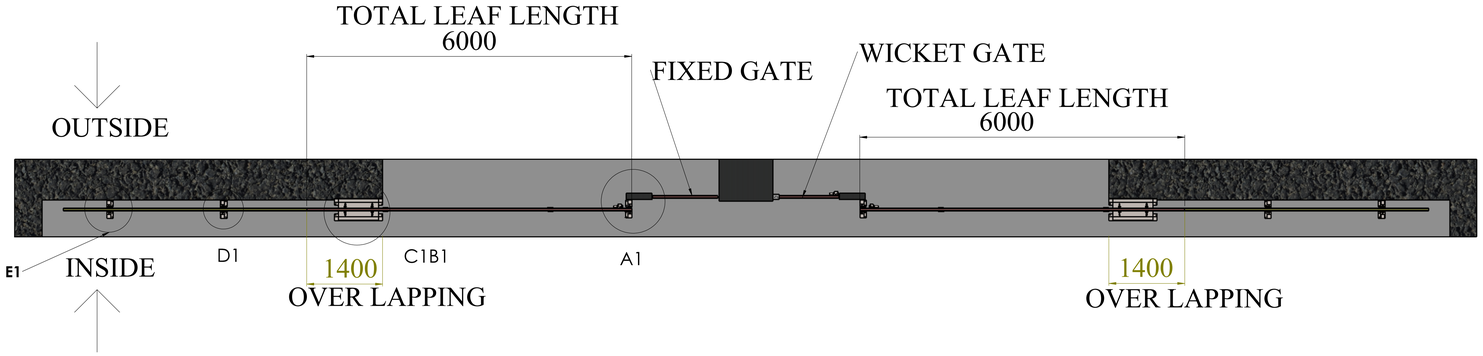


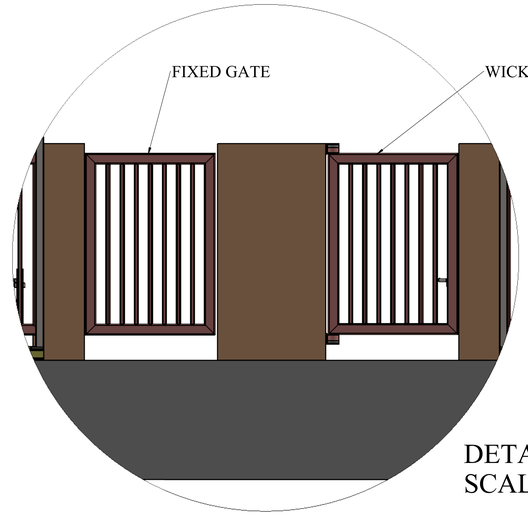


DETAIL E1
SCALE 1 : 20

FIXED GATE AND SWING
GATE VIEW

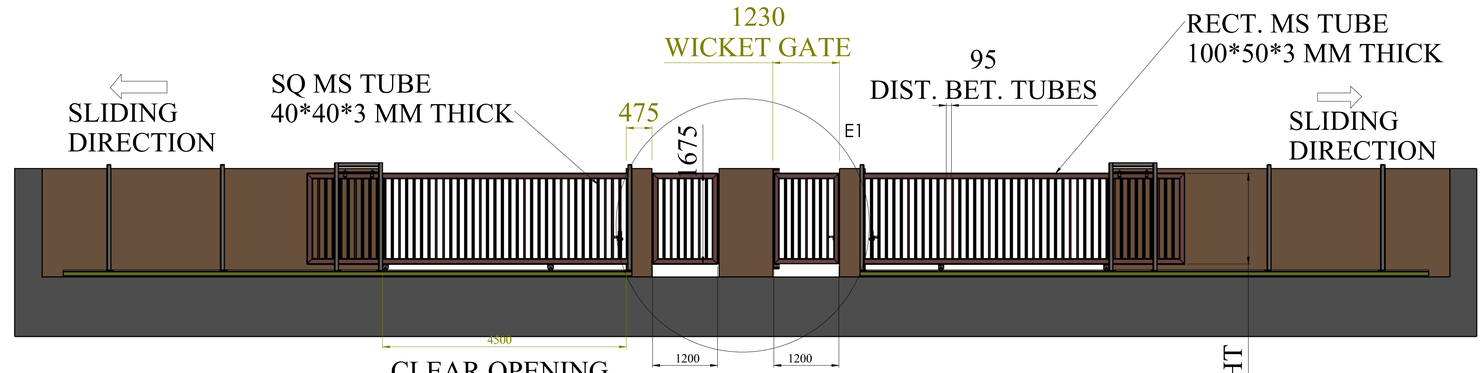


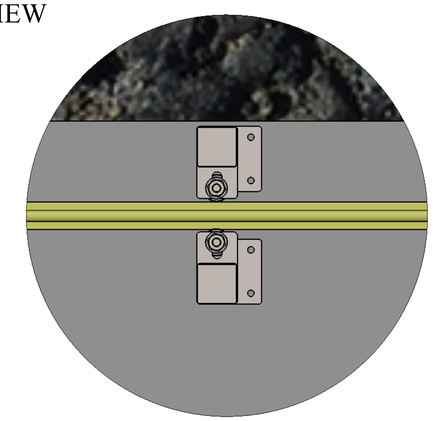

DETAIL D1
SCALE 1 : 4

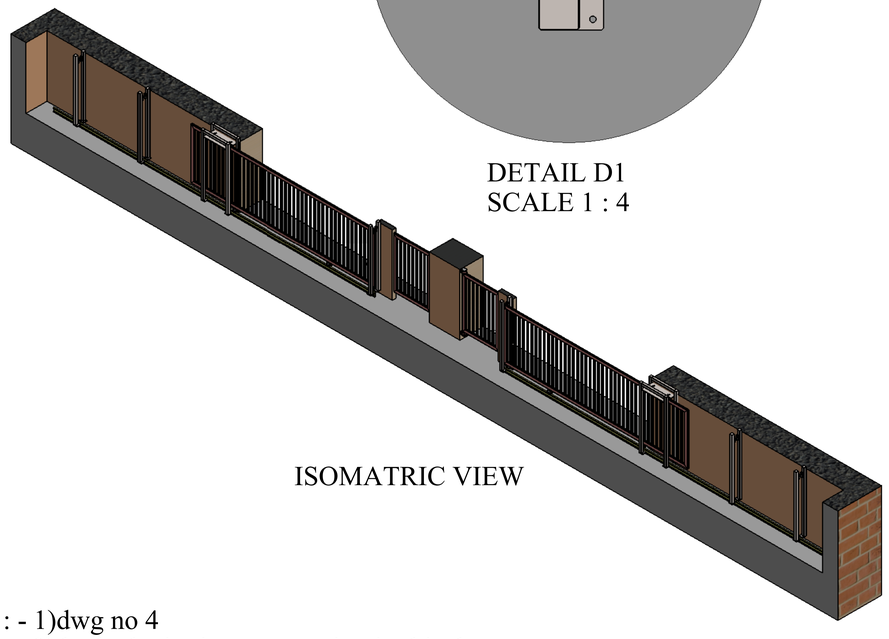


ISOMATRIC VIEW

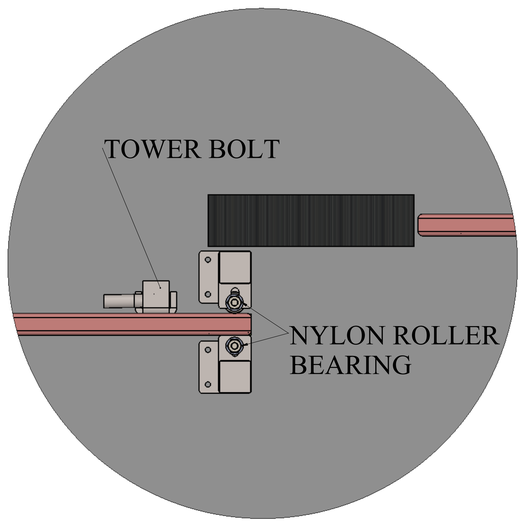

POST 1 AND NYLON ROLLER
BEARING ASSEM.

DETAIL A1
SCALE 1 : 5

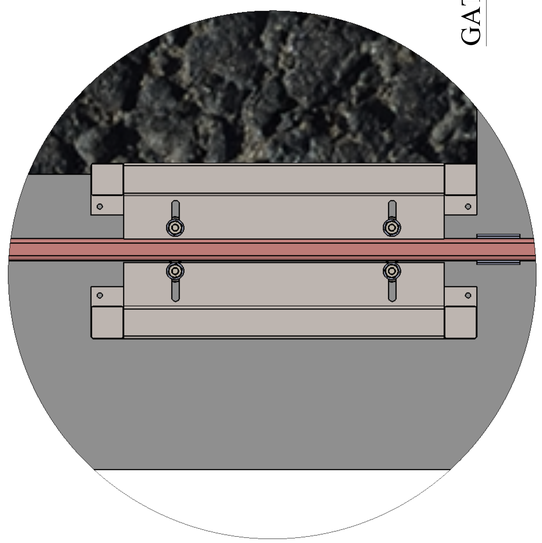

POST 2 AND NYLON ROLLER
BEARING ASSEM.

DETAIL C1B1
SCALE 1 : 5

Note : - 1)dwg no 4
2) barbed wire is not menstion in this dwg.
3)Total column -04 (A1,B1,C1,D1)
4) 03 column posts when the gates is in the closed position.(A1,B1,C1)
5) 03 column posts when the gates is in the fully open position.(B1,C1,D1,E1)

UNLESS OTHERWISE SPECIFIED: DIMENSIONS ARE IN MILLIMETERS SURFACE FINISH: TOLERANCES: LINEAR: ANGULAR:			FINISH:			DEBURR AND BREAK SHARP EDGES	DO NOT SCALE DRAWING	REVISION
	NAME	SIGNATURE	DATE				TITLE:	
DRAWN								
CHK'D								
APPV'D								
MFG								
Q.A								
			MATERIAL:				DWG NO.	
			WEIGHT:				SCALE:1:100	SHEET 1 OF 1

SBFINAL ASSM. GA DRAWING (TYPE NO 04