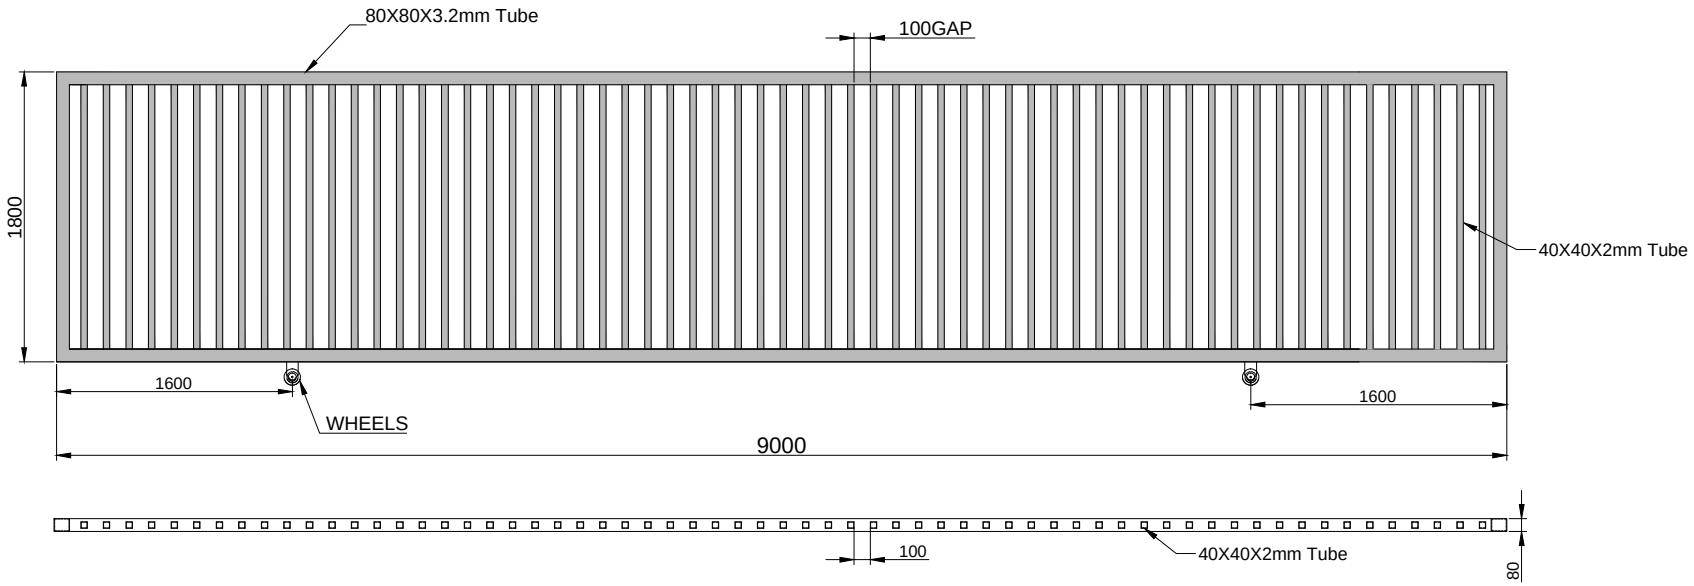

NOTE-
1. ONE COAT OF RED OXIDE & TWO COAT OF APPROVED RAL SHADE WILL BE GIVEN TO THE GATE.

Sr.no		Specification	QTY
01	OUTER TUBE	MS TUBE 80 X 80 X 3.2mm	22 m
02	INNER TUBE	MS TUBE 40 X 40 X 2mm	105 m
03	GAP IN TUBE	100mm	
04	WHEEL	WHEEL WITH BRACKET	02 NOS

QTY :- 01 NOS
MATERIAL :-MS

This drawing & design is the property of NIHVA TECHNOLOGIES. Not to be sold or copied to any other concern.

TITLE: AUTOMATIC SINGLE LEAF SLIDING GATE (6)

NIHVA TECHNOLOGIES PVT. LTD. PUNE
Tel : 020 66304033
Email:- info@nihva.com
Website:- www.nihva.com

	NAME	SIGN	DATE
DRAWN	S.L		30/08/18
CHECK	P.A		30/08/18
APPROVAL	R.D		30/08/18

If any queries contact : design@nihva.com

ALL DIMENSION ARE IN mm

CLIENT -
PROJECT -
SITE LOCATION -
DWG. NO.:-NIHVA/18-19/VDR/102
REV. :-0
SCALE: NTS
WT:
SHEET: 01 OF 01