

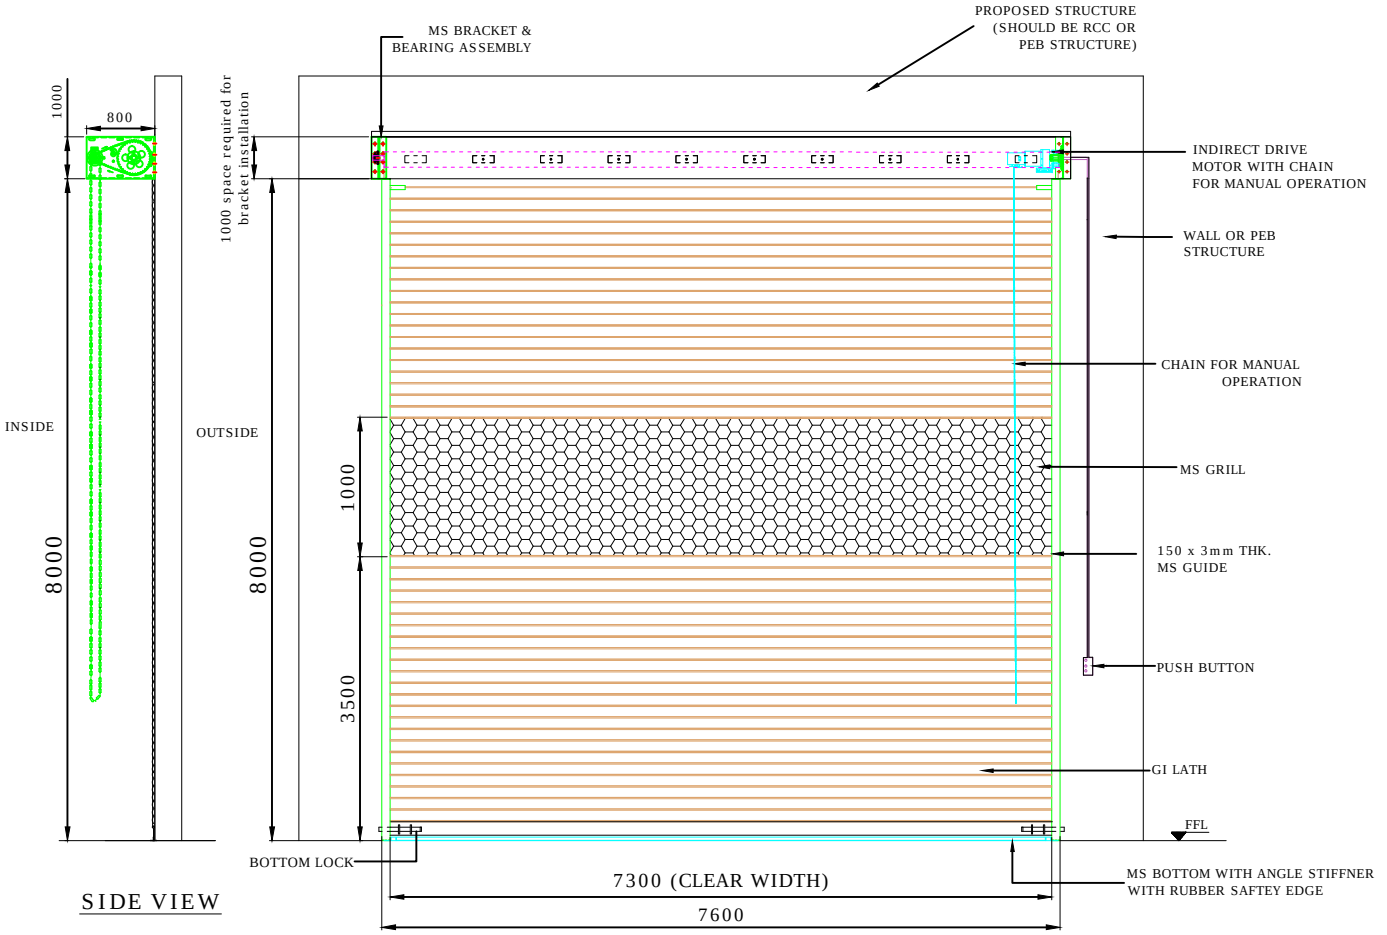



SIDE VIEW

ELEVATION

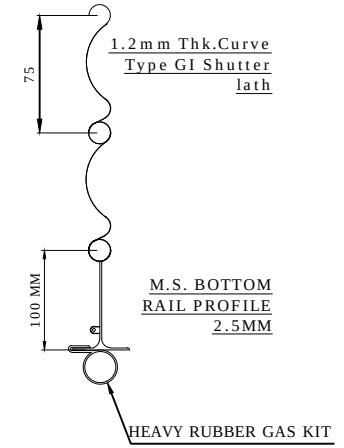

M.S. BOTTOM RAIL PROFILE 2.5MM

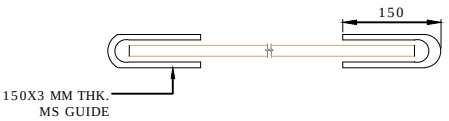

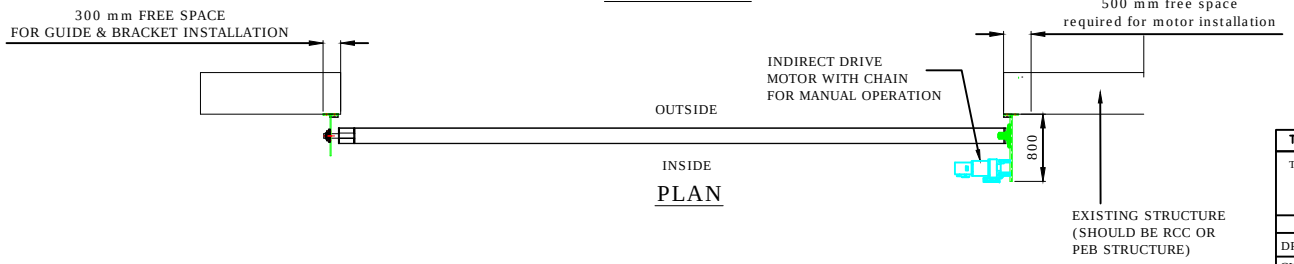

PLAN

COLORS:-
1. RAL7035 LIGHT GRAY.
2.RAL9001 CREAM WHITE.
3.RAL9010 PURE WHITE.

NOTE:-
1.REQUIRED STRUCTURE FOR ROLLING SHUTTER SHALL BE IN CLIENT SCOPE.
2.ALL REQUIRED CIVIL WORK IN CLIENT SCOPE.
3.3 PHASE POWER SUPPLY SHOULD BE PROVIDED.
4.CLIENT HAS TO SELECT RAL COLOR SHADE FROM GIVEN OPTION.

CLEAR WIDTH (CW)	CLEAR HEIGHT (CH)	QUANTITY
7300	8000	1

This drawing & designing is the property of NIHVA TECHNOLOGIES. Not to be sold or copied to any other concern.

TITLE
MOTORIZED ROLLING SHUTTER

NIHVA TECHNOLOGIES PVT. LTD. PUNE
Tel : 020 66304033
Email:- info@nihva.com
Website:- www.nihva.com

	SIGN	DATE
DRAWN	SURAJ	14/09/17
CHECK	SAGAR	14/09/17
APPROVAL	SHEKHAR	14/09/17
REV.		

If any queries contact : projects@nihva.com

ALL DIMENSION ARE IN mm

CLIENT -S.S.GHORPADE
PROJECT -ROSS PROCESS EQUIPMENT PVT. LTD.
SITE -CHAKAN
DWG. NO. : NIHVA/17-18/0203
SCALE: NTS | WT: | SHEET: 01 OF 01