

PRODUCED BY AN AUTODESK EDUCATIONAL PRODUCT

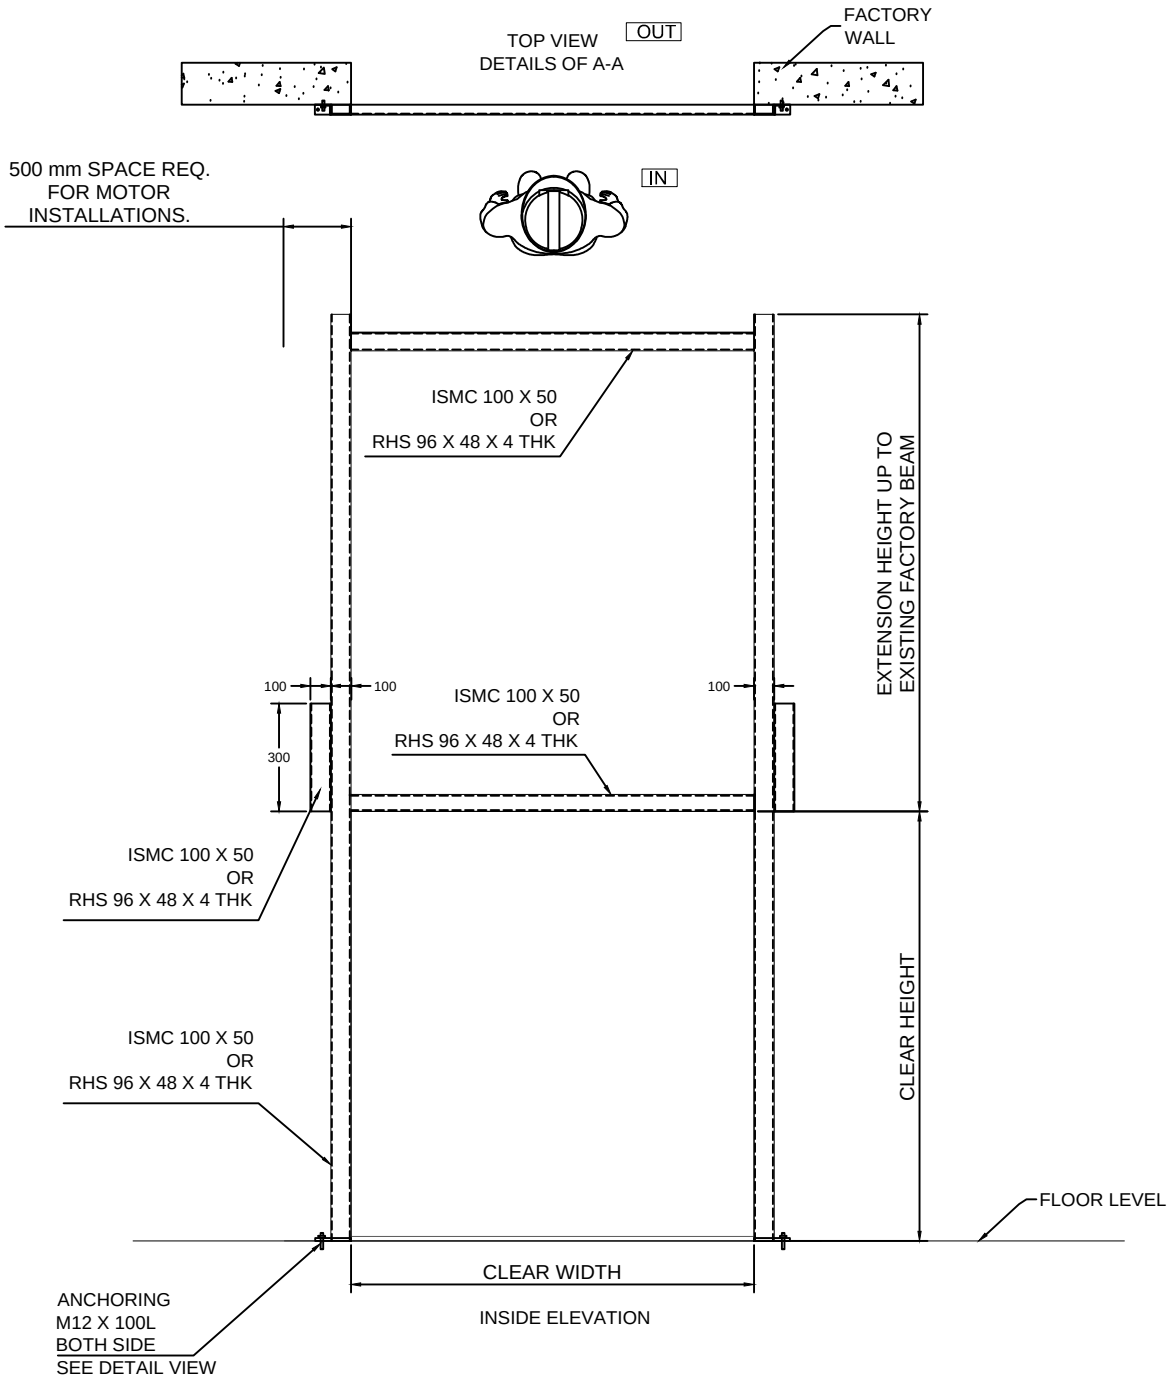

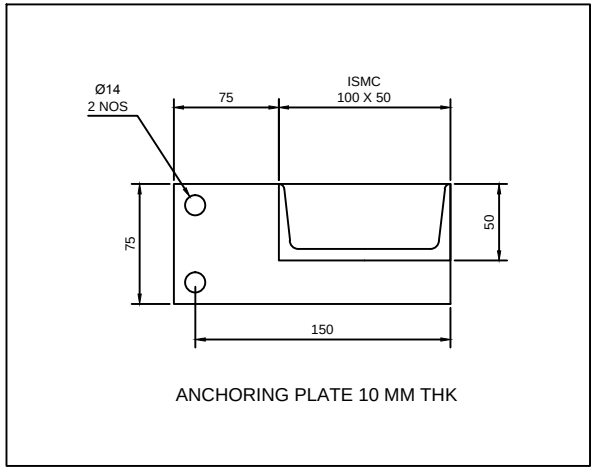

SR NO	CLEAR WIDTH	CLEAR HEIGHT	QTY
01	2400mm	3000mm	1

NOTE : REQ. M.S STRUCTURE FOR DOOR INSTALLATION WILL BE IN CLIENT SCOPE.

TOLERANCE: 10mm

This drawing & design is the property of NIHVA TECHNOLOGIES. Not to be sold or copied to any other concern.

TITLE: SECTIONAL DOOR (HL) STRUCTURE

NIHVA TECHNOLOGIES PVT. LTD. PUNE
Tel : 020 66304033
Email:- info@nihva.com
Website:- www.nihva.com

	NAME	SIGN	DATE
DRAWN	P.A		05.06.20
CHECK	G.J		05.06.20
APPROVAL			

CLIENT - RMK INFRASTRUCTURE

PROJECT -

SITE -

If any queries contact : design@nihva.com

DWG. NO. : NIHVA/20-21/0029 REV: R00

ALL DIMENSION ARE IN mm

SCALE: NTS WT: SHEET: 01 OF 01

PRODUCED BY AN AUTODESK EDUCATIONAL PRODUCT