



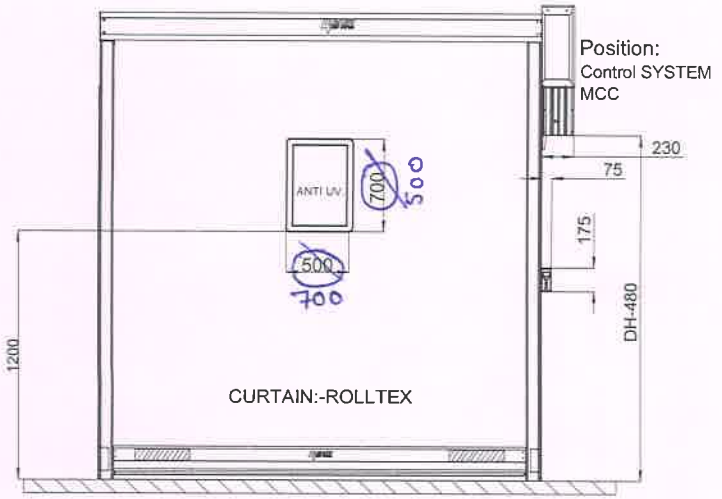


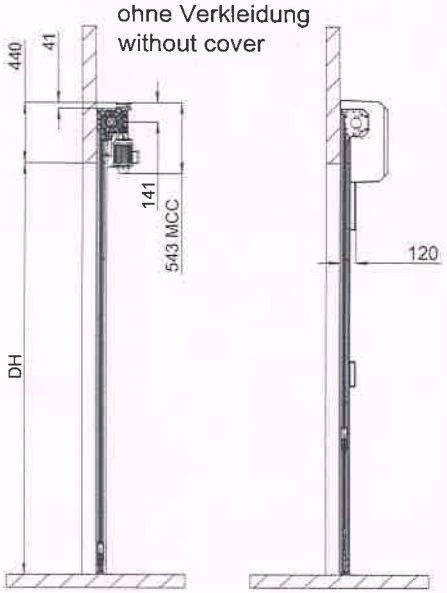

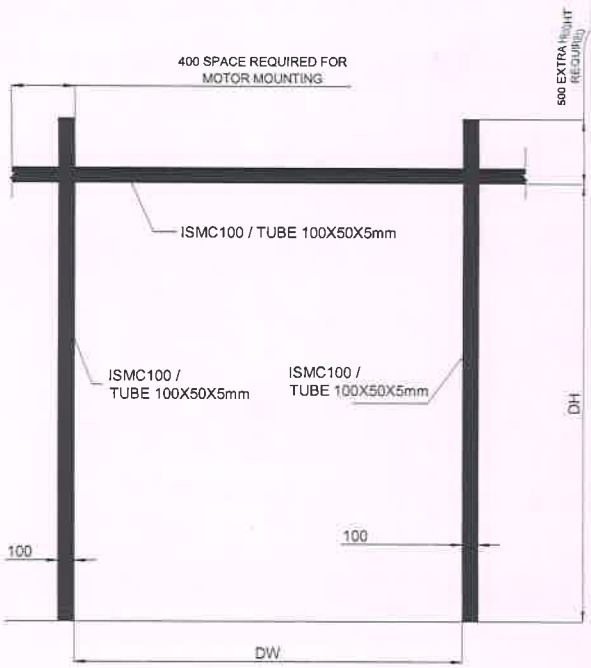

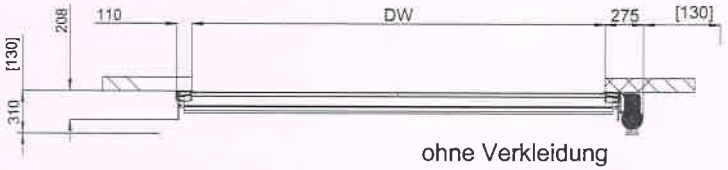

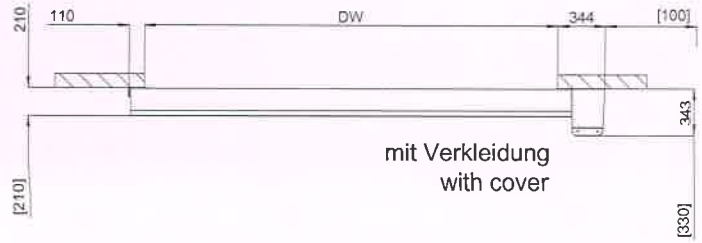

* Please Go ahead for manufacturing with modifying window size.

* Albany door with including running sensor.

7/9/19

Tolerance ±3 mm (for all dimensions)
Dimensions in [ ] ==> clearance for installation

RAL : 5002 BLUE

CLEAR WIDTH(DW)	CLEAR HEIGHT(DH)	QTY
4000mm	2500mm	01 NOS

NOTE : ALL CIVIL & STRUCTURAL WORK WILL BE IN CLIENT SCOPE.

TITLE	HIGH SPEED DOOR RP300 & STRUCTURE		
	NAME	SIGN	DATE
DRAWN	P.V.A		06.09.19
CHECK	V.M.T		06.09.19
APPVED			

If any queries contact : design@nihva.com

ALL DIMENSION ARE IN mm

NIHVA TECHNOLOGIES PVT. LTD.

NIHVA TECHNOLOGIES PVT. LTD. PUNE
Tel : 020 66304033
Email - info@nihva.com
Website :- www.nihva.com

CLIENT :- FINEARC SYSTEMS PVT LTD

PROJECT :-

LOCATION :- PUNE.

DWG. NO. :- NIHVA/19-20/0086 REV.-00

SCALE: NTS | WT: | SHEET: 01 OF 01