






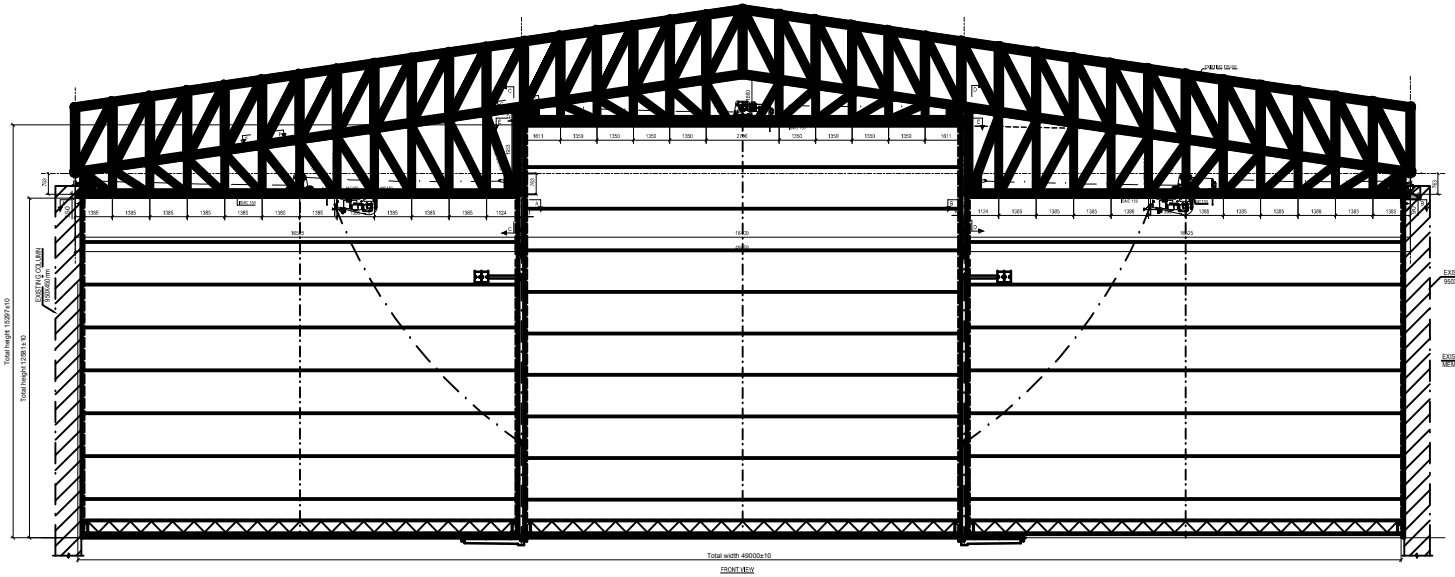

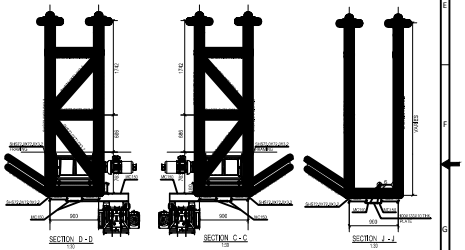

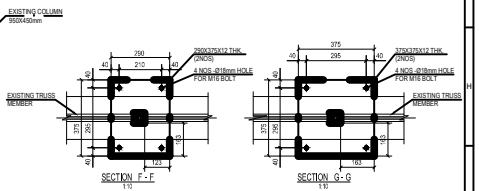

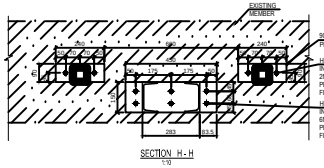

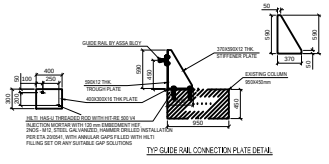

REV.NO.	DESCRIPTION.	REV.DATE	DRAWN.	CHKD.	APPD.

DWG.TITLE :- STRUCTURAL DRAWING FOR DOOR FRAME

PROJECT	HANGER DOOR
CLIENT	Cochin International Airport

NIHVA TECHNOLOGIES PVT. LTD.

NIHVA TECHNOLOGIES PVT LTD, PUNE
Tel: 02066304033 , website: www.nihva.com
email:-info@nihva.com

DRAWN :KPL	CHECKED : HAB	SCALE: 1:100
APPROVED : HAB	JOB CODE. : 1714	DATE: 14.07.2022
DWG.NO: NIHVA/22-23/CLT/0075	(SH-1OF1)	REV. - R0 SIZE. - A0

A1 (841 x 594)