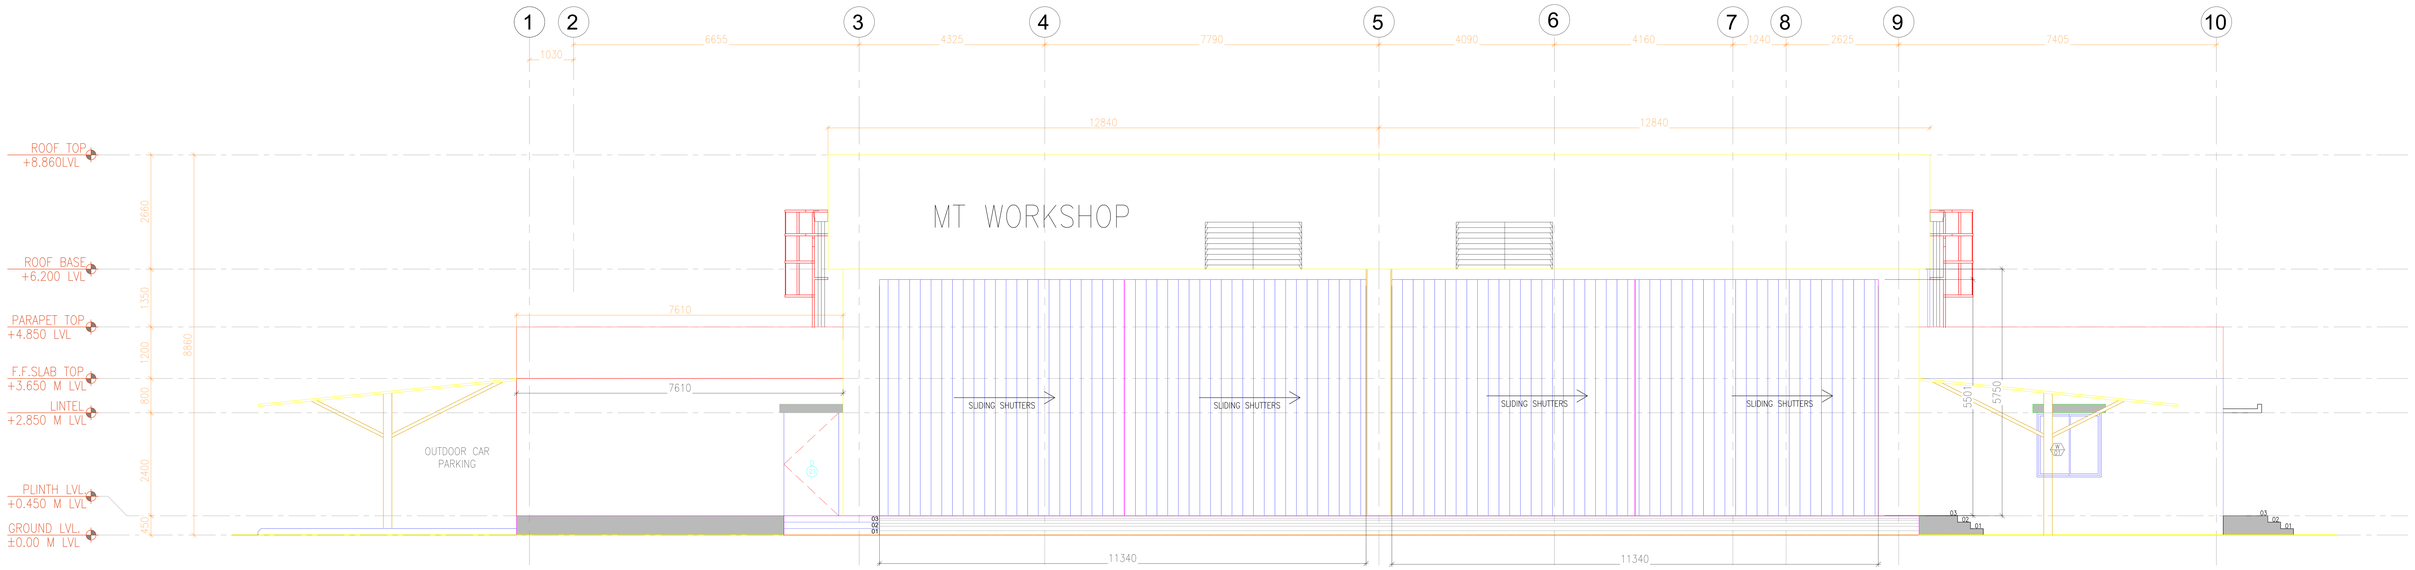

1
2
3
4
5
6
7
8
9
10
1030
6655
4325
7790
4090
4160
1240
2625
7405
12840
12840
ROOF TOP
+8.860LVL
ROOF BASE
+6.200 LVL
PARAPET TOP
+4.850 LVL
F.F.SLAB TOP
+3.650 M LVL
LINTEL
+2.850 M LVL
PLINTH LVL
+0.450 M LVL
GROUND LVL.
±0.00 M LVL
2660
1350
8860
1200
800
2400
450
MT WORKSHOP
7610
7610
OUTDOOR CAR
PARKING
SLIDING SHUTTERS
SLIDING SHUTTERS
SLIDING SHUTTERS
SLIDING SHUTTERS
5501
5750
03
02
01
11340
11340

ELEVATION–A