

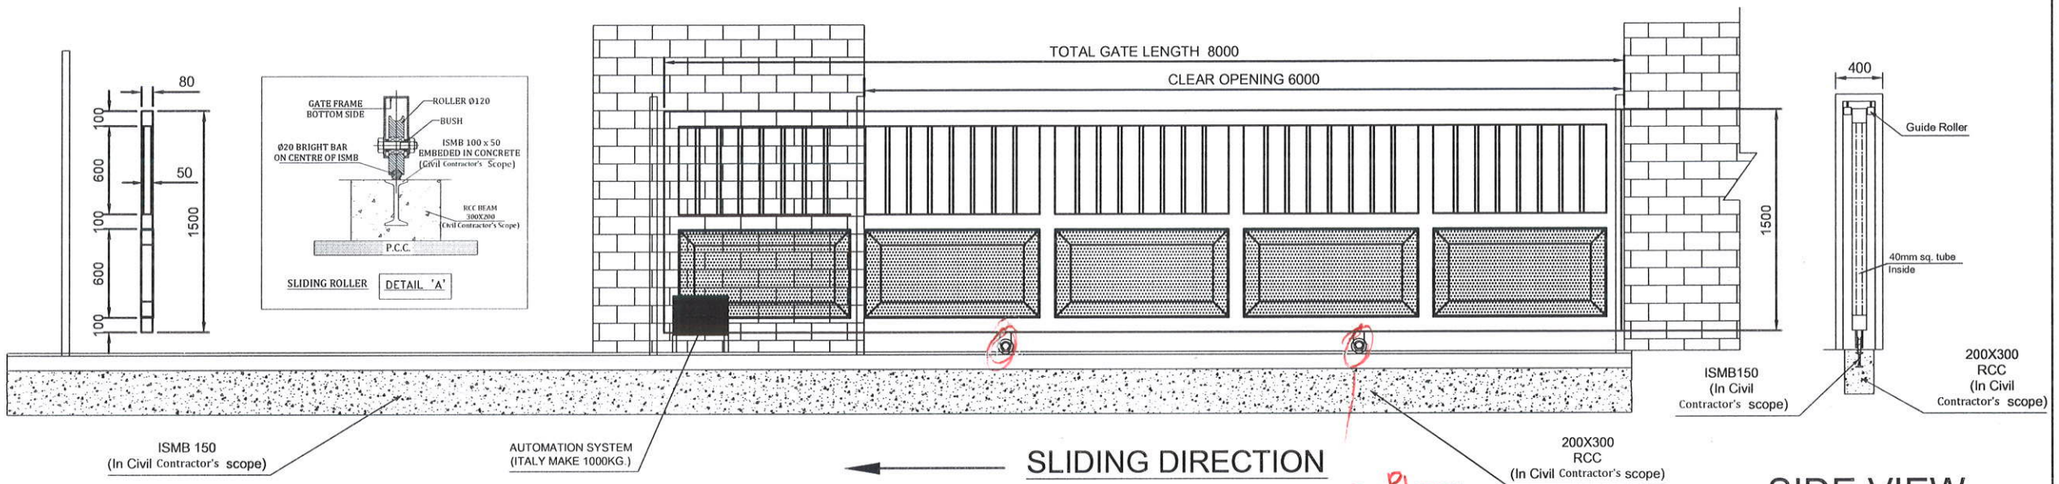


Please check if no. of wheeler are adequate

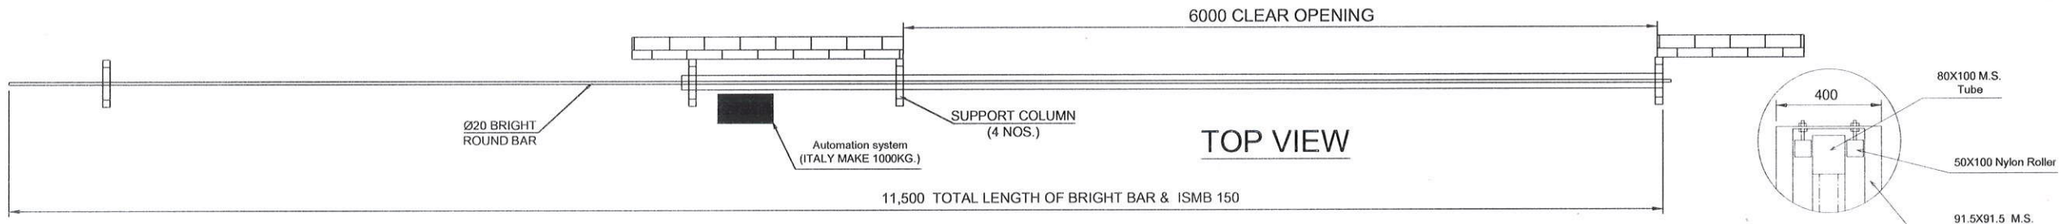

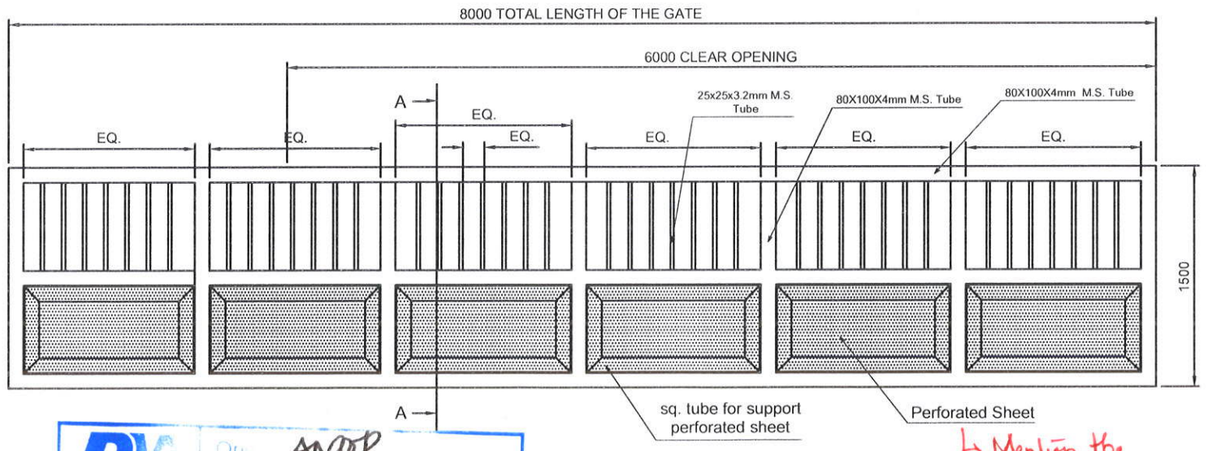

Mention the thickness

Clear Opening size	- 6000X1500mm
Total length of gate	- 8000X1500mm
No. Of Column	- 4 nos.
Factory paint finish	- Red oxide primer coat
NOTE :-	*ALL REQ. CIVIL WORK WILL BE IN YOUR CONTRACTOR'S SCOPE.

★ will be as per specification

☑ FINAL CERTIFIED

This drawing & designing is the property of NIHVA TECHNOLOGIES. Not be sold or copy to any other concern.

TITLE	MOTORIZED SLIDING GATE		NIHVA TECHNOLOGIES PVT. LTD.
	SIGN	DATE	
DRAWN	ABHIJIT	28/10/15	CLIENT - REWARD CONSTRUCTION
CHECK	ANIL	28/10/15	PROJECT - GIVAUDAN
REV.	03		SITE - RANJANGAON MIDC
APPROVAL			DWG. NO. : NIHVA/15-16/105
If any queries contact : projects@nihva.com			SCALE: 01 / WT: / SHEET: 01 OF 01
ALL DIMENSION ARE IN mm			

NIHVA TECHNOLOGY PVT. LTD. PUNE
Tel : 020 66304033
Email:- info@nihva.com
Website:- www.nihva.com

PVA GROUP
Org. ANTOP
Status of No. 3
Date 3/11/2015
COLLATED COMMENTS AND STATUS CODES
☐ 1. Document is unacceptable revise and re submit
☐ 2. Incorporate Comments and re submit
☑ 3. Re-submit as "Final certified" work may proceed in Accordance with the contract (with comments alleinded)
☐ 4. No comment Work may proceed in accordance with the contract

★ is a repeated comment.
Pls confirm and respond ASAP.